

19' WIDE ROAD

This drawing, design & content is property of Architect and shall not be used, copied or reproduced without prior written permission of the firm

Follow the written dimensions only. Do not scale dimensions from drawings. Any discrepancy in the drawing or dimensions should be brought to the attention of architects prior to execution. This drawing should be read in conjunction with other drawings issued for project.

PROJECT
Project: Proposed House
Jhansi
U.P., India
Client: Mr.Anubhav Sahu

Drawn by
ER.Shaalu Gupta

Checked by
Er. Sankalp Tiwari

Date : 20/05/2025


Drawing Status
 conceptual
 for approval
 not for construction
 for construction
 as built
 other _____


Drawing and scale
GROUND FLOOR

#LayID

Architects
Meerendra Buildcon
ARCHITECTURE PLANNING & INTERIOR DESIGN

Add:- 159/1, Ayodhapuri gwalior road, jhansi (U.P)
Mob:- 9450076030, 8299732040.
E-mail:- meerendra_07@gmail.com

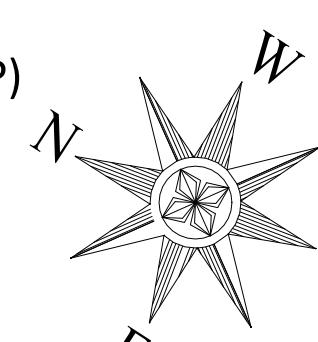

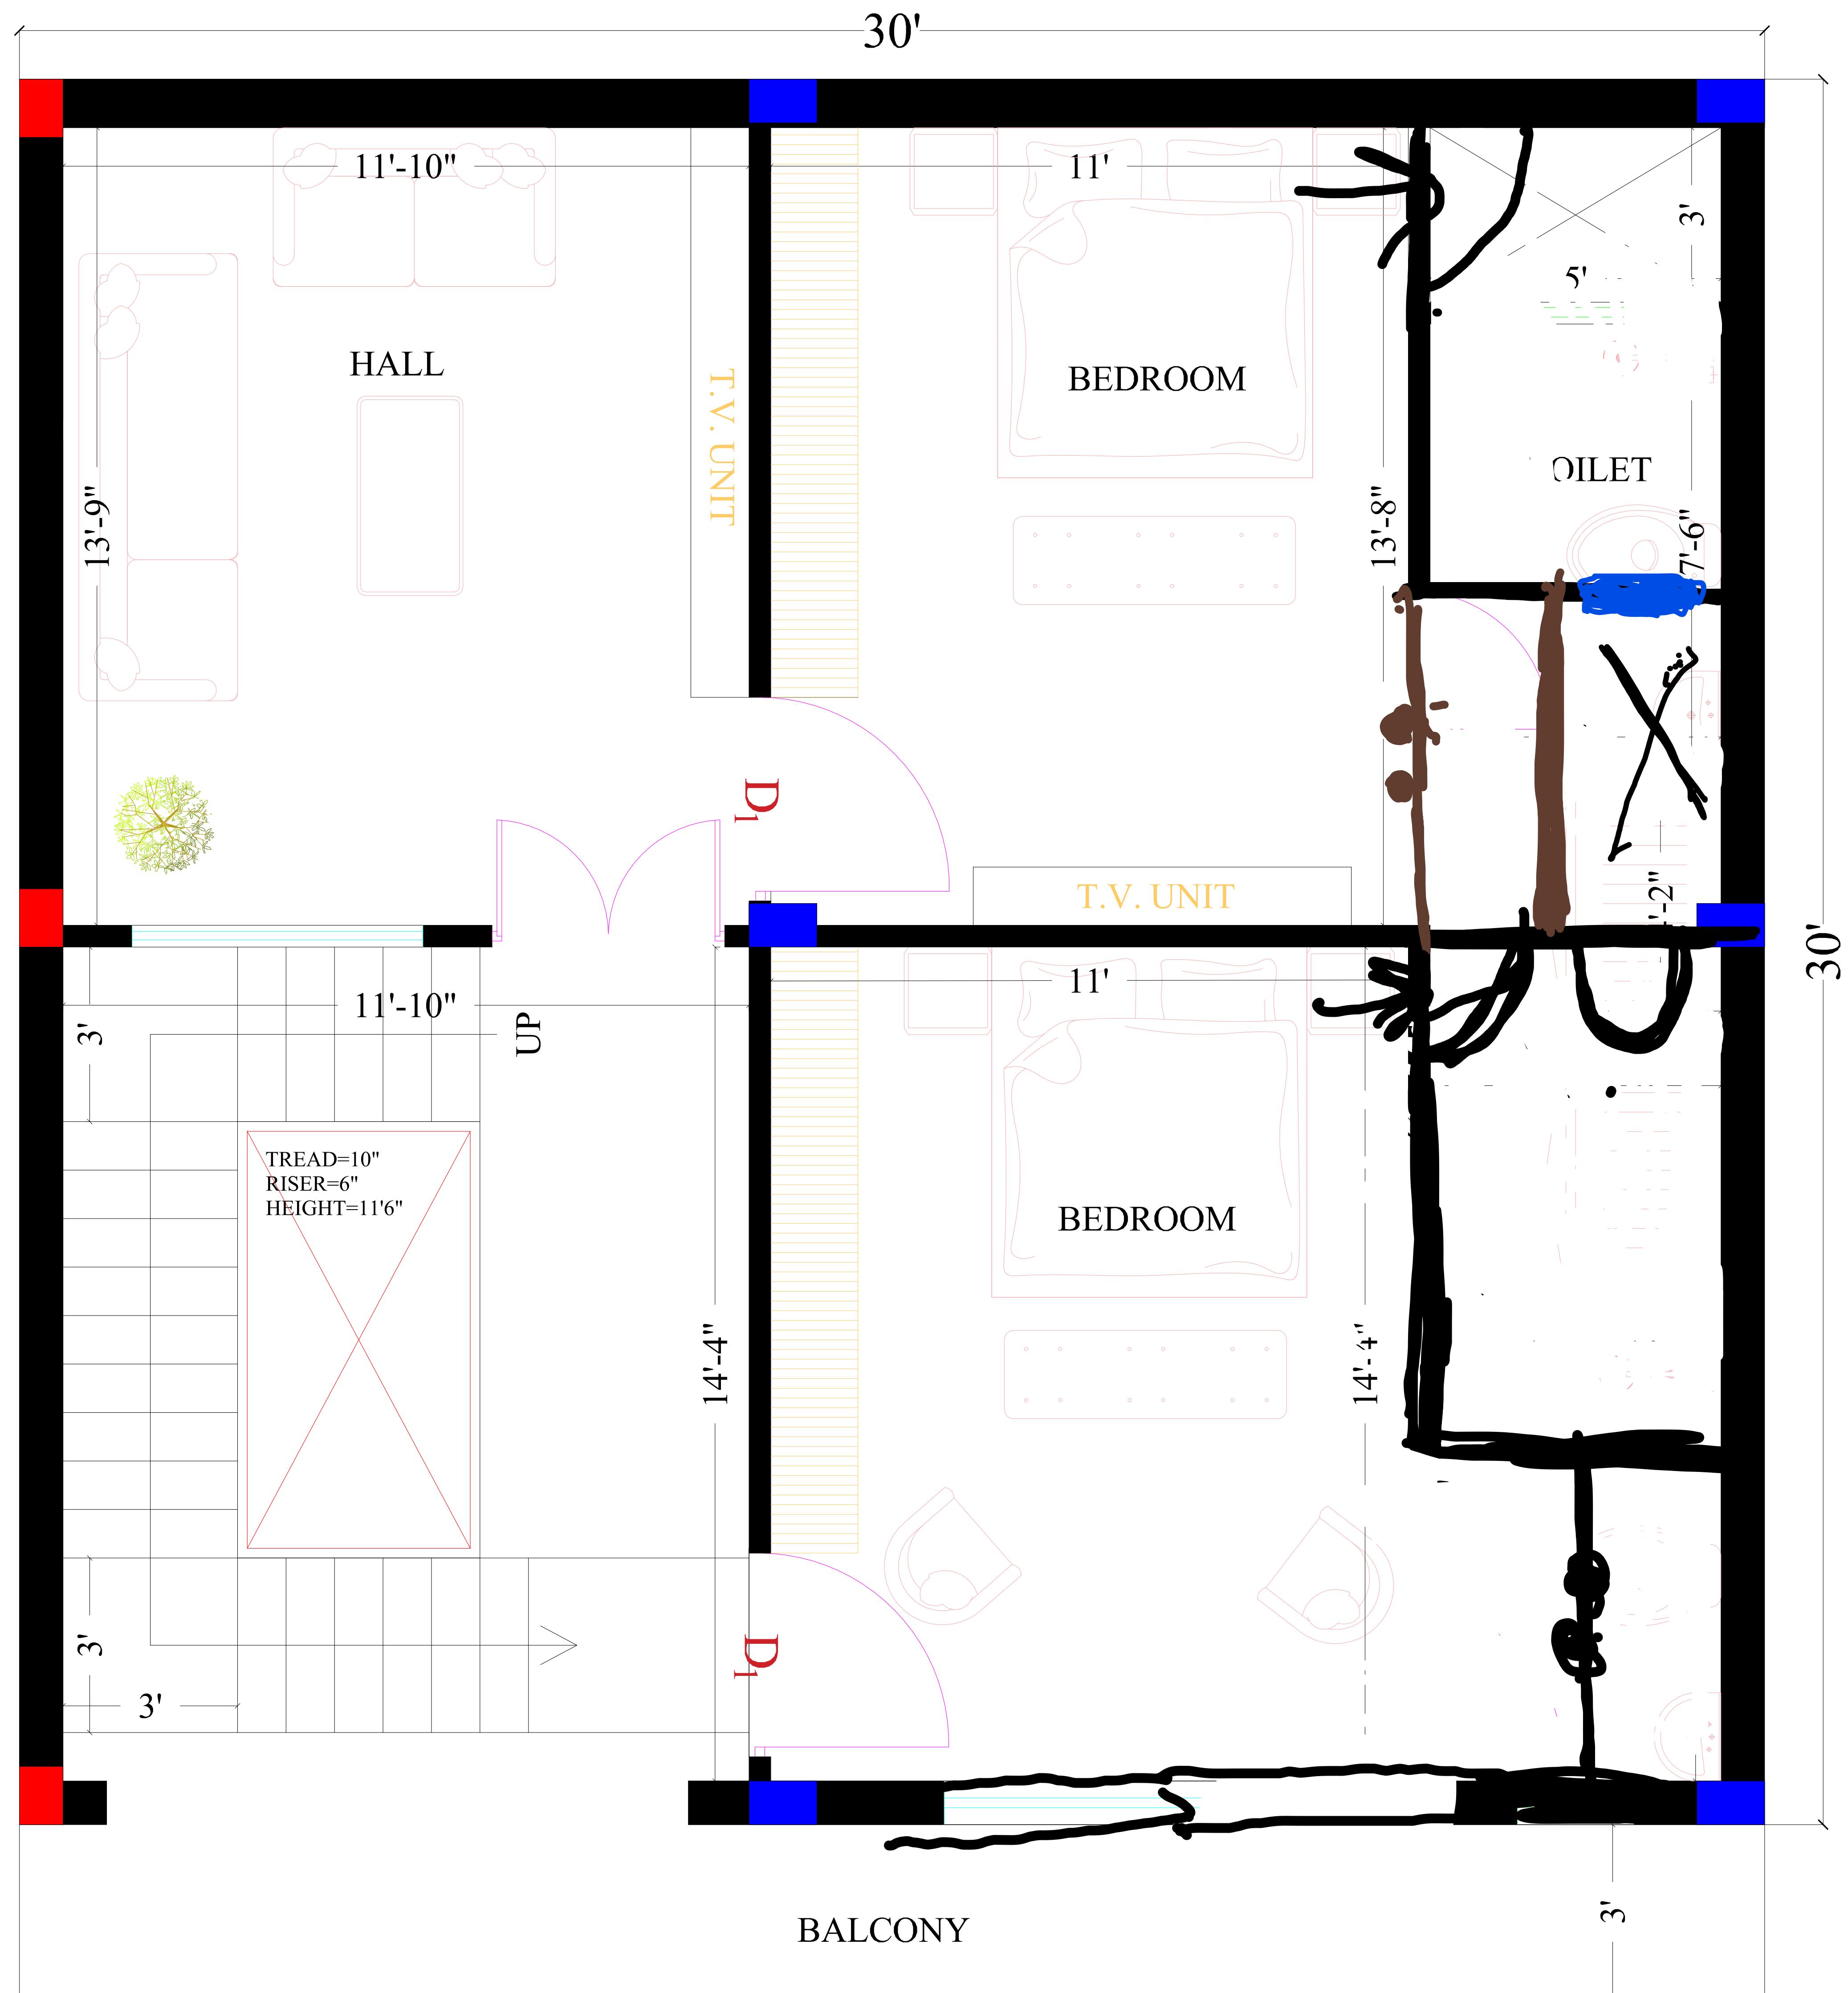

19' WIDE ROAD

This drawing, design & content is property of Architect and shall not be used, copied or reproduced without prior written permission of the firm

Follow the written dimensions only. Do not scale dimensions from drawings. Any discrepancy in the drawing or dimensions should be brought to the attention of architects prior to execution. This drawing should be read in conjunction with other drawings issued for project.

PROJECT
Project: Proposed House
Client: Mr.Anubhav Sahu
Jhansi
U.P., India


Drawn by
ER.Shaalu Gupta
Checked by
Er. Sankalp Tiwari
Date : 20/05/2025


Drawing Status
 conceptual
 for approval
 not for construction
 for construction
 as built
 other _____

Drawing and scale
GROUND FLOOR
#LayID


Architects
Meerendra Buildcon
ARCHITECTURE PLANNING & INTERIOR DESIGN

Add:- 159/1, Ayodhapuri gwalior road, jhansi (U.P)
Mob:- 9450076030, 8299732040.
E-mail:- meerendra_07@gmail.com

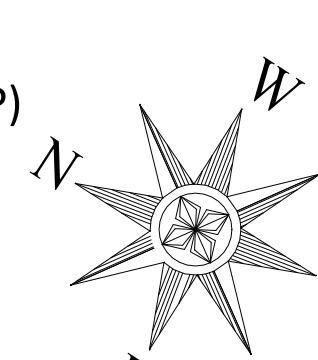


 


COLUMN LAYOUT

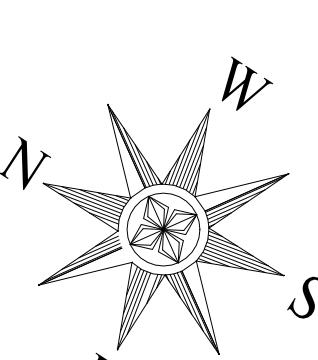PROJECT	Drawn by ER.Shaalu Gupta	Drawing Status	Drawing and scale WORKING	#LayID	Architects
					Meerendra Buildcon ARCHITECTURE PLANNING & INTERIOR DESIGN
					Add:- 159/1, Ayodhapuri gwalior road, jhansi (U.P) Mob:- 9450076030, 8299732040. E-mail:- meerendra_07@gmail.com
					
This drawing, design & content is property of Architect and shall not be used, copied or reproduced without prior written permission of the firm	Project: Proposed House	conceptual			
Follow the written dimensions only. Do not scale dimensions from drawings. Any discrepancy in the drawing or dimensions should be brought to the attention of architects prior to execution. This drawing should be read in conjunction with other drawings issued for project.	Client: Mr.Anubhav Sahu	for approval			
		not for construction			
		for construction			
		as built			
		other _____			


COLUMN DETAIL

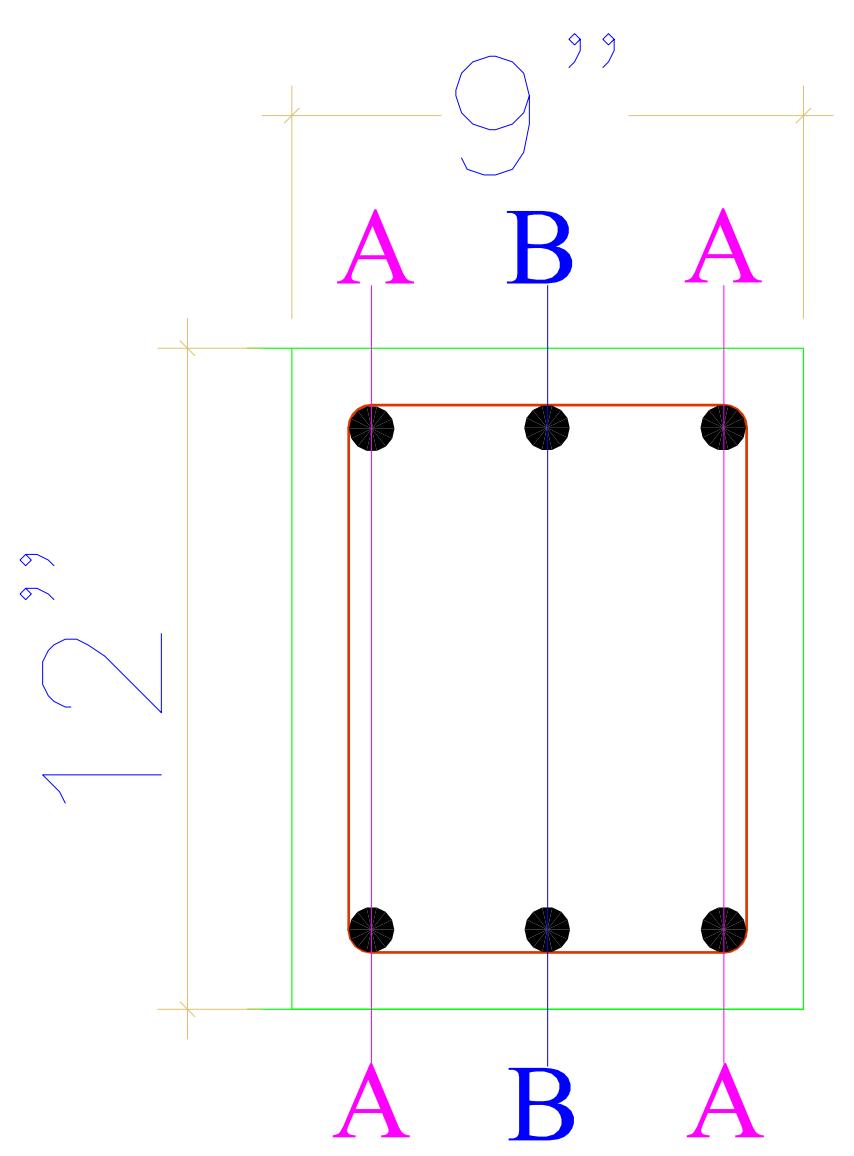

AA-4-16mm \varnothing
BB-2-12mm \varnothing

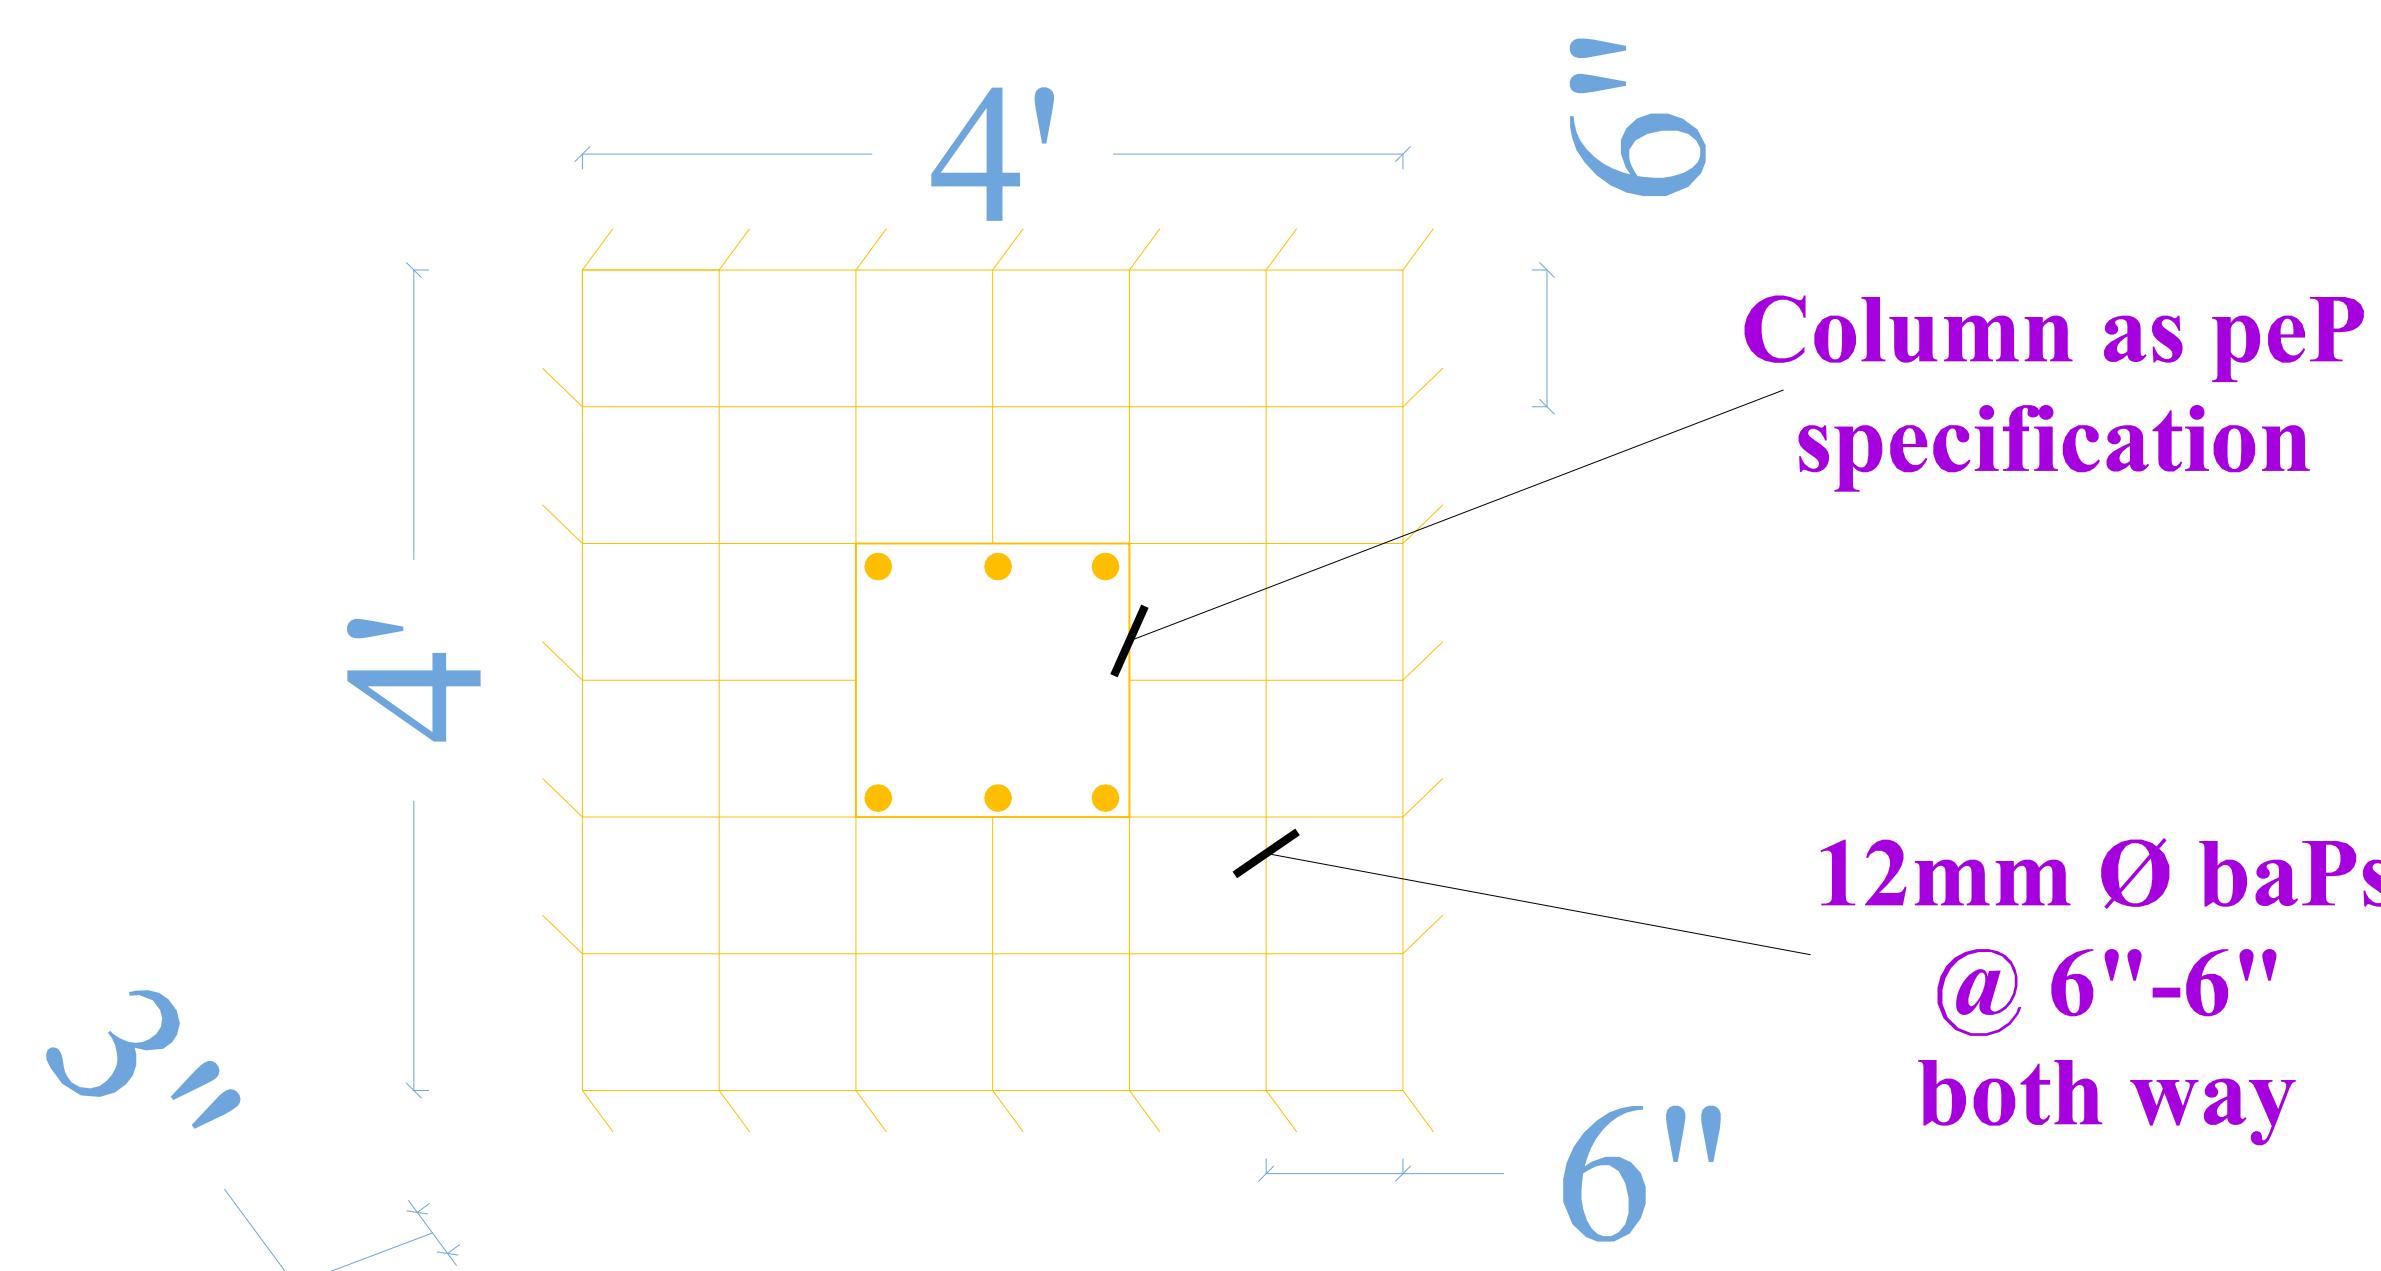


MATTING PLAN

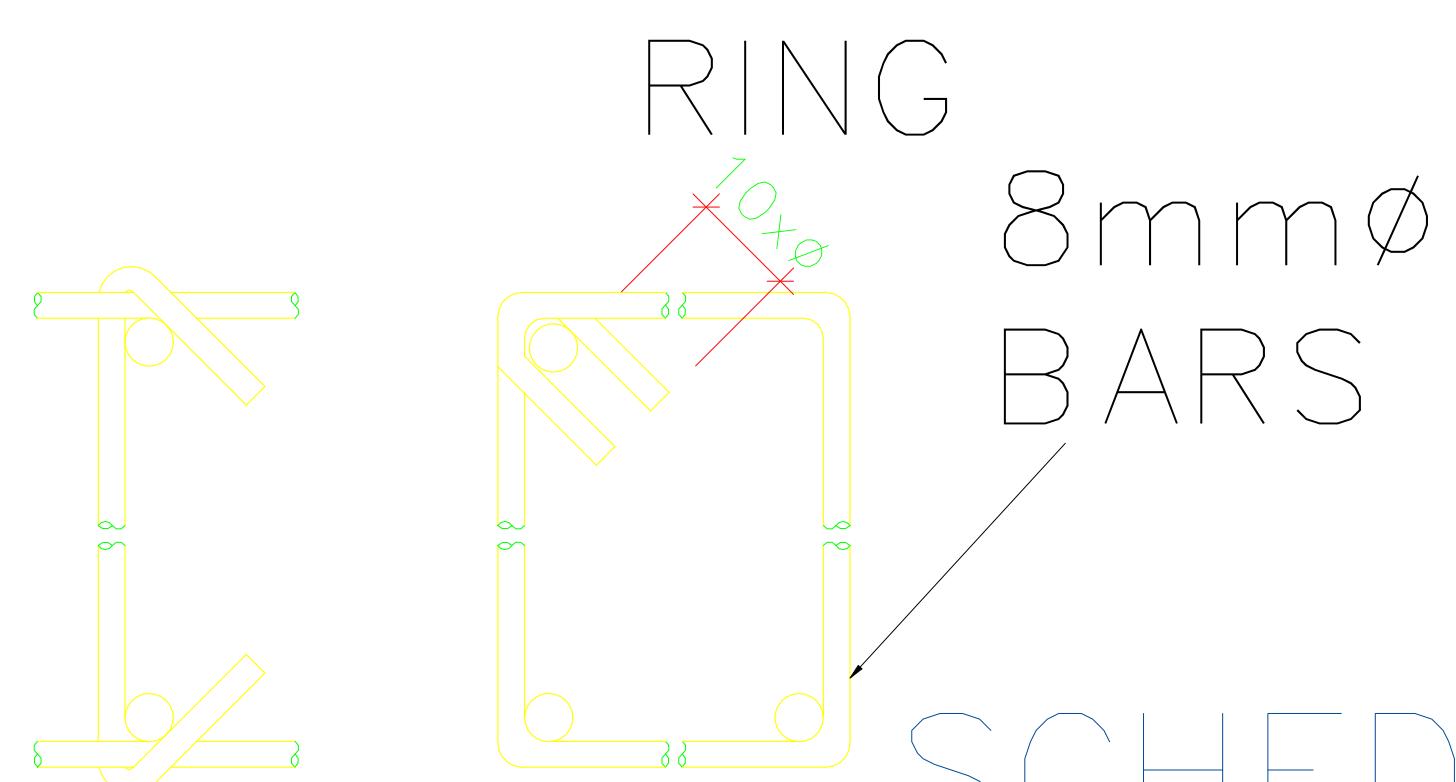


SCHEDULE OF
COLUMN TIES


COLUMN DETAIL

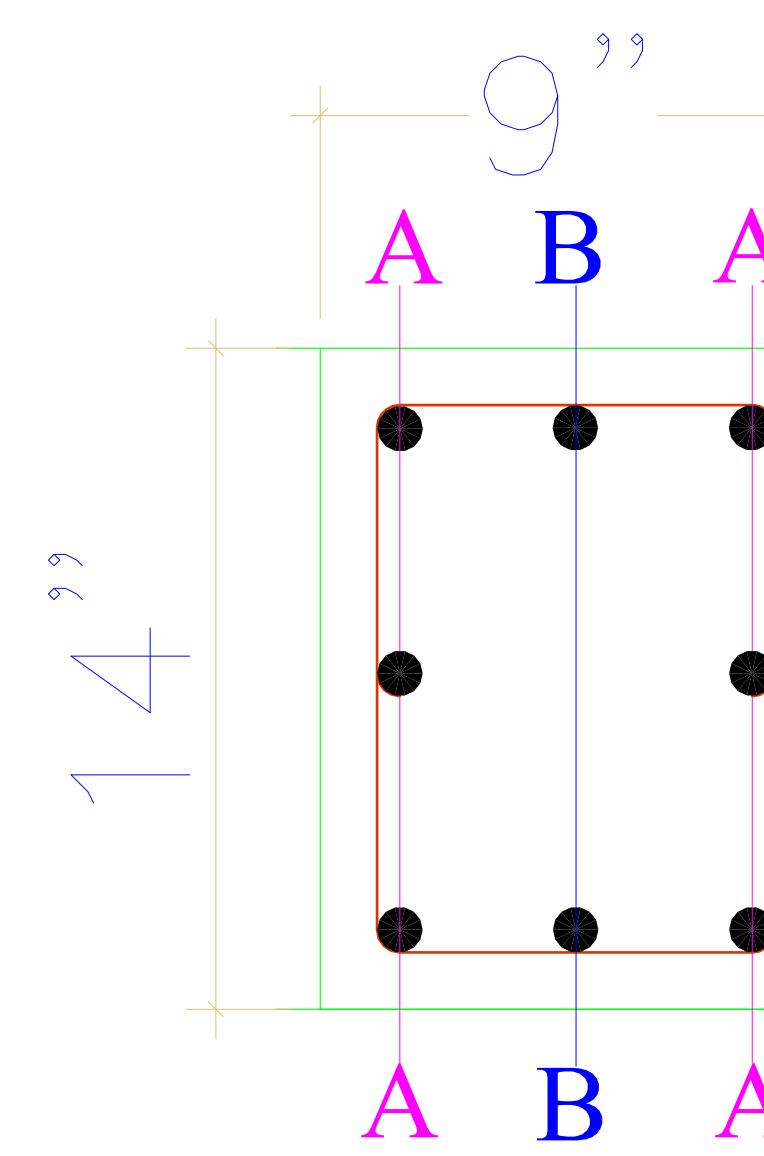


AA-6-16mm \varnothing
BB-2-12mm \varnothing

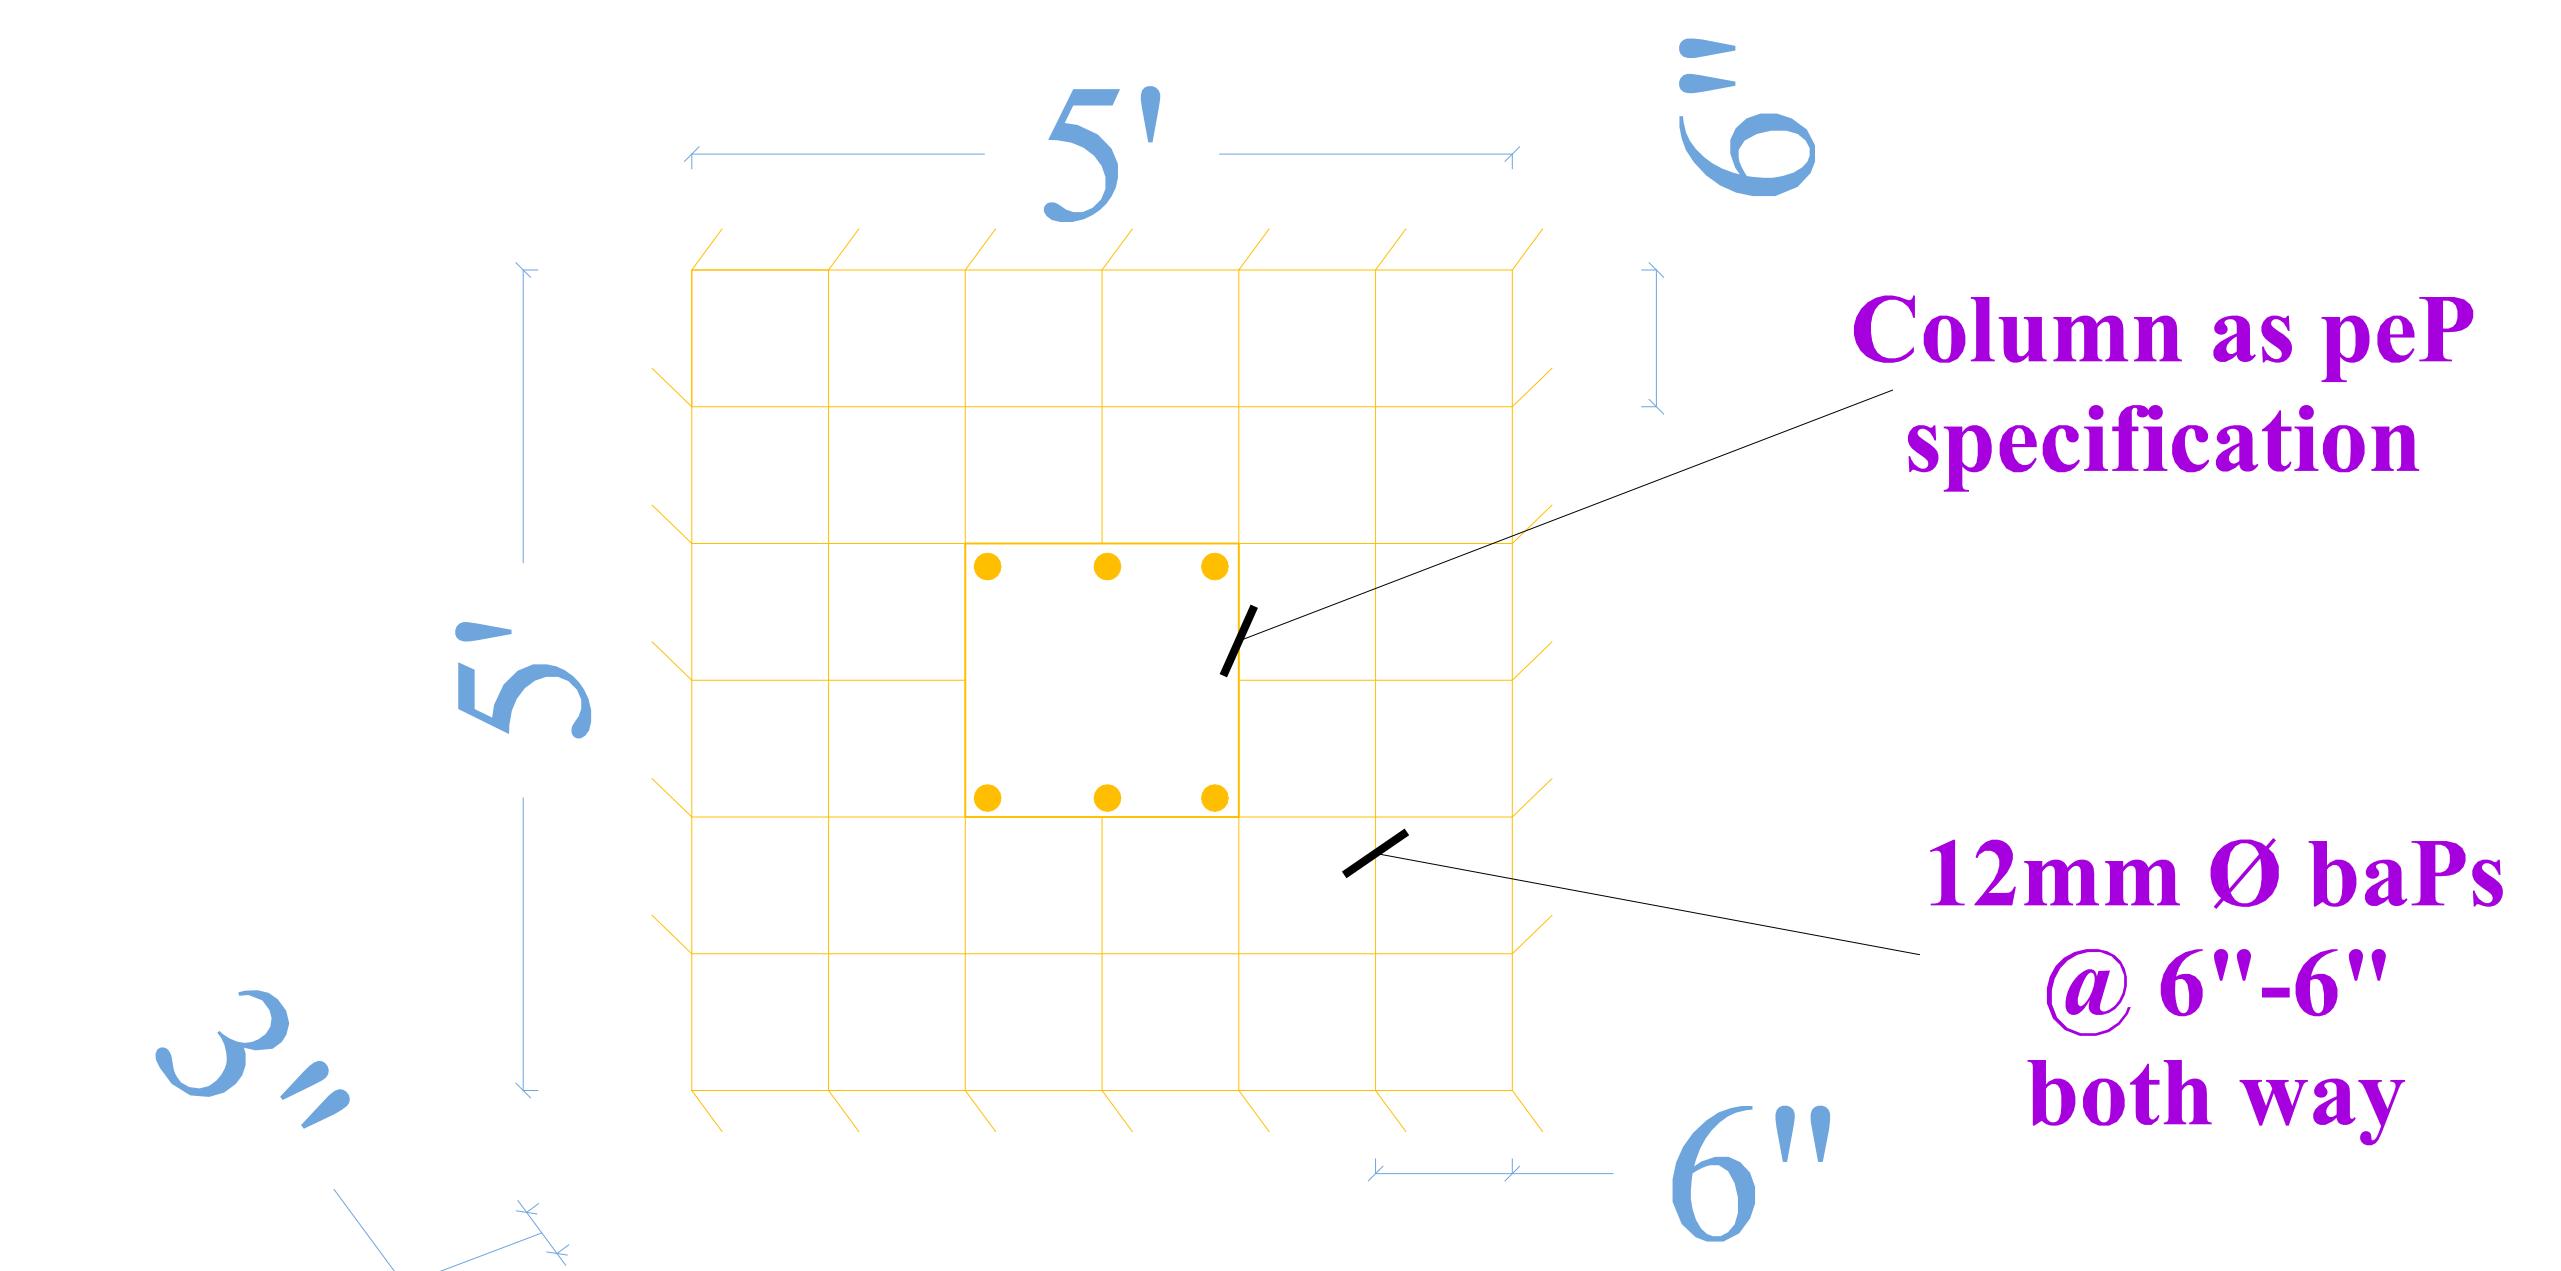

MATTING PLAN

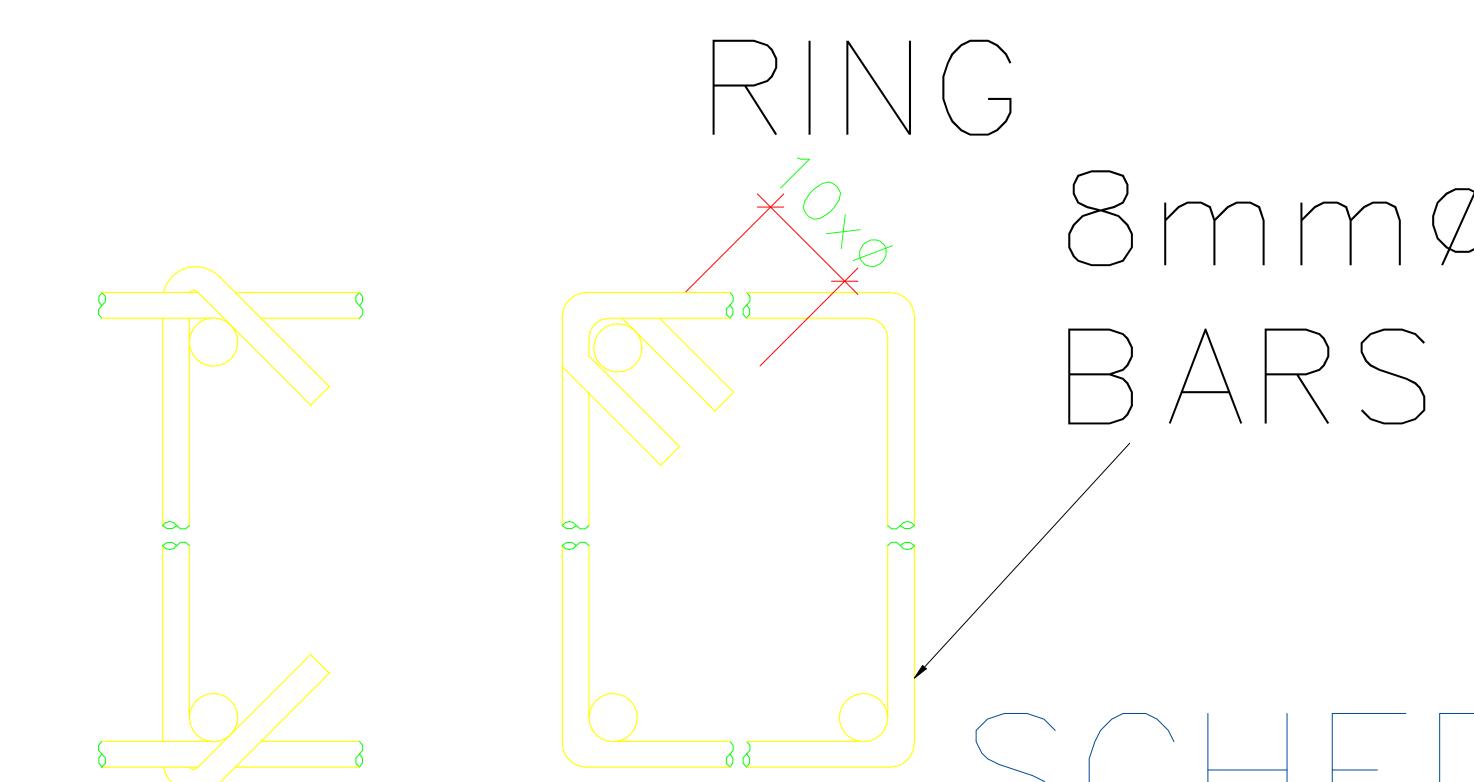


SCHEDULE OF
COLUMN TIES

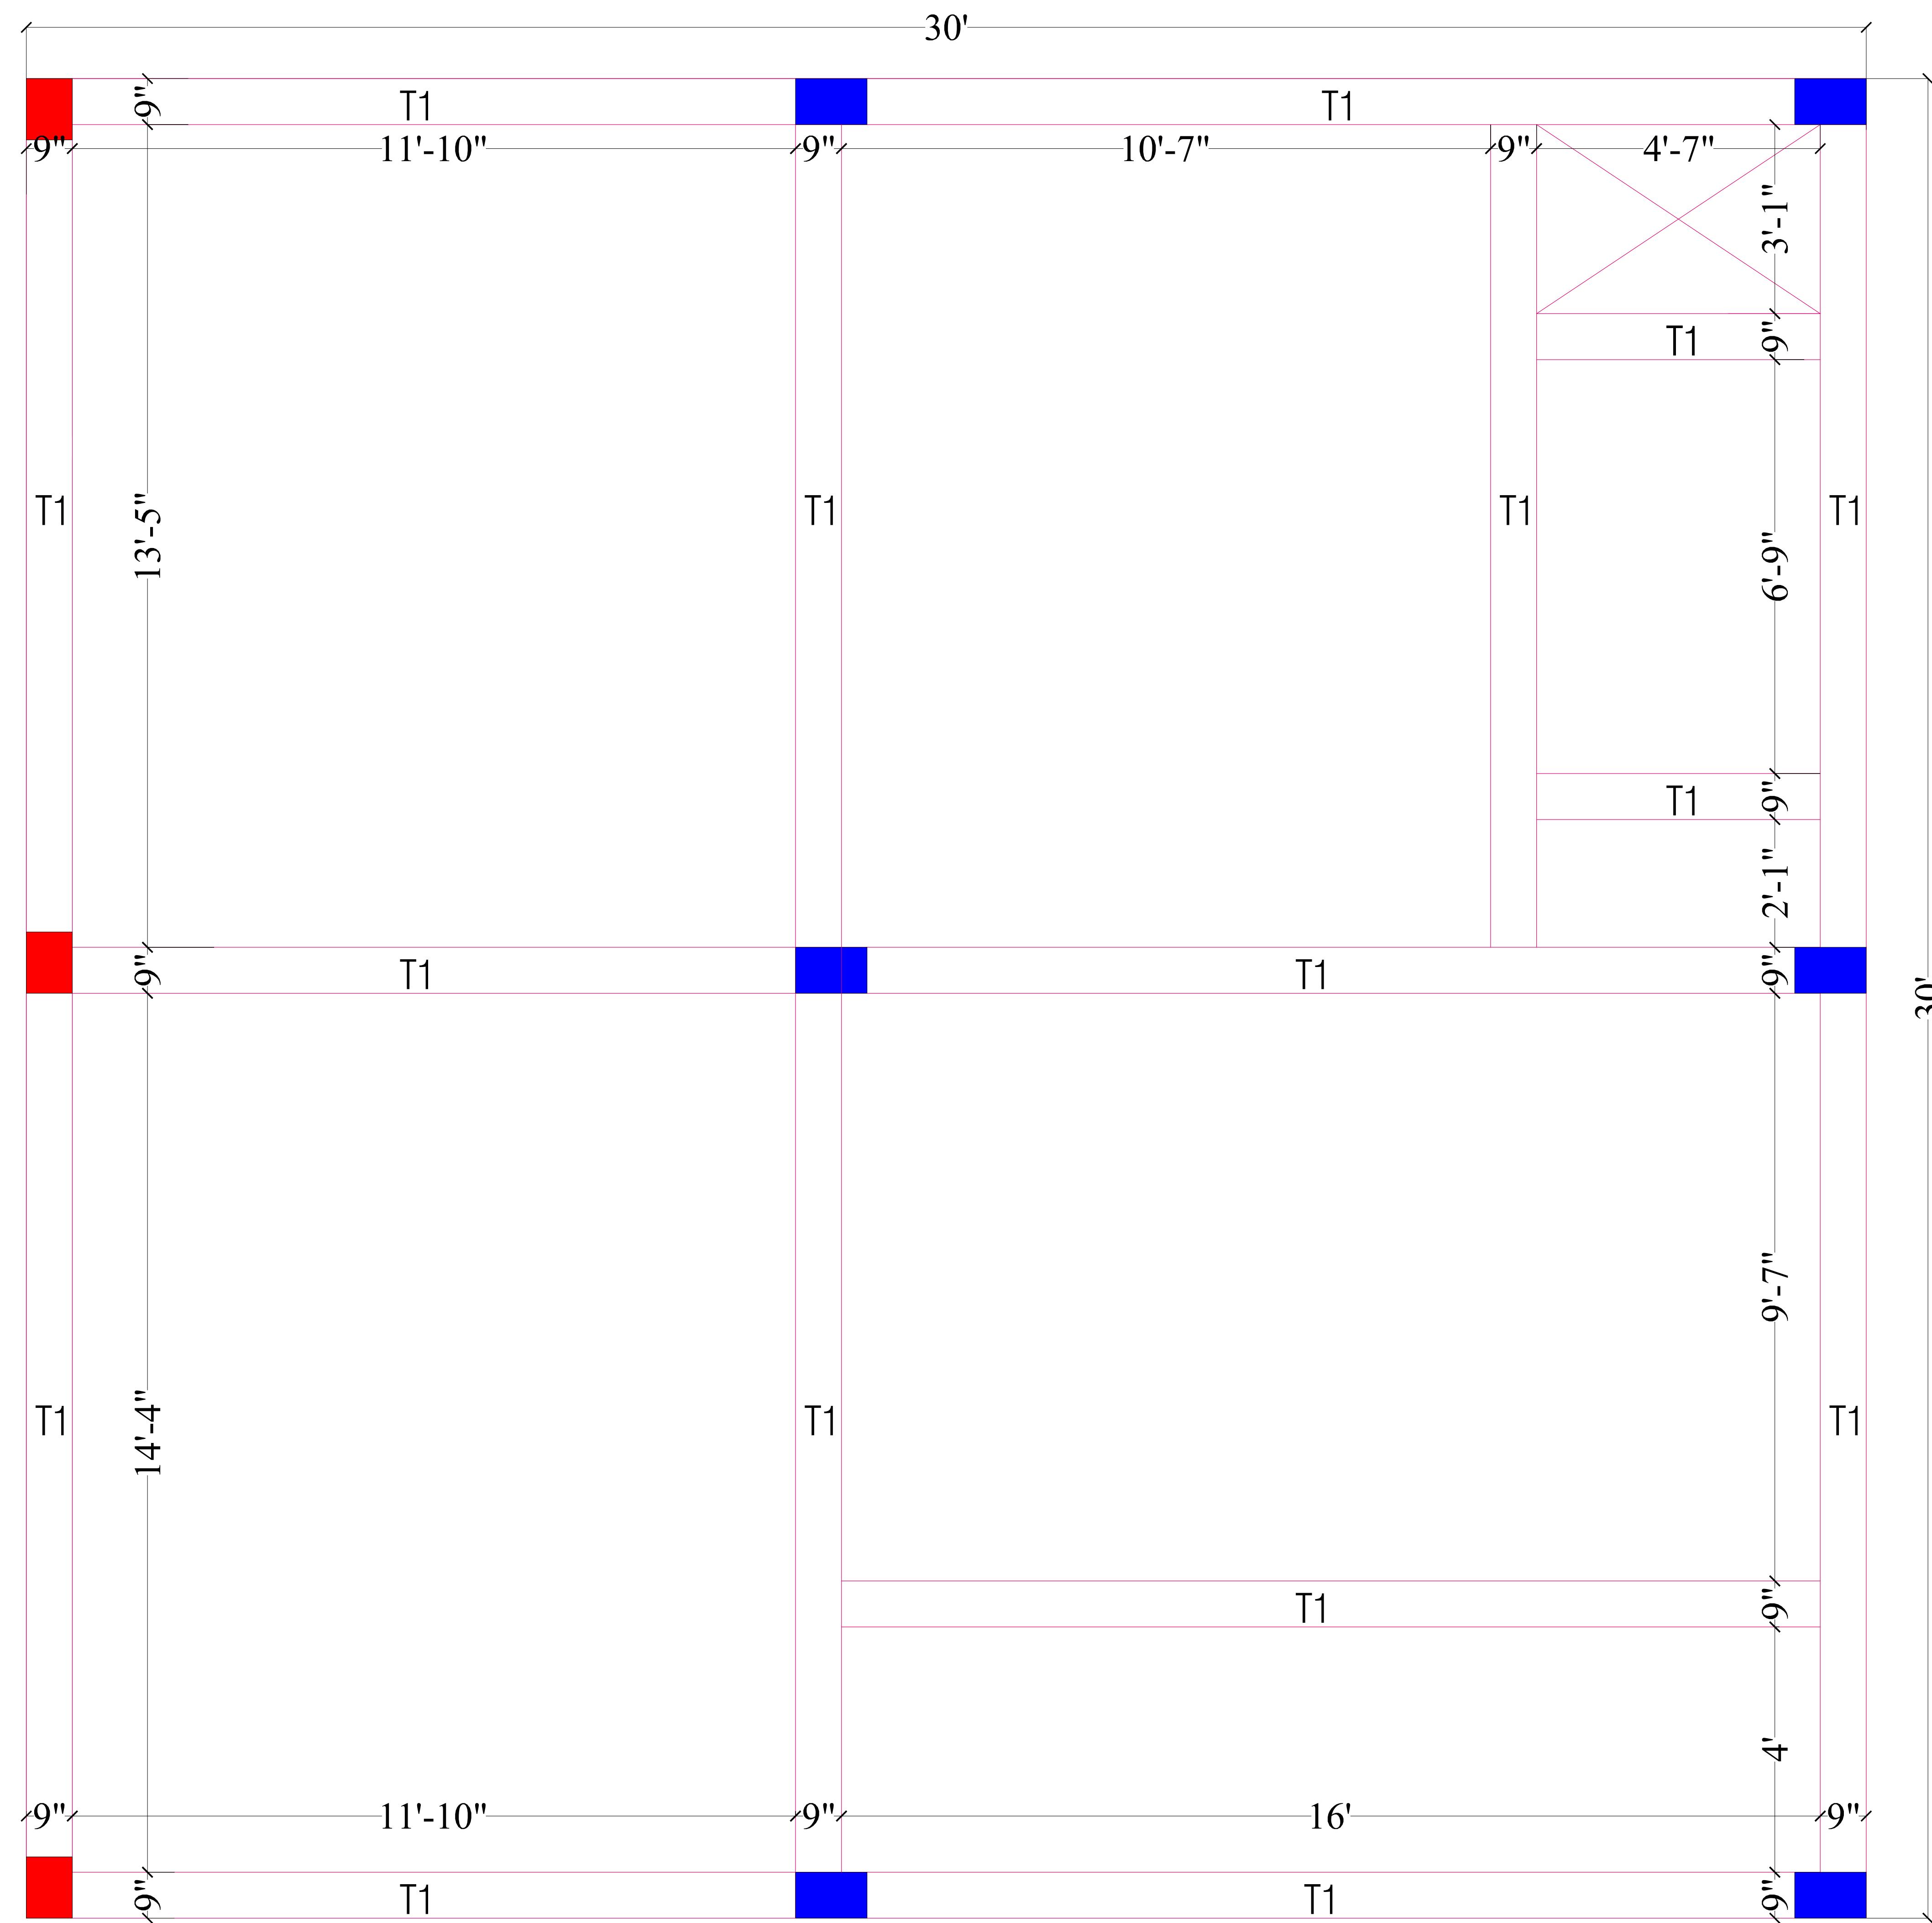

FOR ALL FLOORS

S.NO.	TIEBEAM	BEAM. SIZE	REINFORCEMENT	TIES IN MID	TIES IN END & BOTTOM
1	T1	9"X9"	6 BARS OF 12mm	8mm@7" C/C	8mm@5" C/C

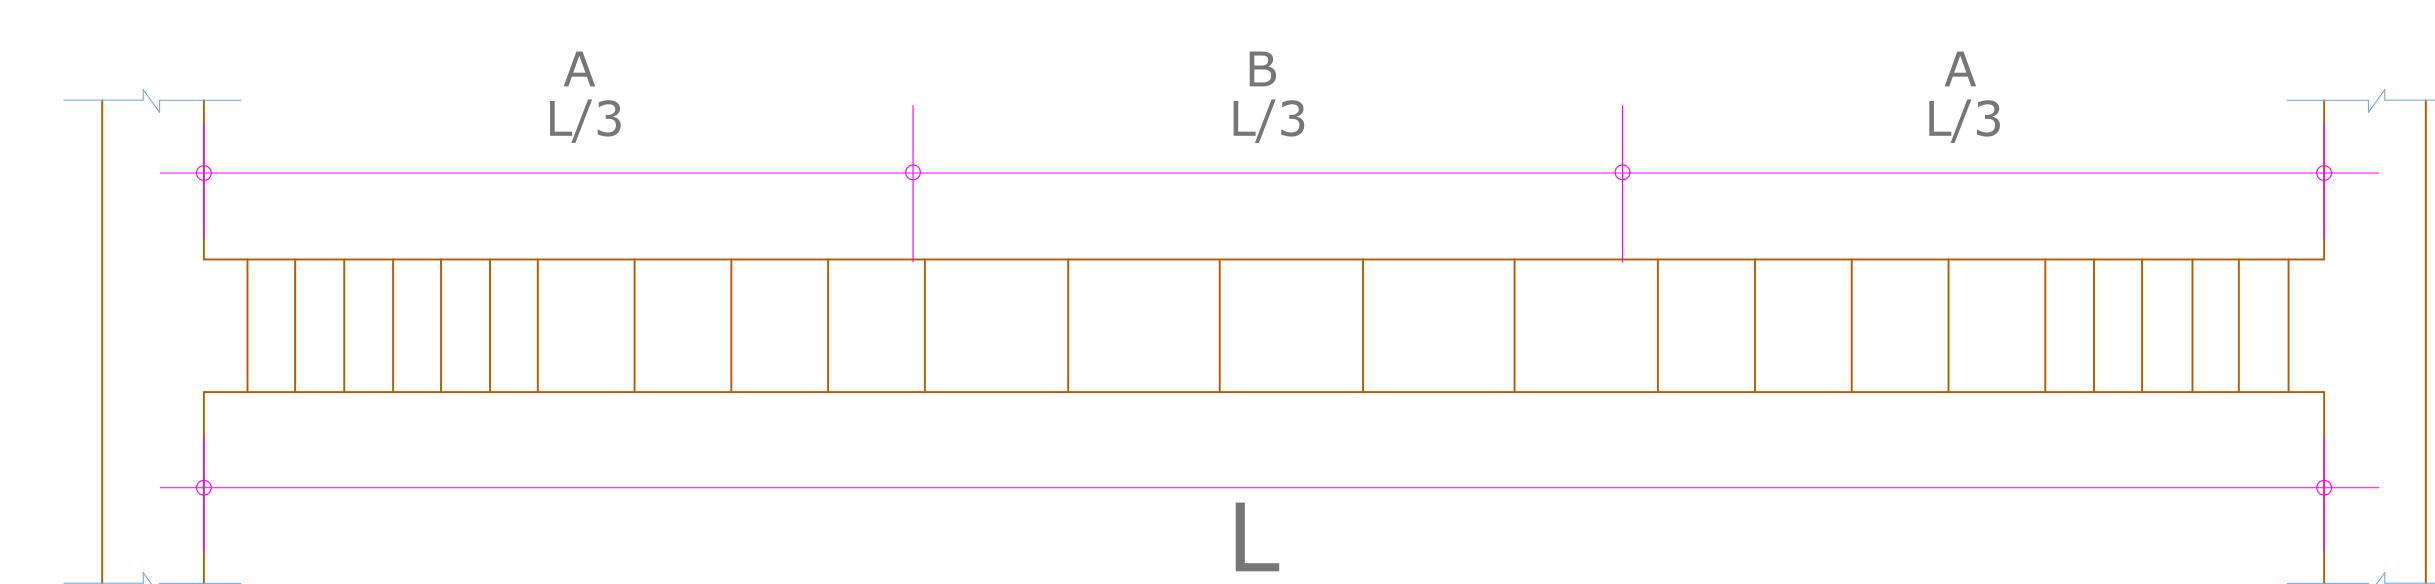

PLINTH BEAM PLAN

This drawing, design & content is property of Architect and shall not be used, copied or reproduced without prior written permission of the firm

Follow the written dimensions only. Do not scale dimensions from drawings. Any discrepancy in the drawing or dimensions should be brought to the attention of architects prior to execution. This drawing should be read in conjunction with other drawings issued for project.

Project: Proposed House
Jhansi
U.P., India
Client: Mr. Anubhav Sahu

Drawn by
ER.Shaalu Gupta

Checked by
Er. Sankalp Tiwari

Date : 20/05/2025


Drawing Status
 conceptual
 for approval
 not for construction
 for construction
 as built
 other _____


Drawing and scale
WORKING

#LayID

Architects
Meerendra Buildcon
ARCHITECTURE PLANNING & INTERIOR DESIGN


Add:- 159/1, Ayodhapuri gwalior road, jhansi (U.P)
Mob:- 9450076030, 8299732040.
E-mail:- meerendra_07@gmail.com

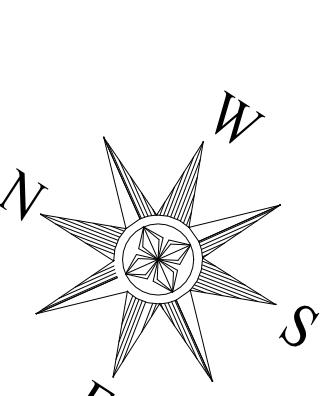

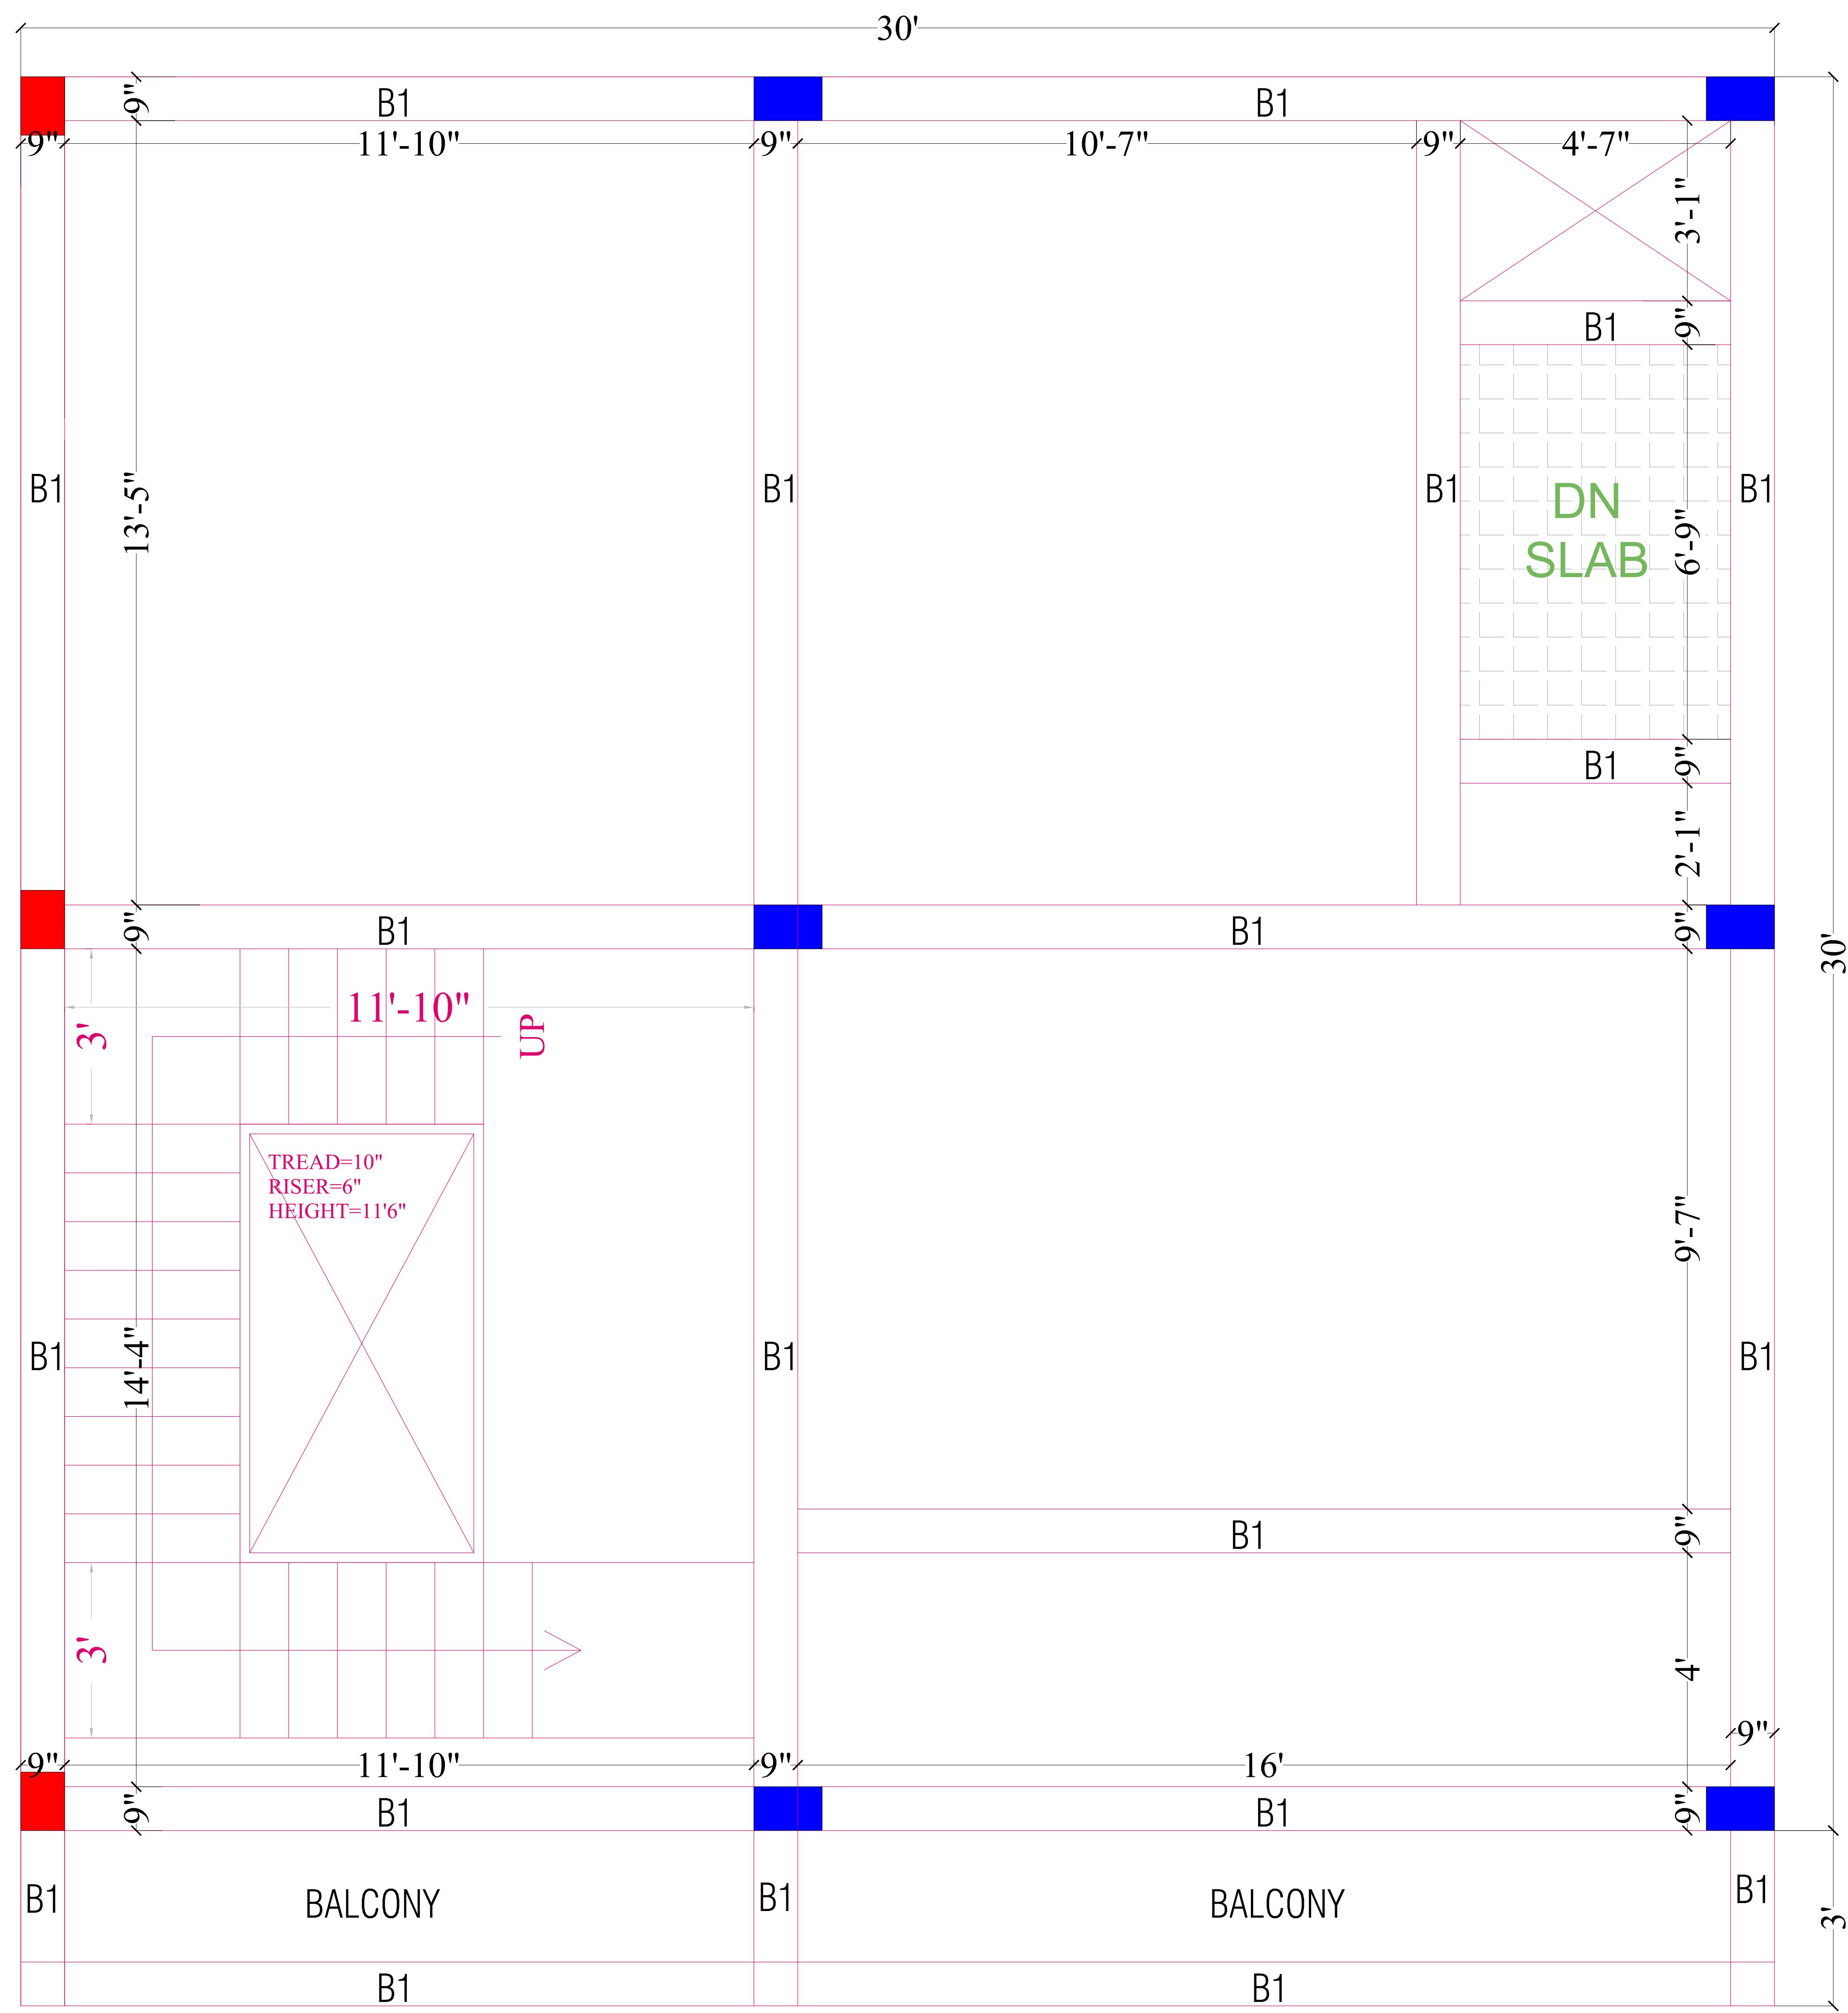

FOR ALL FLOORS

S.NO.	TIEBEAM	BEAM. SIZE	REINFORCEMENT	TIES IN MID	TIES IN END & BOTTOM
1	B1	9"X12"	4 BARS OF 16mm 2 BARS OF 12mm	8mm@7" C/C	8mm@5" C/C

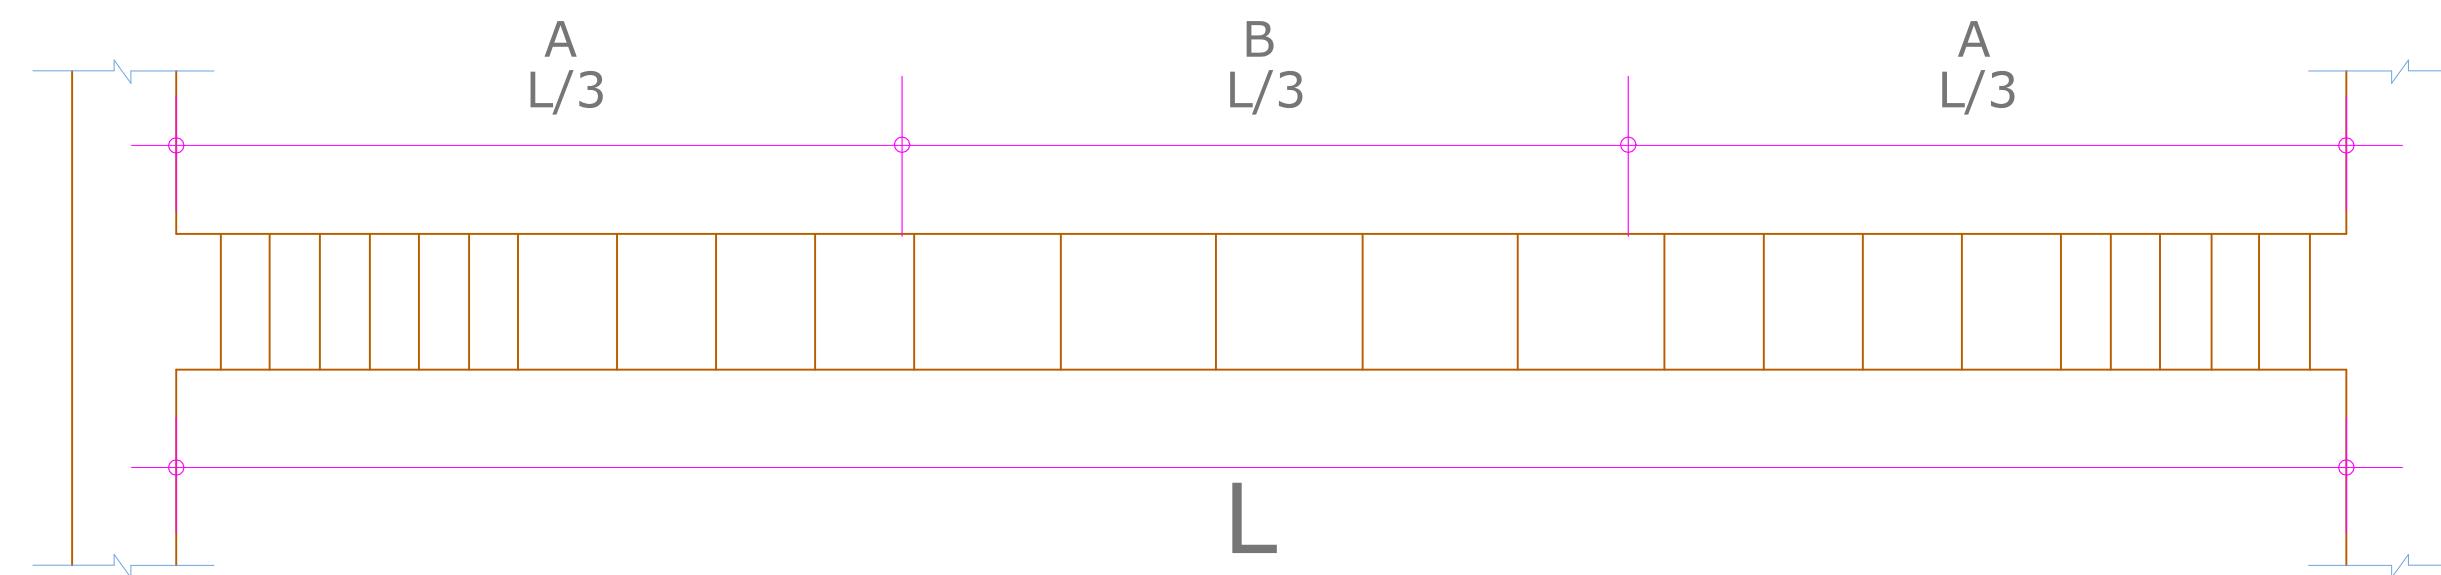

GROUND FLOOR ROOF BEAM PLAN

This drawing, design & content is property of Architect and shall not be used, copied or reproduced without prior written permission of the firm

Follow the written dimensions only. Do not scale dimensions from drawings. Any discrepancy in the drawing or dimensions should be brought to the attention of architects prior to execution. This drawing should be read in conjunction with other drawings issued for project.

PROJECT
Project: Proposed House
Jhansi
U.P., India
Client: Mr.Anubhav Sahu

Drawn by
ER.Shaalu Gupta

Checked by
Er. Sankalp Tiwari

Date : 20/05/2025


Drawing Status
 conceptual
 for approval
 not for construction
 for construction
 as built
 other _____


Drawing and scale
WORKING

#LayID

Architects
Meerendra Buildcon
ARCHITECTURE PLANNING & INTERIOR DESIGN


Add:- 159/1, Ayodhapuri gwalior road, jhansi (U.P)
Mob:- 9450076030, 8299732040.
E-mail:- meerendra_07@gmail.com

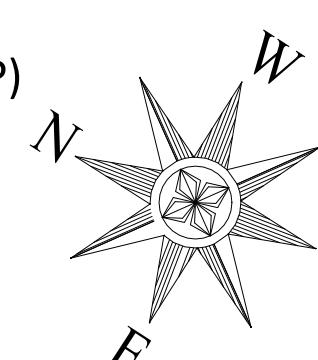

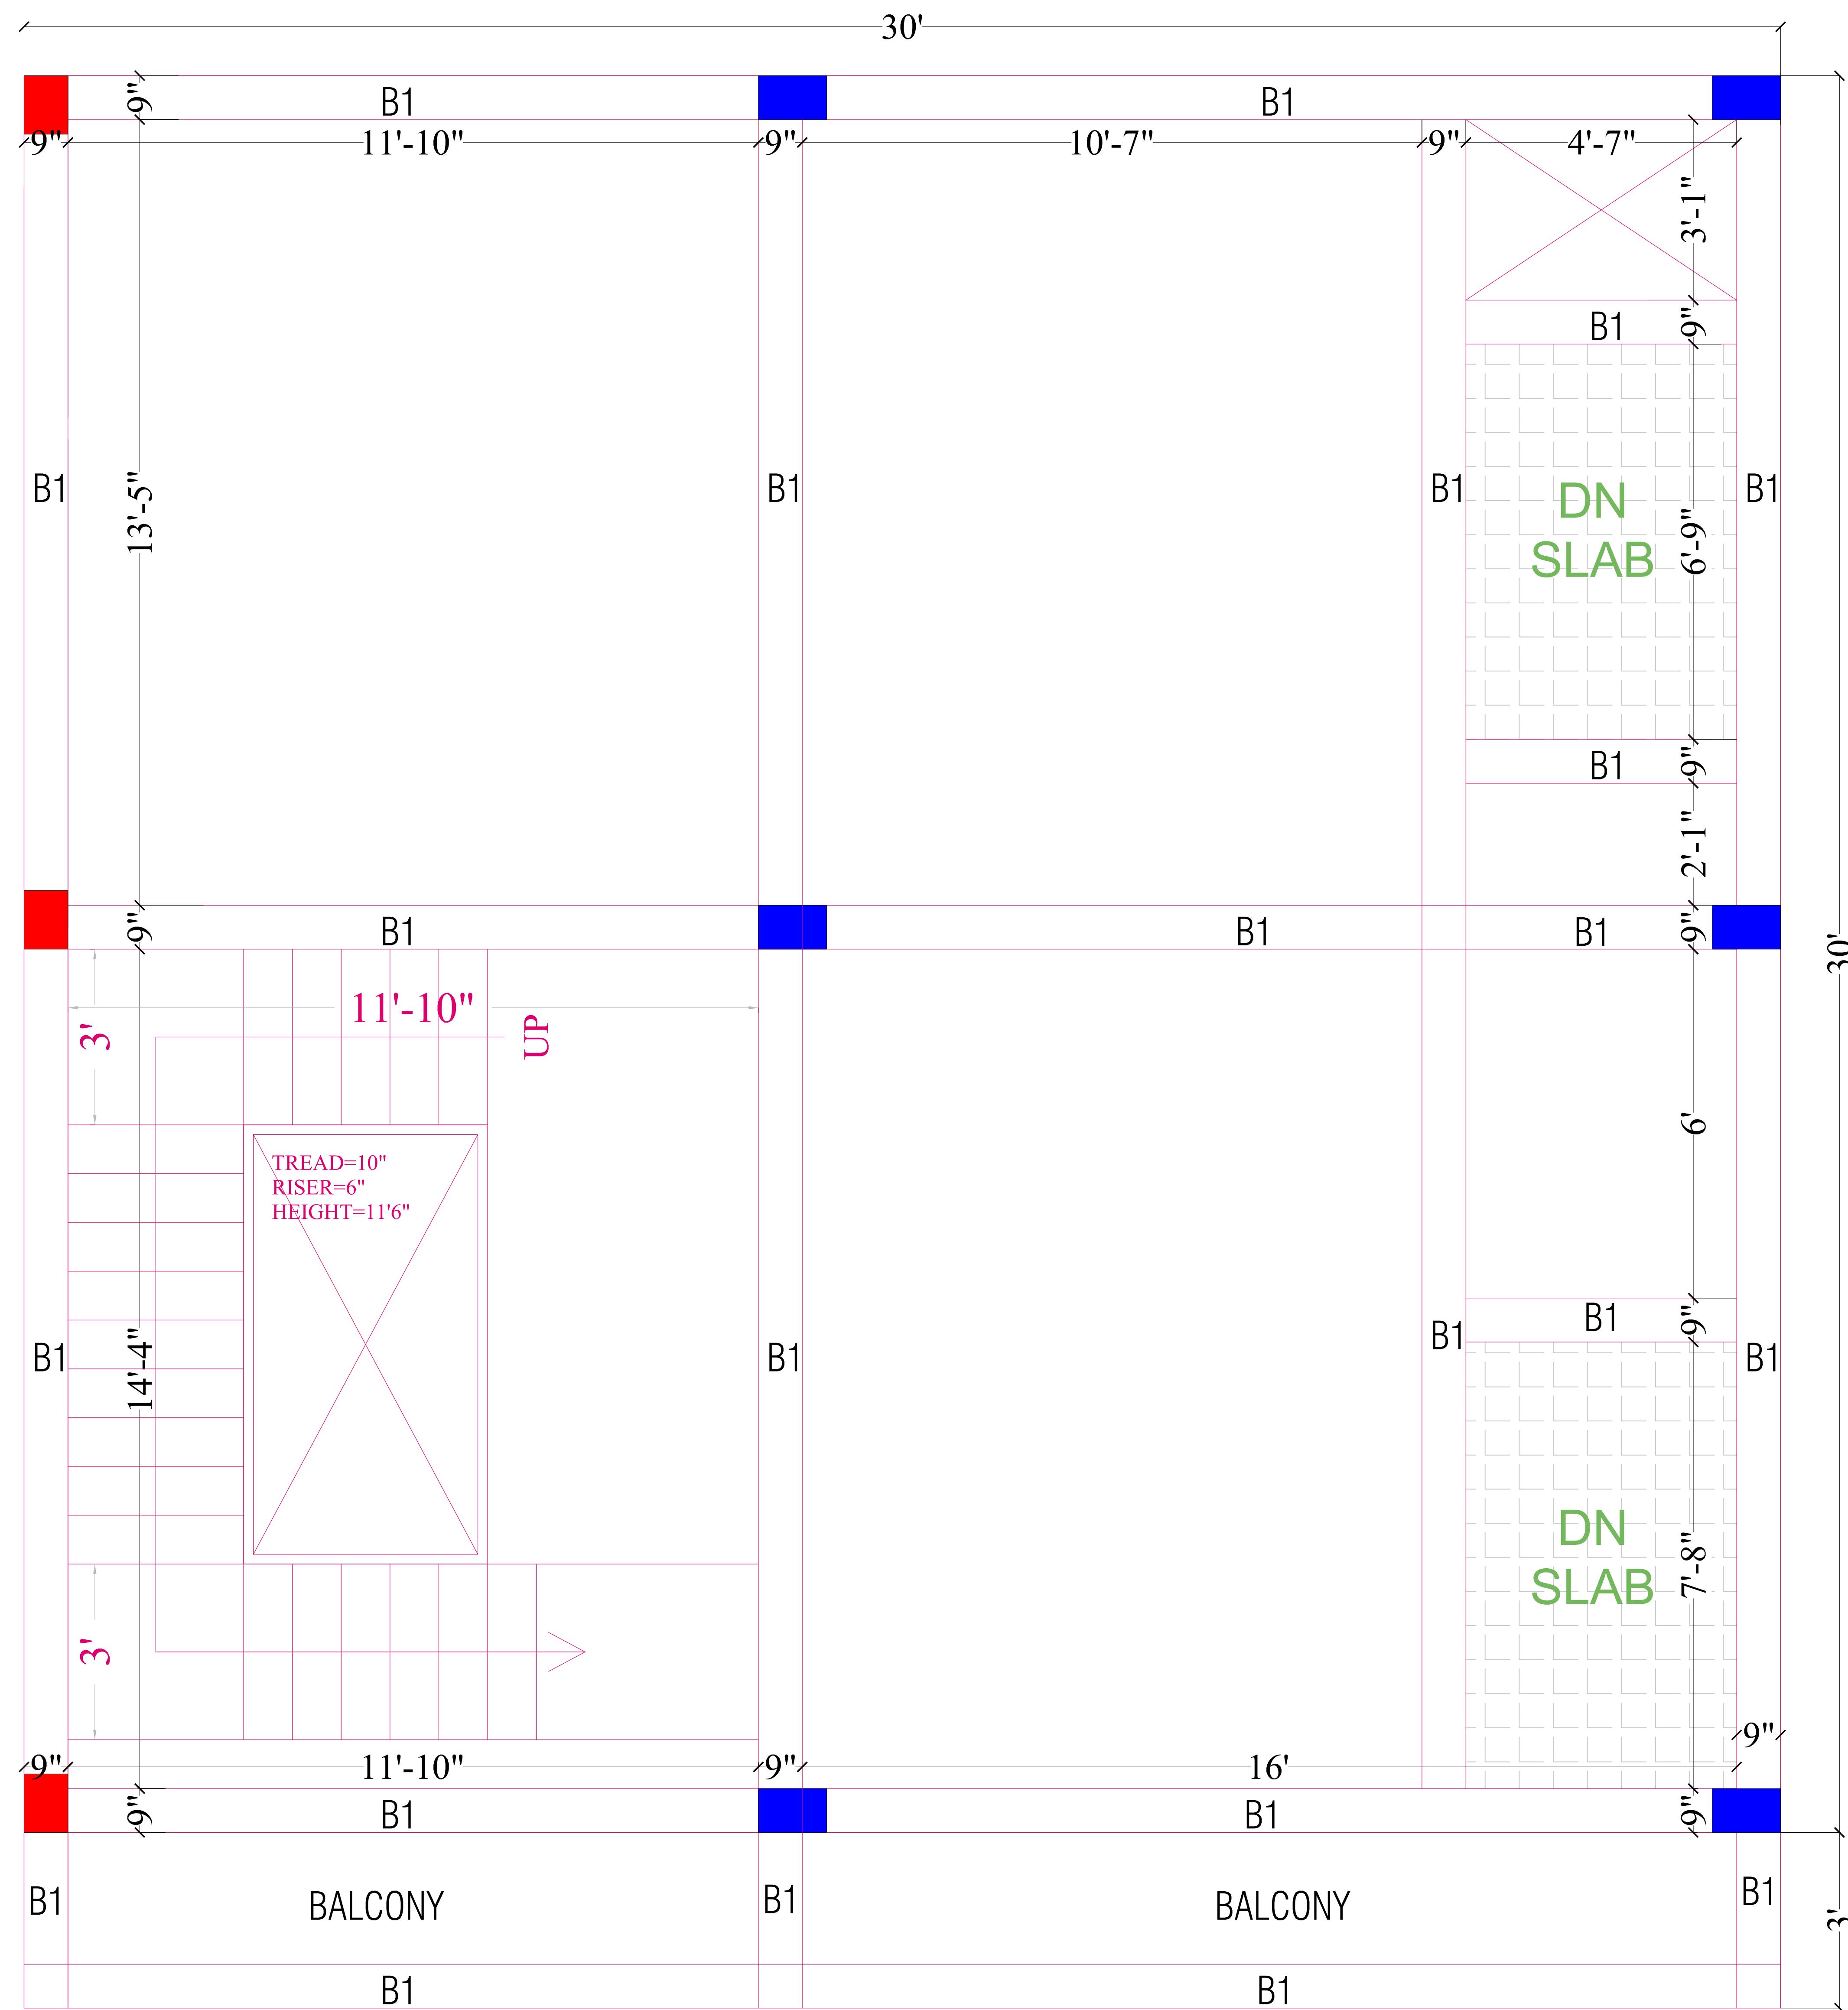

FOR ALL FLOORS

S.NO.	TIEBEAM	BEAM. SIZE	REINFORCEMENT	TIES IN MID	TIES IN END & BOTTOM
1	B1	9"X12"	4 BARS OF 16mm 2 BARS OF 12mm	8mm@7" C/C	8mm@5" C/C

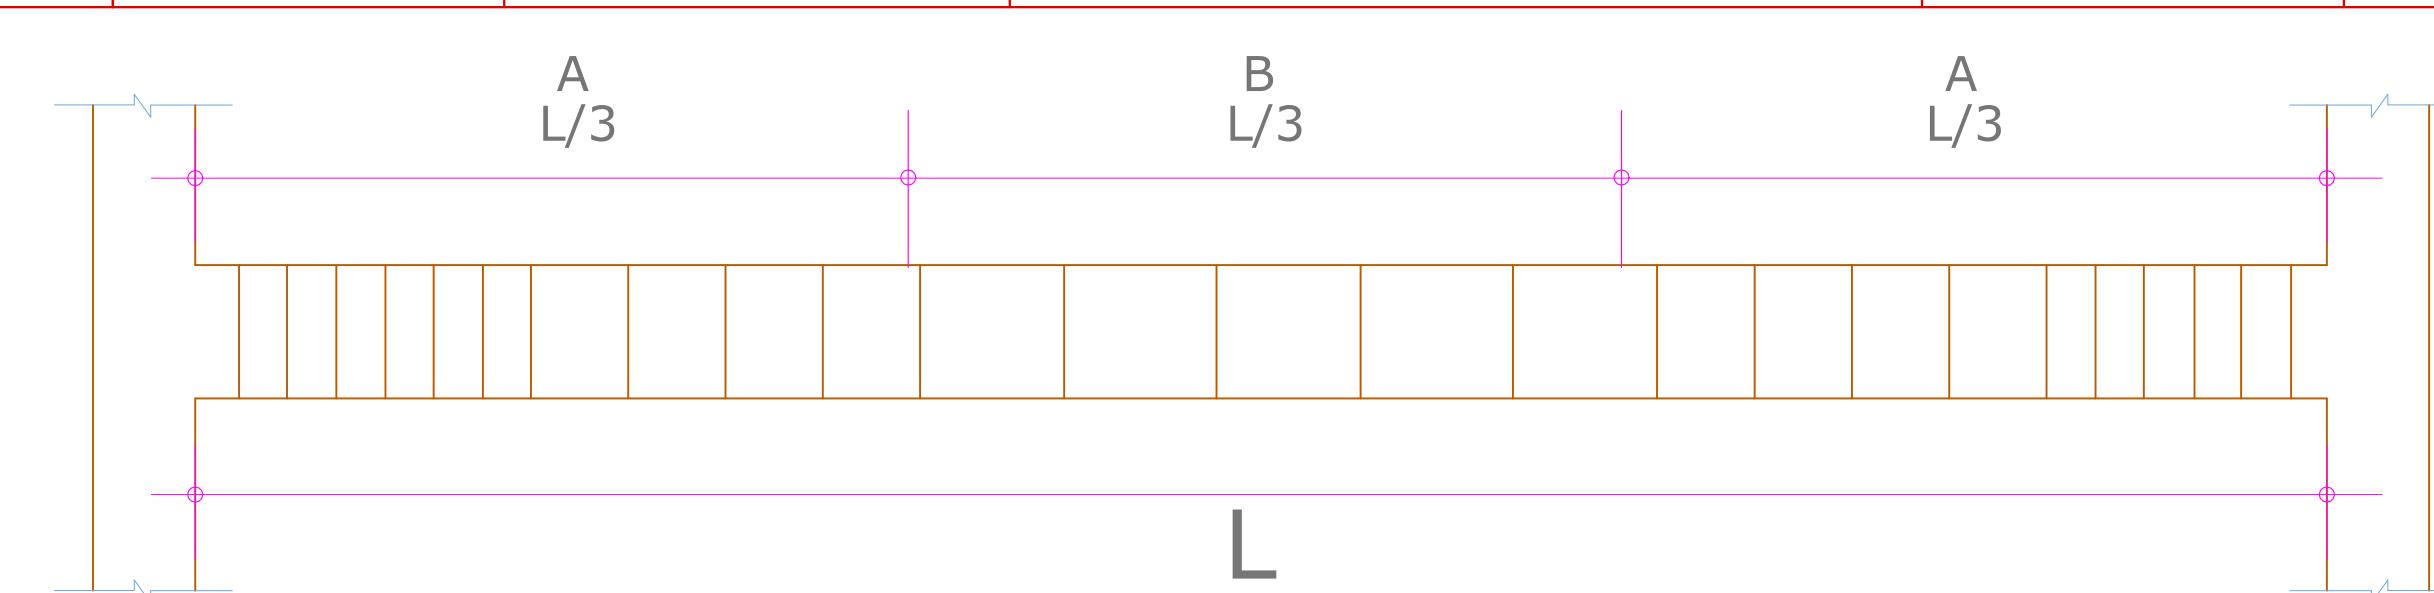

FIRST FLOOR ROOF BEAM PLAN

This drawing, design & content is property of Architect and shall not be used, copied or reproduced without prior written permission of the firm

Follow the written dimensions only. Do not scale dimensions from drawings. Any discrepancy in the drawing or dimensions should be brought to the attention of architects prior to execution. This drawing should be read in conjunction with other drawings issued for project.

PROJECT
Project: Proposed House
Jhansi
U.P., India
Client: Mr. Anubhav Sahu

Drawn by
ER.Shaalu Gupta

Checked by
Er. Sankalp Tiwari

Date : 20/05/2025

Drawing Status
 conceptual
 for approval
 not for construction
 for construction
 as built
 other _____


Drawing and scale
WORKING


#LayID

Architects

Meerendra Buildcon
ARCHITECTURE PLANNING & INTERIOR DESIGN

Add:- 159/1, Ayodhapuri gwalior road, jhansi (U.P)
Mob:- 9450076030, 8299732040.
E-mail:- meerendra_07@gmail.com

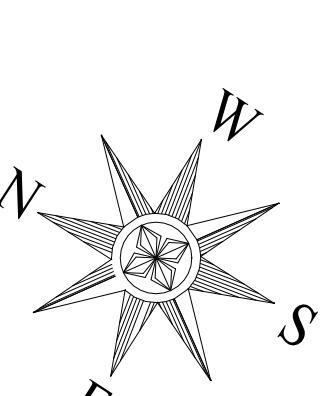

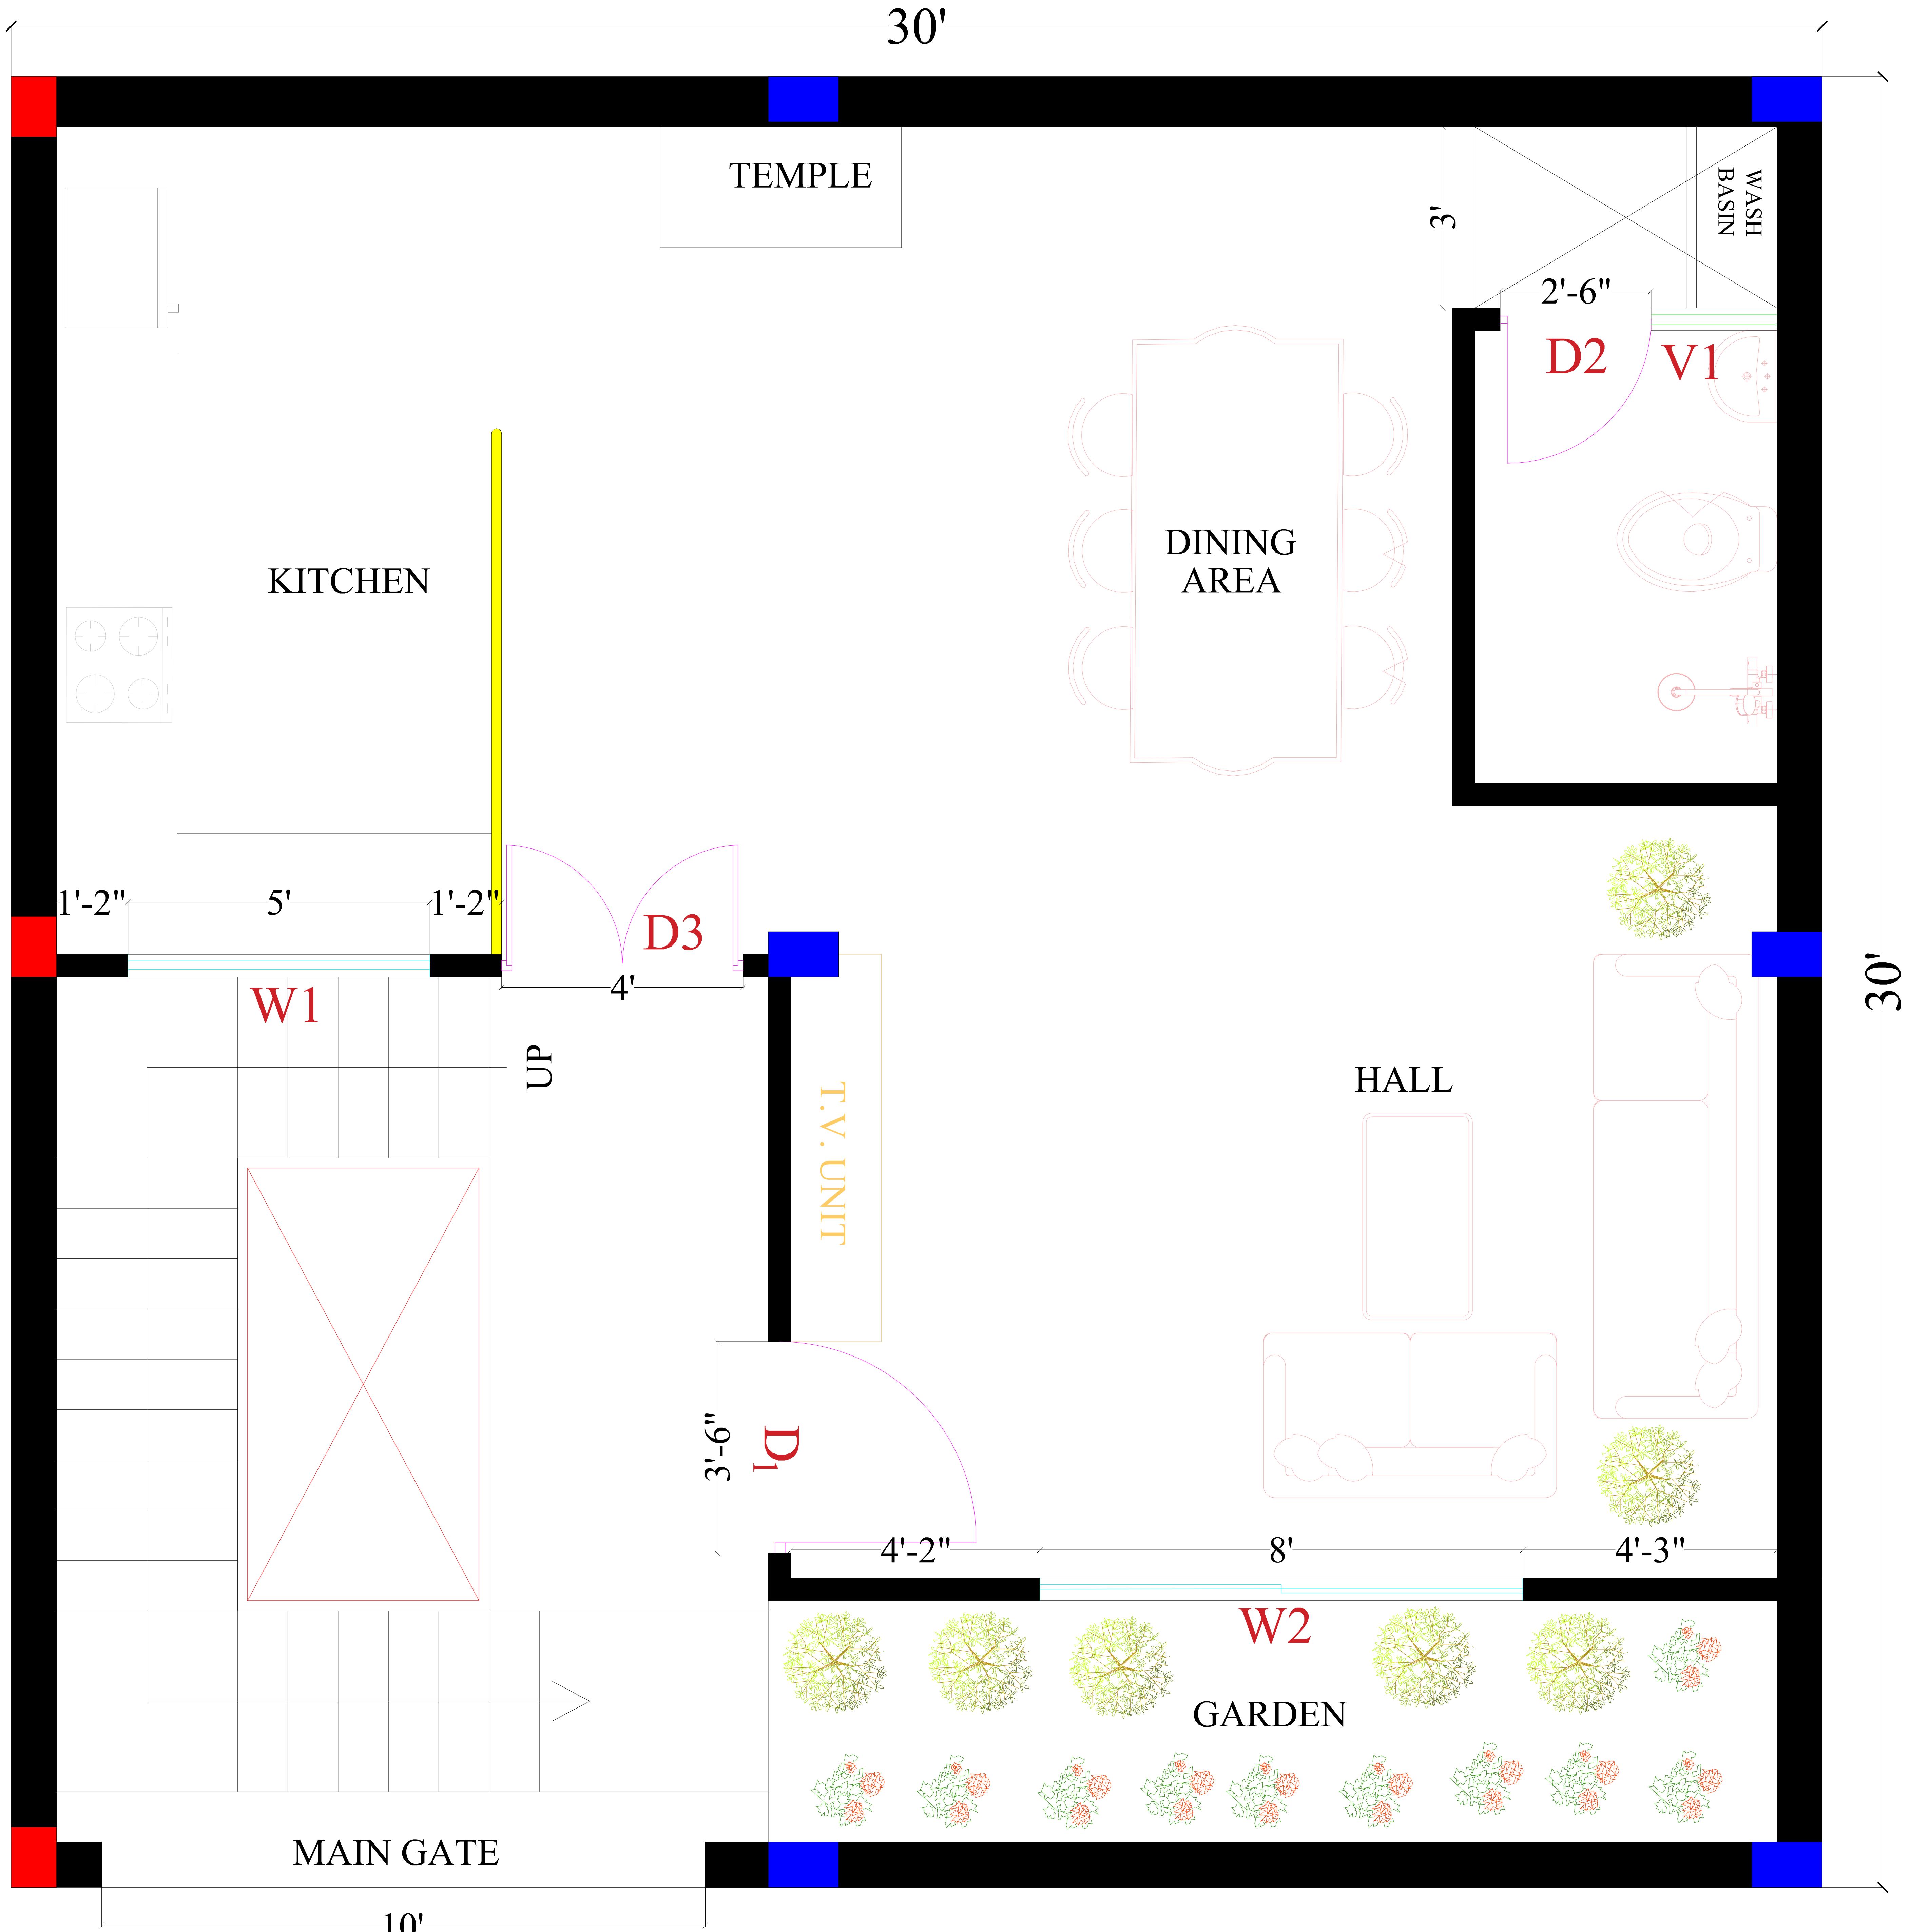

GROUND FLOOR DOOR WINDOW PLAN

This drawing, design & content is property of Architect and shall not be used, copied or reproduced without prior written permission of the firm

Follow the written dimensions only. Do not scale dimensions from drawings. Any discrepancy in the drawing or dimensions should be brought to the attention of architects prior to execution. This drawing should be read in conjunction with other drawings issued for project.


PROJECT	
Project:	Proposed House
Client:	Jhansi U.P., India Mr.Anubhav Sahu
Date :	20/05/2025

Drawn by	Drawing Status
ER.Shaalu Gupta	<input checked="" type="checkbox"/> conceptual
	<input type="checkbox"/> for approval
	<input type="checkbox"/> not for construction
	<input type="checkbox"/> for construction
	<input type="checkbox"/> as built
	<input type="checkbox"/> other _____








Drawing and scale	#LayID
WORKING	

Architects

Meerendra Buildcon
ARCHITECTURE PLANNING & INTERIOR DESIGN
Add:- 159/1, Ayodhapuri gwalior road, Jhansi (U.P)
Mob:- 9450076030, 8299732040.
E-mail:- meerendra_07@gmail.com

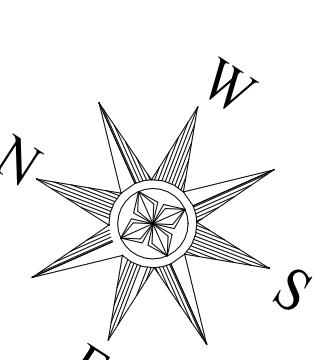


GROUND FLOOR DOOR WINDOW SCHEDULE

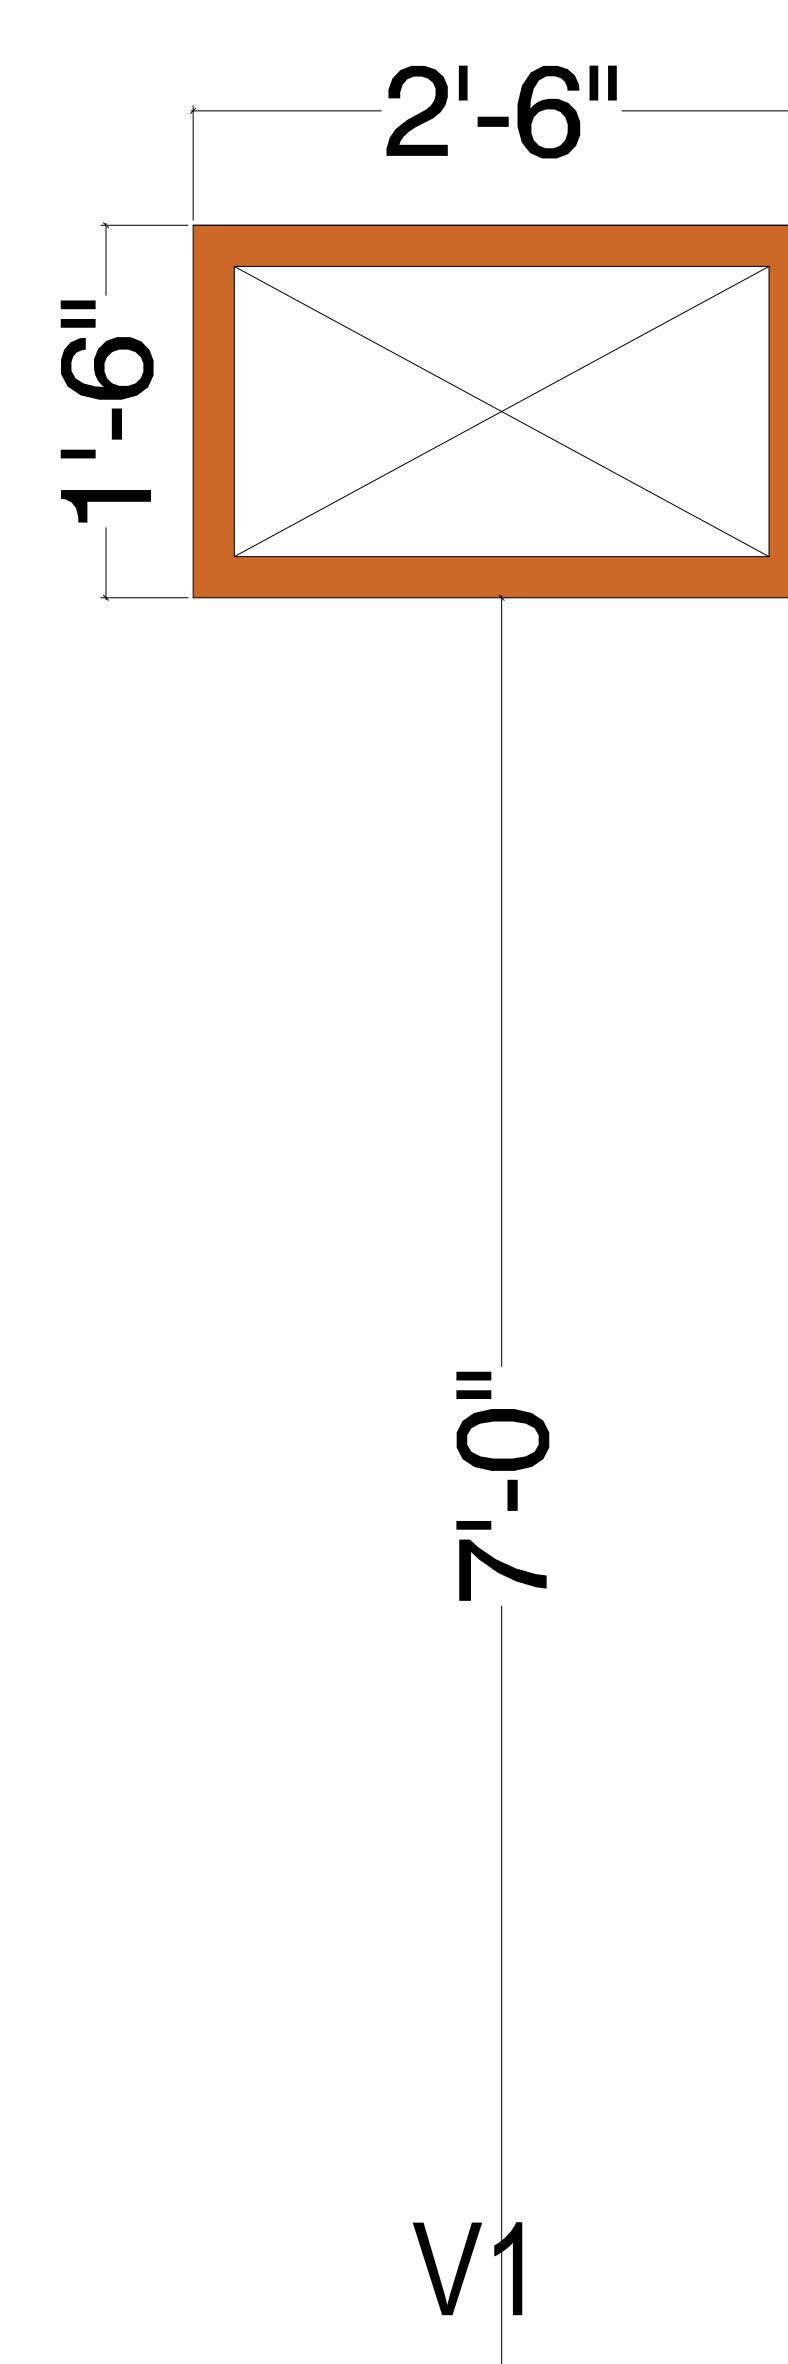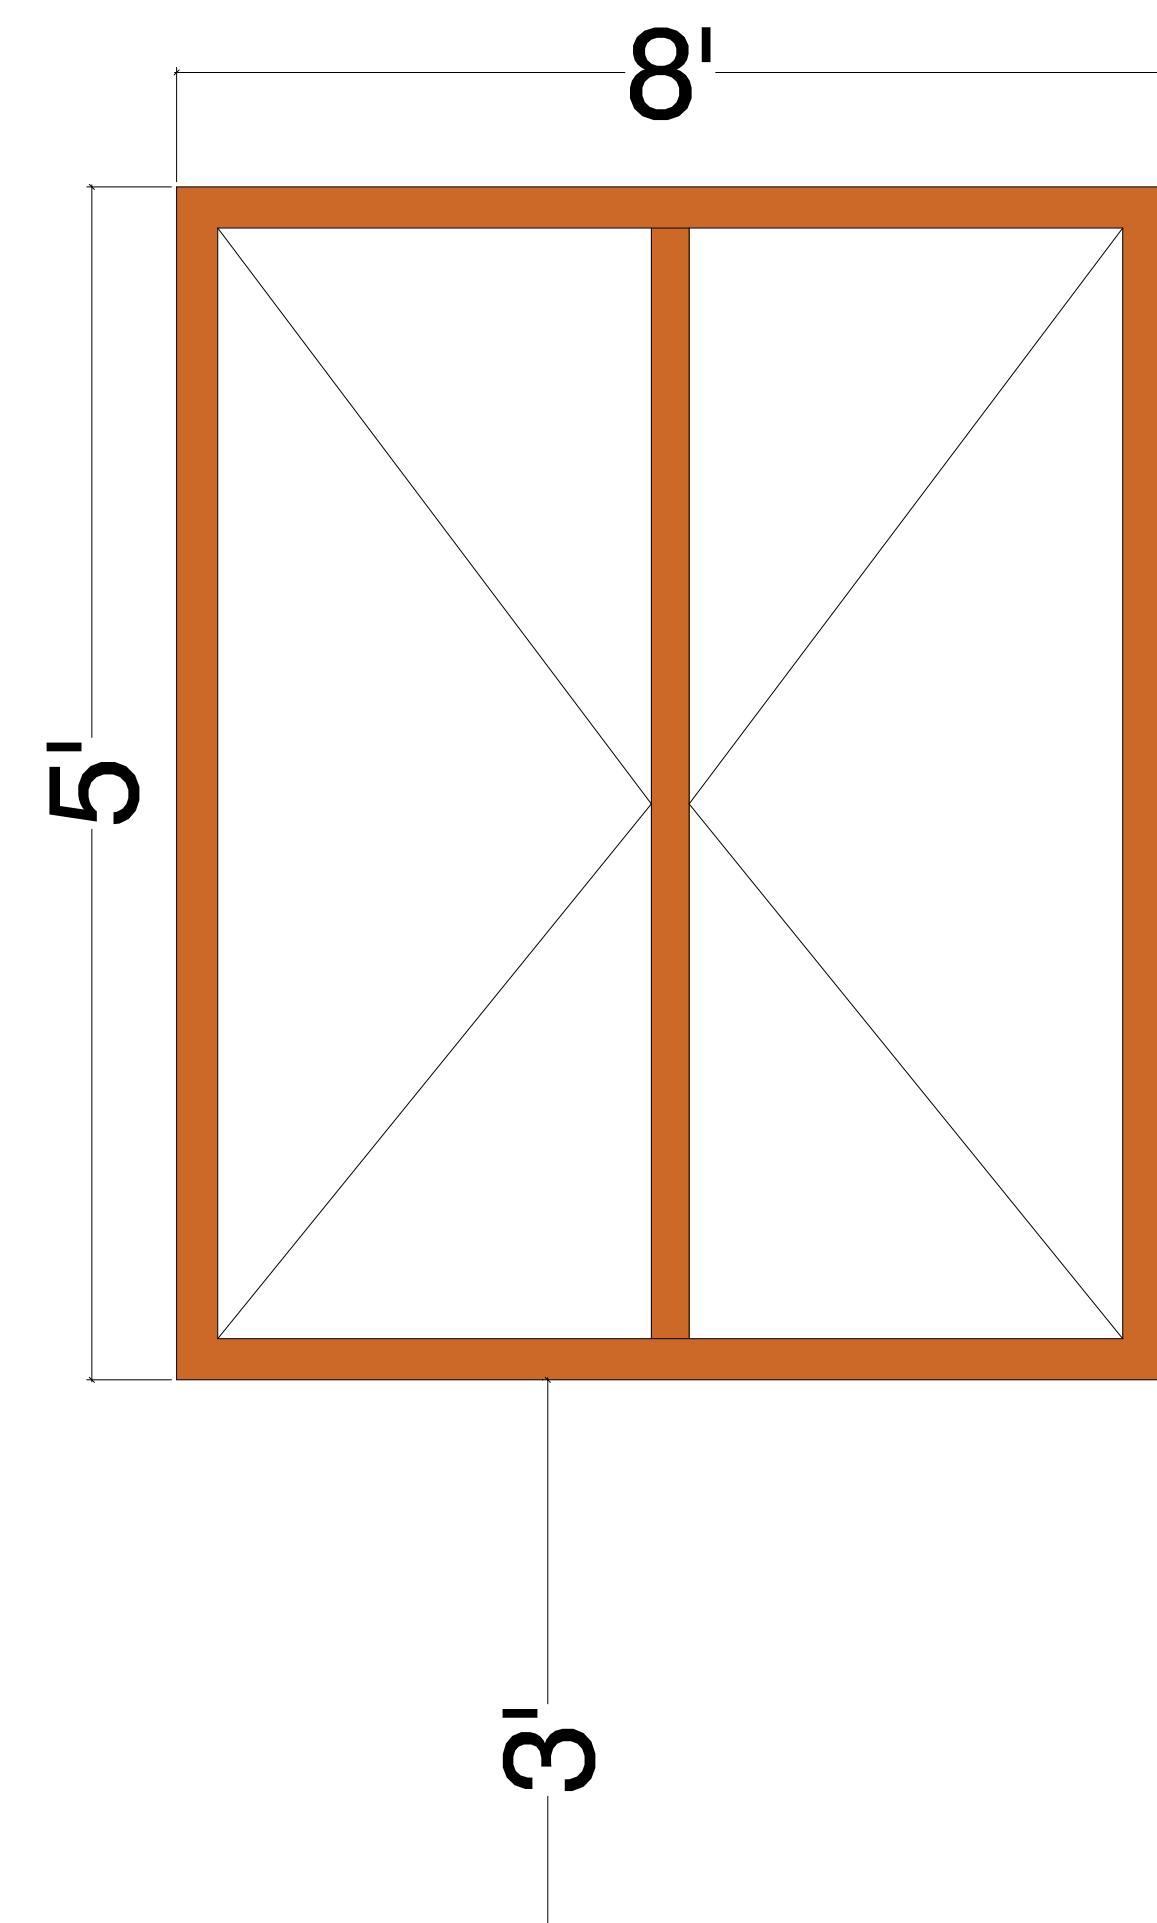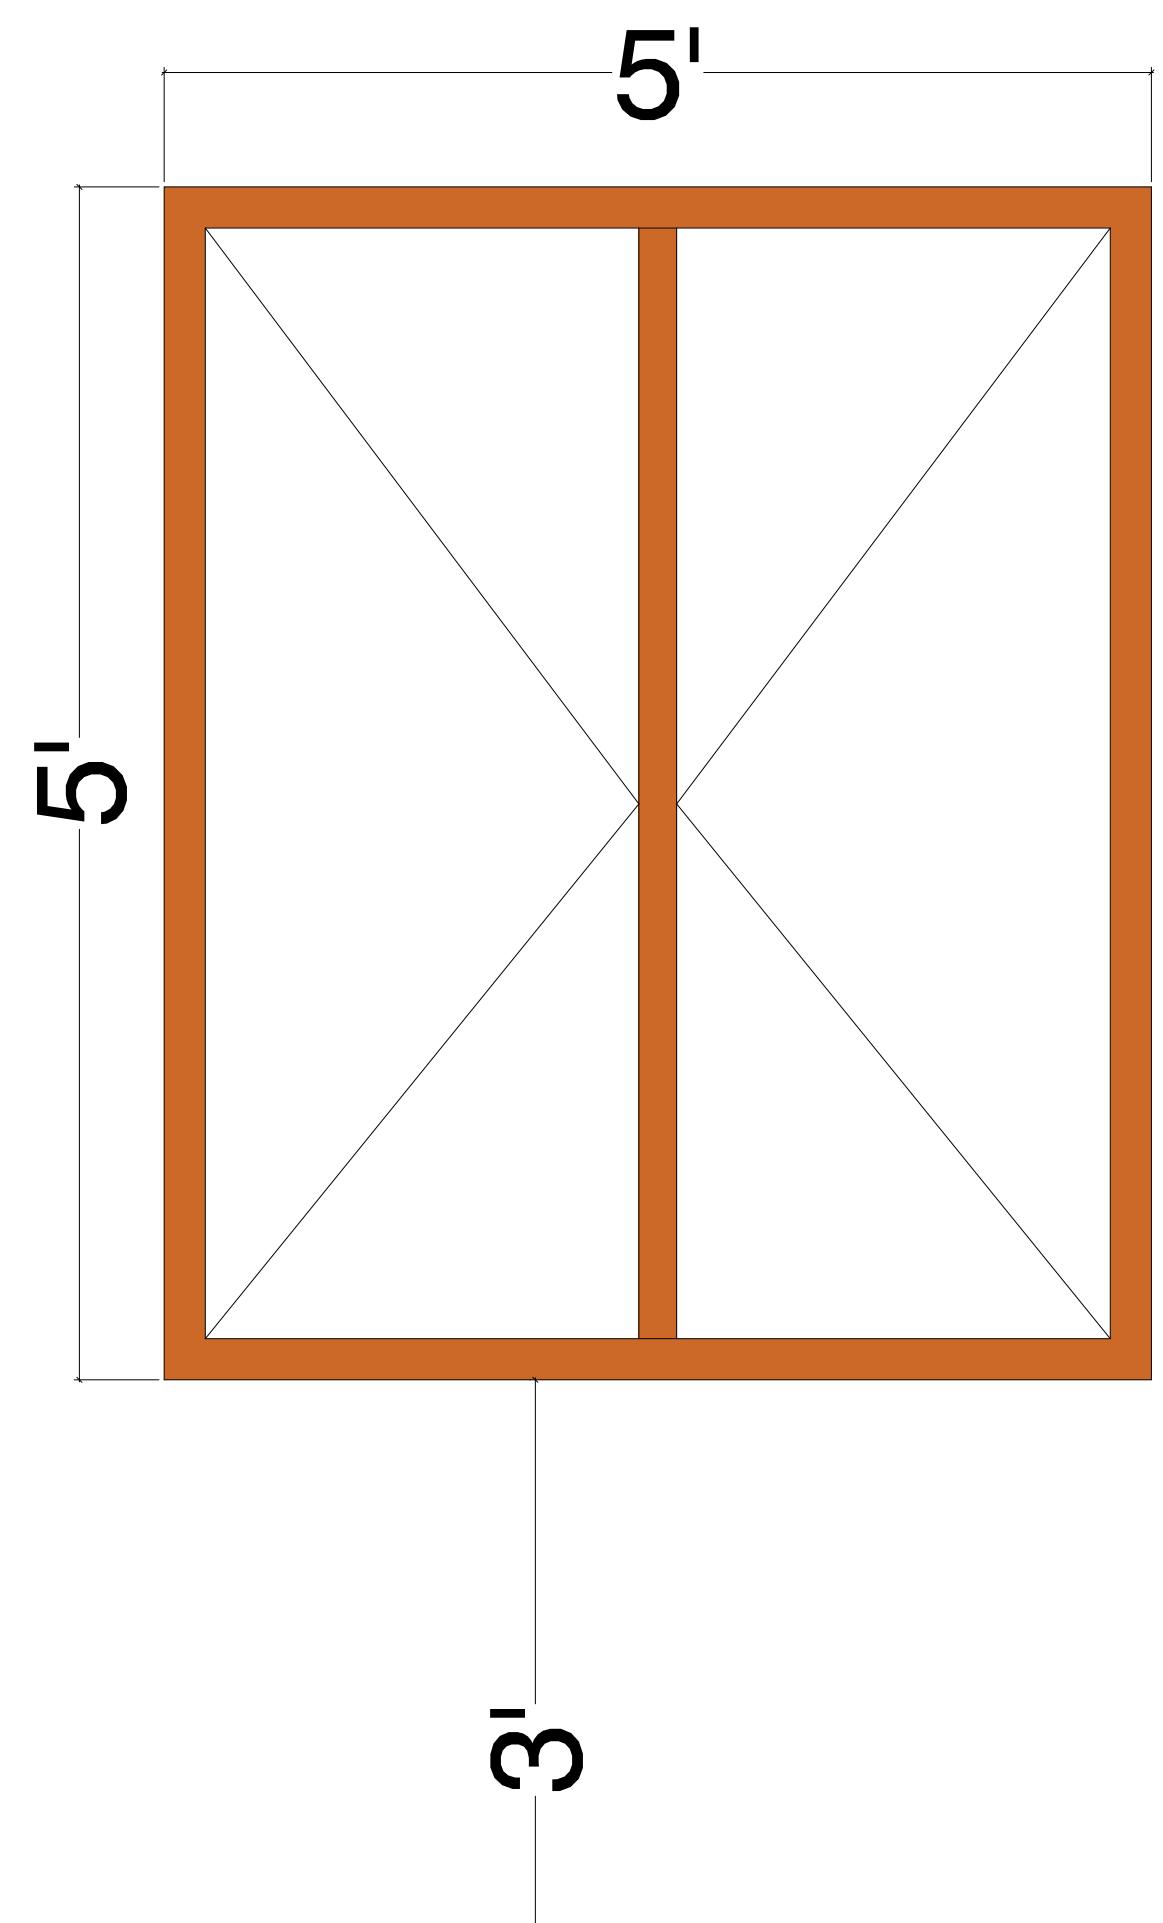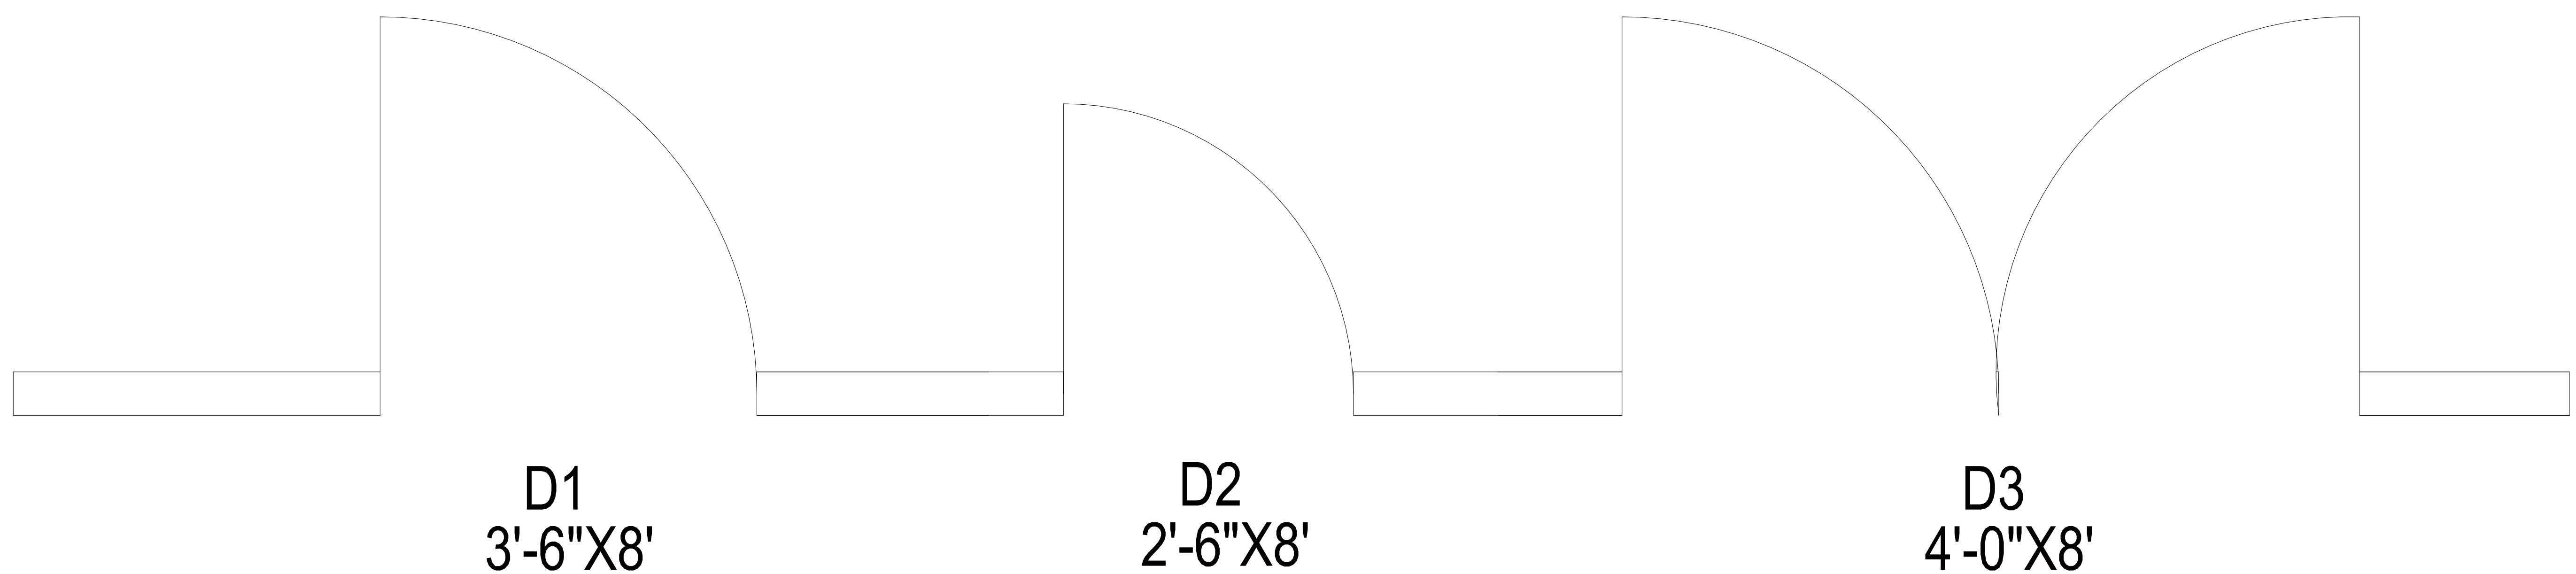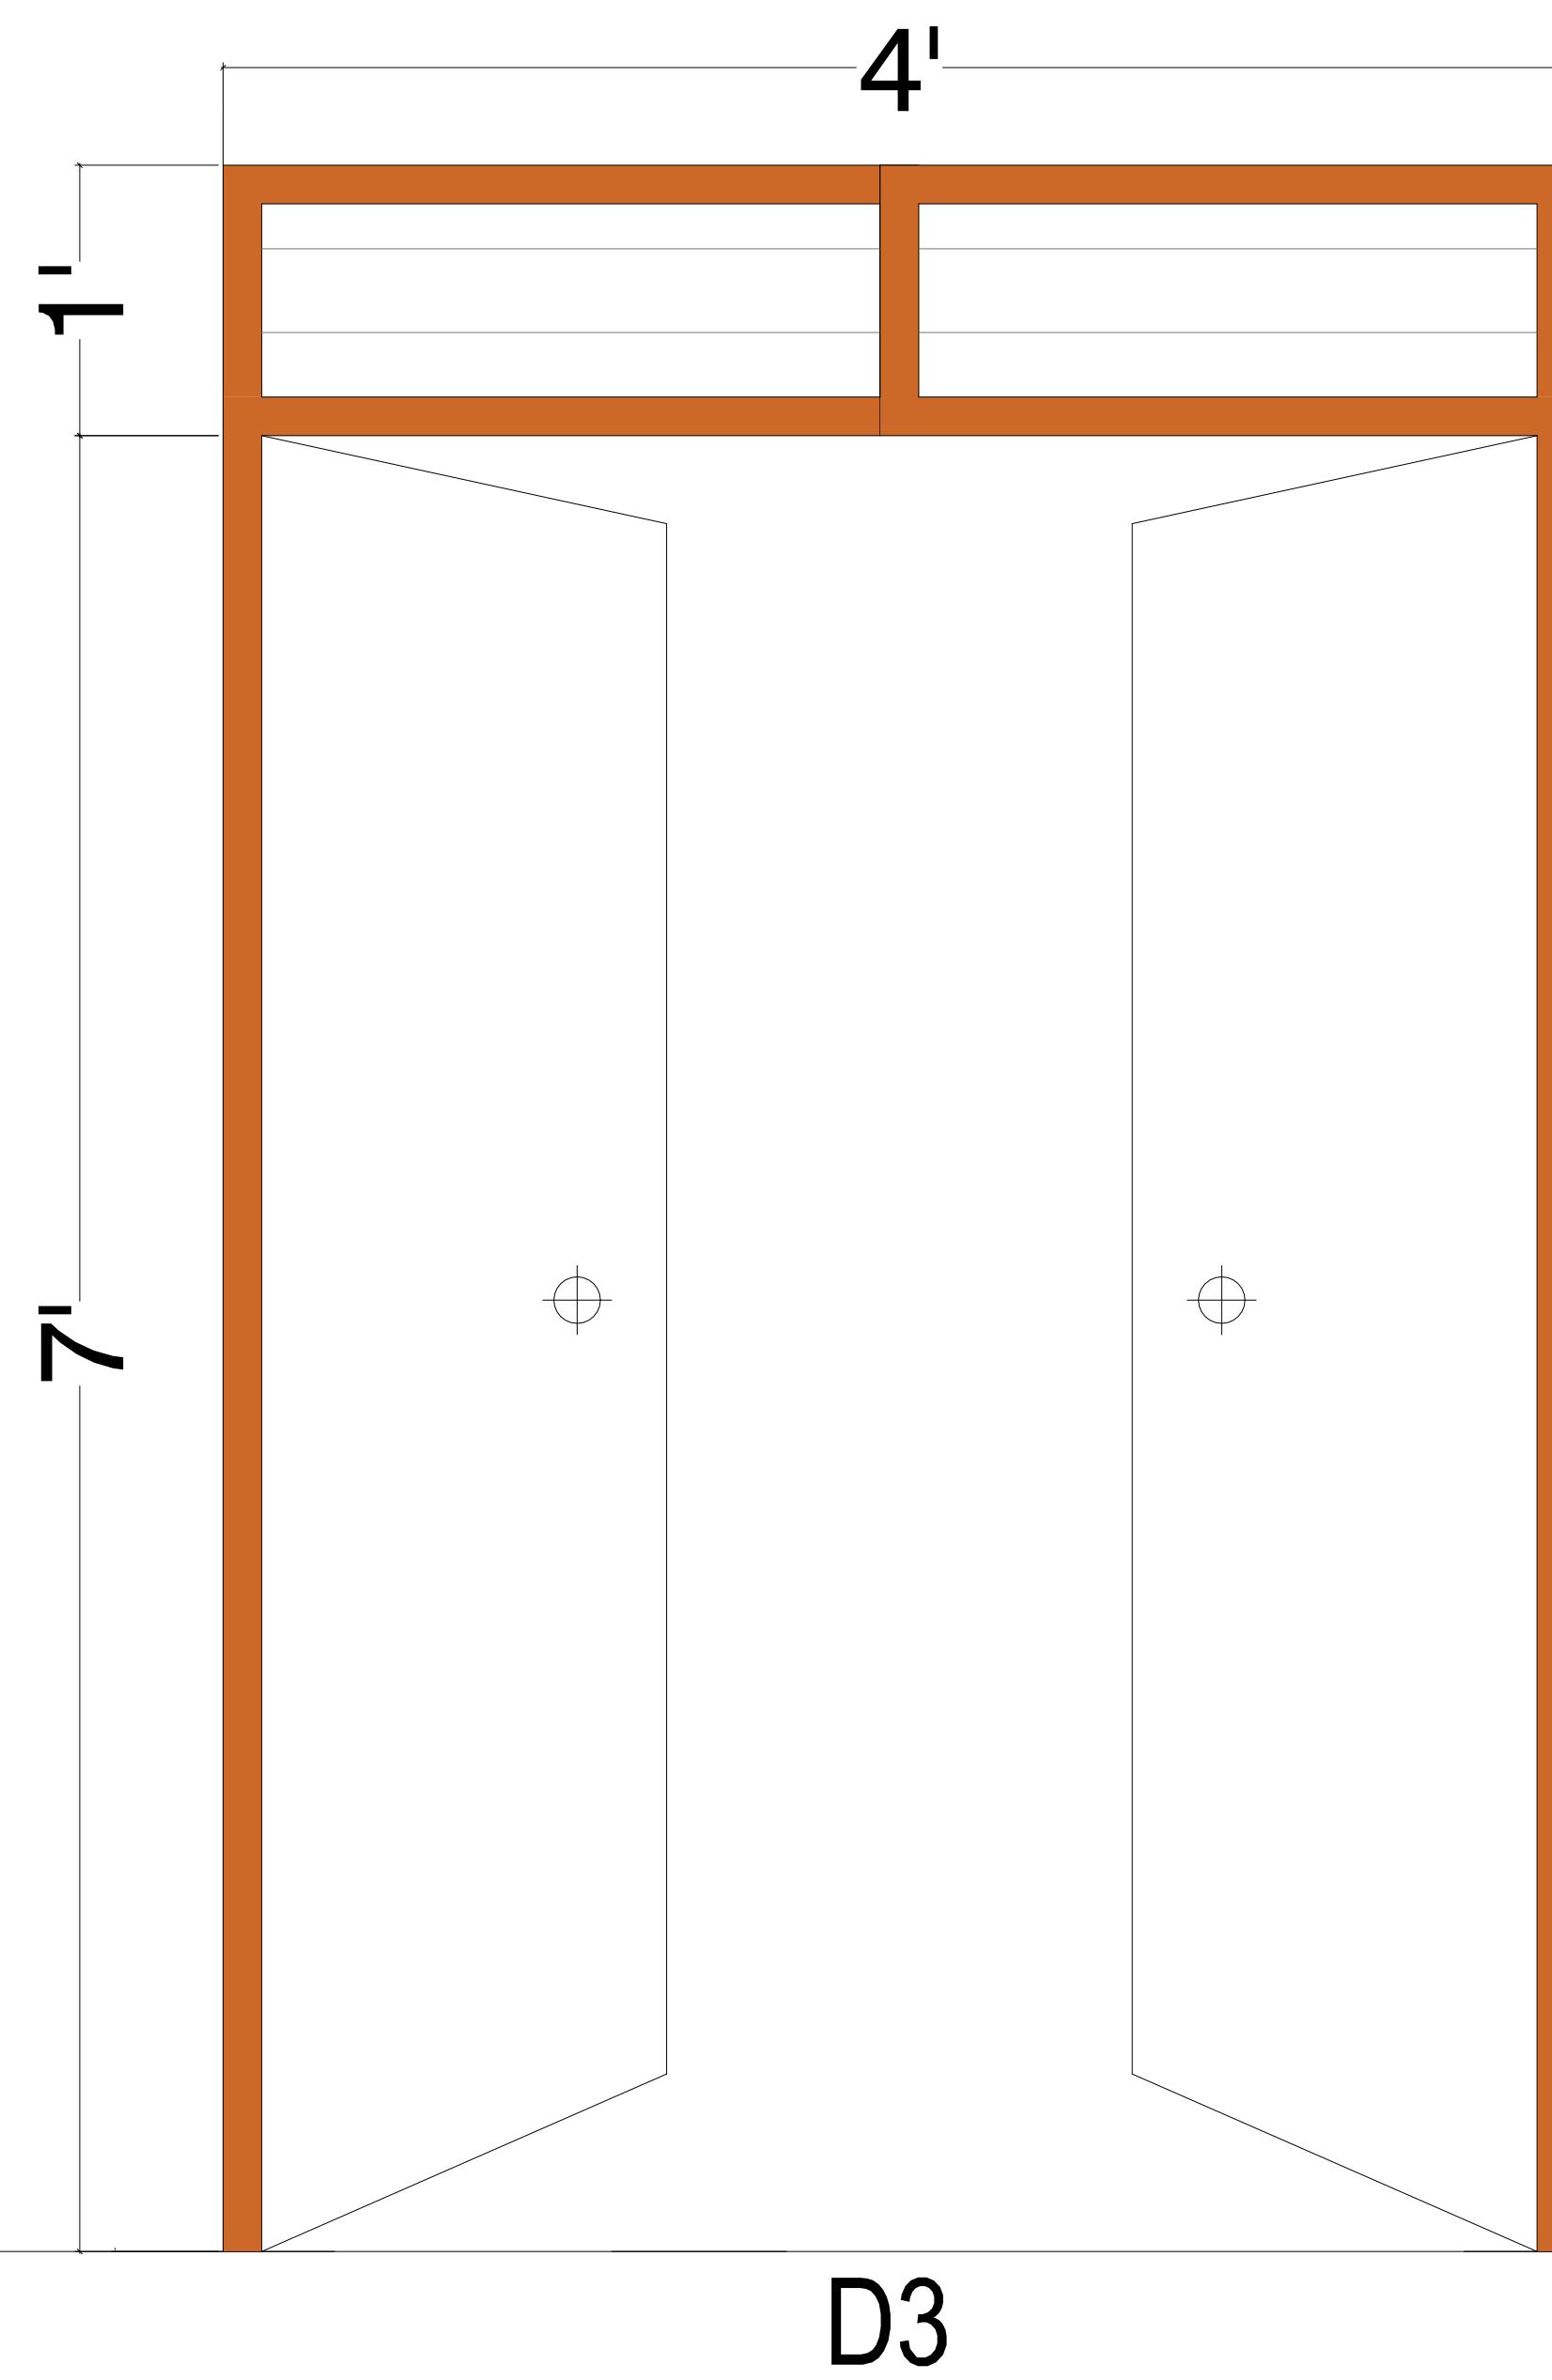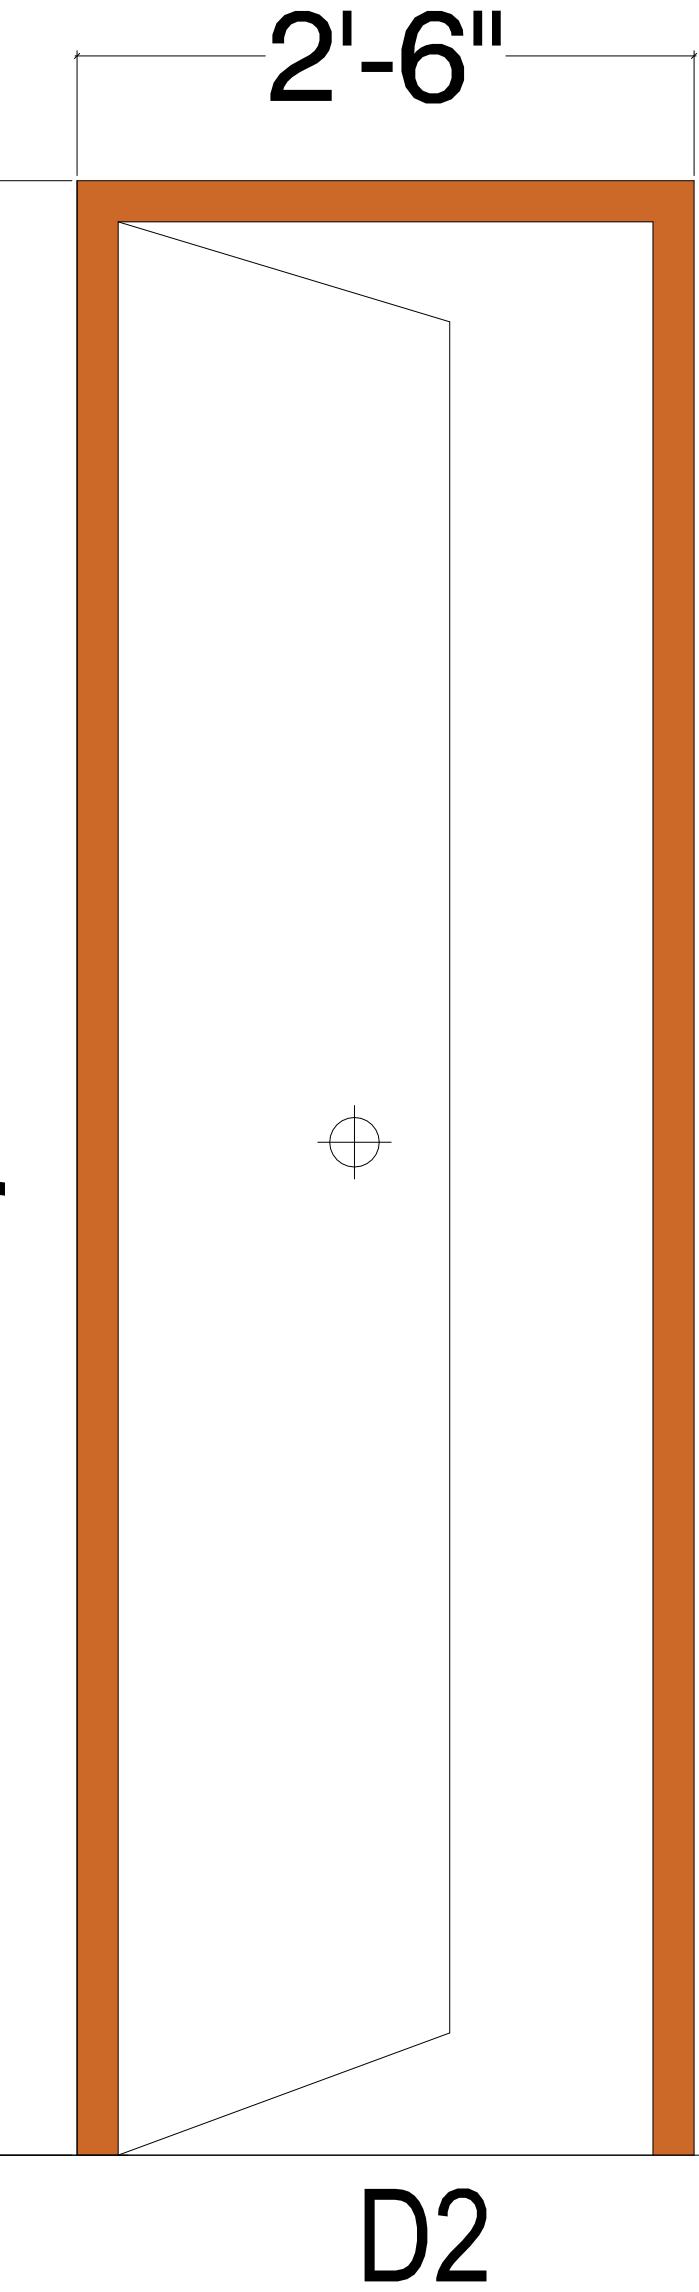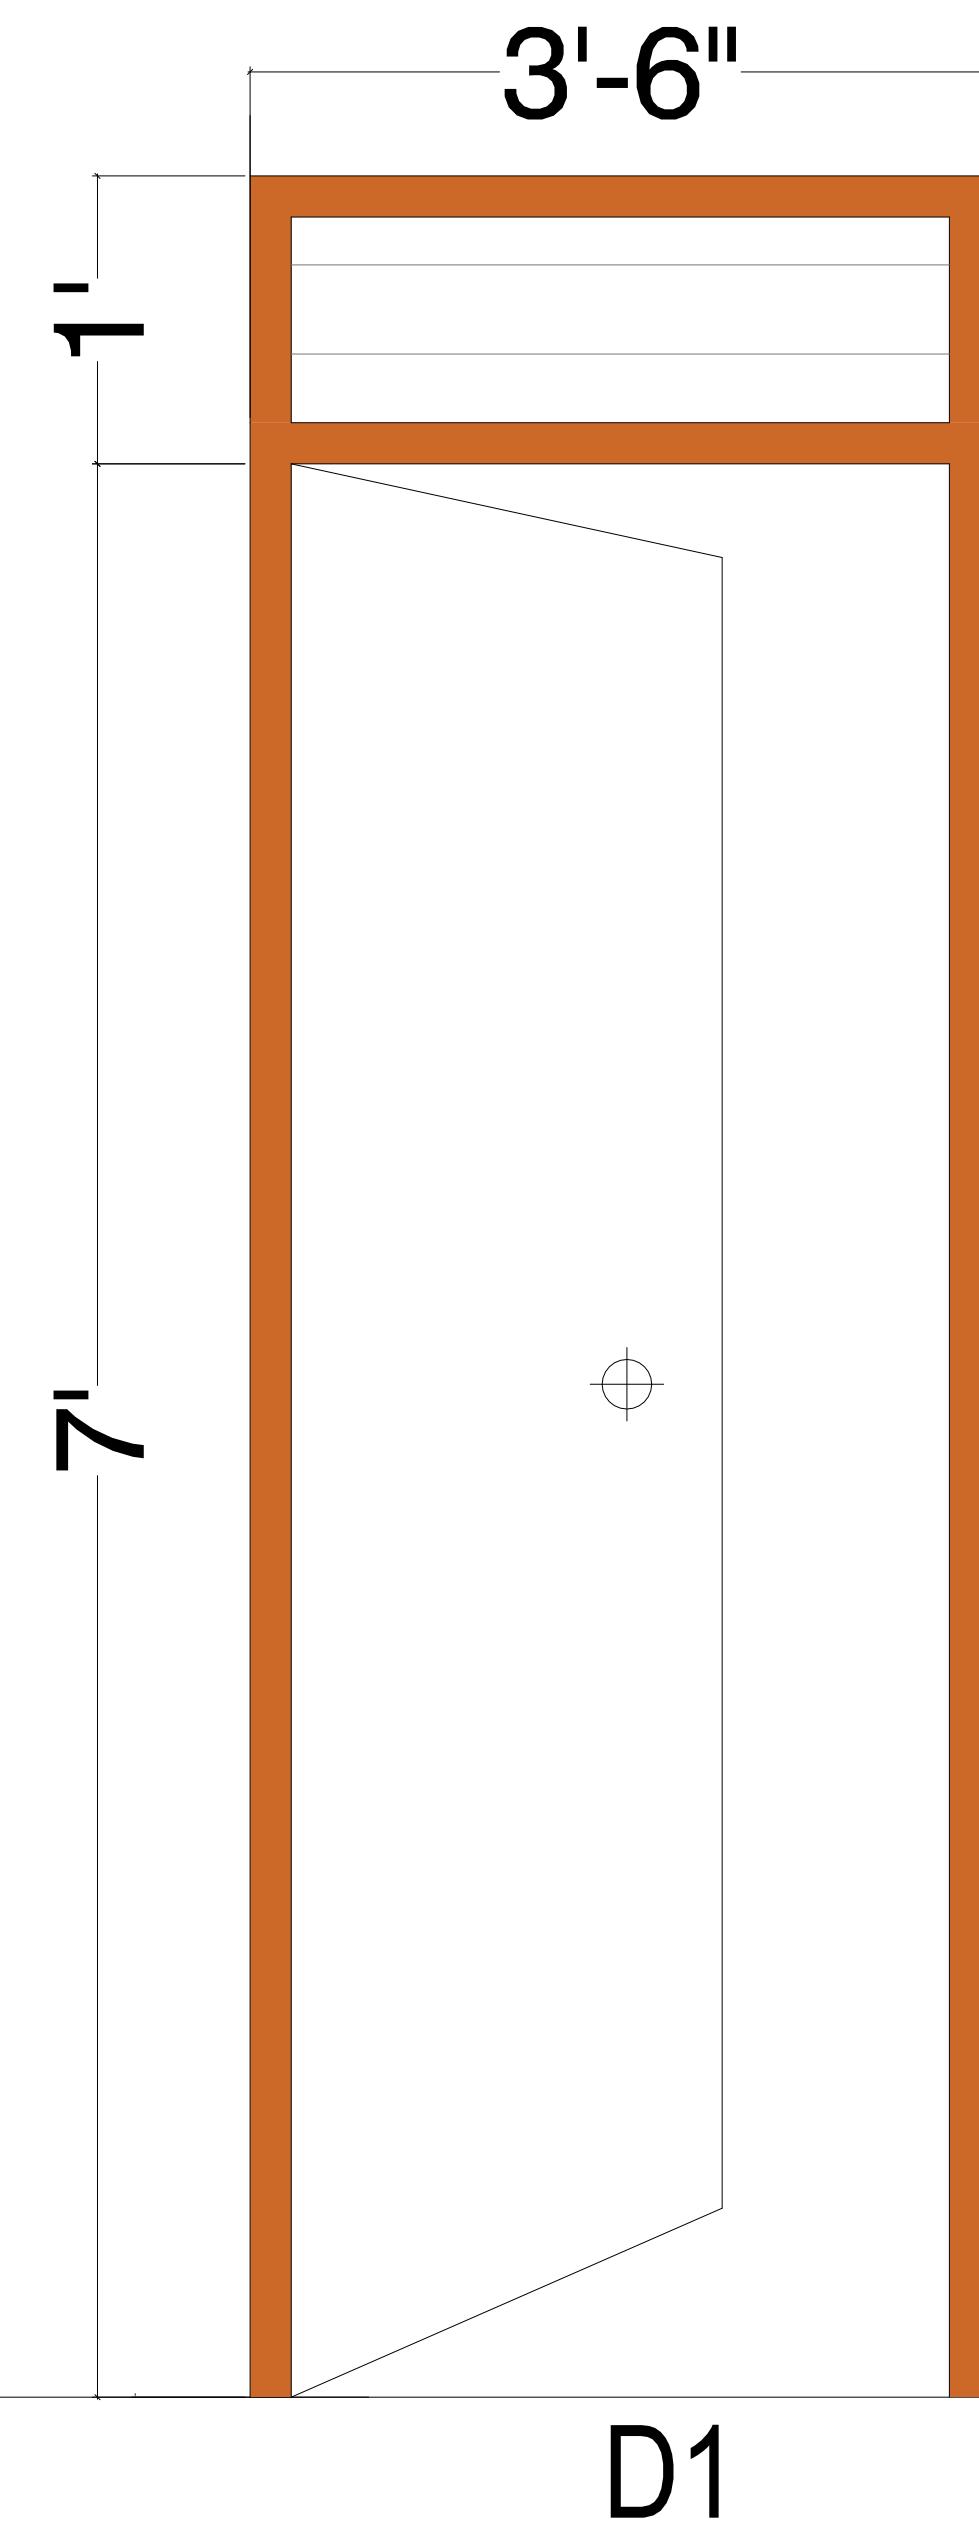

W1
5'X5'

W2
8'X5'

V1
2'-6"X1'-6"

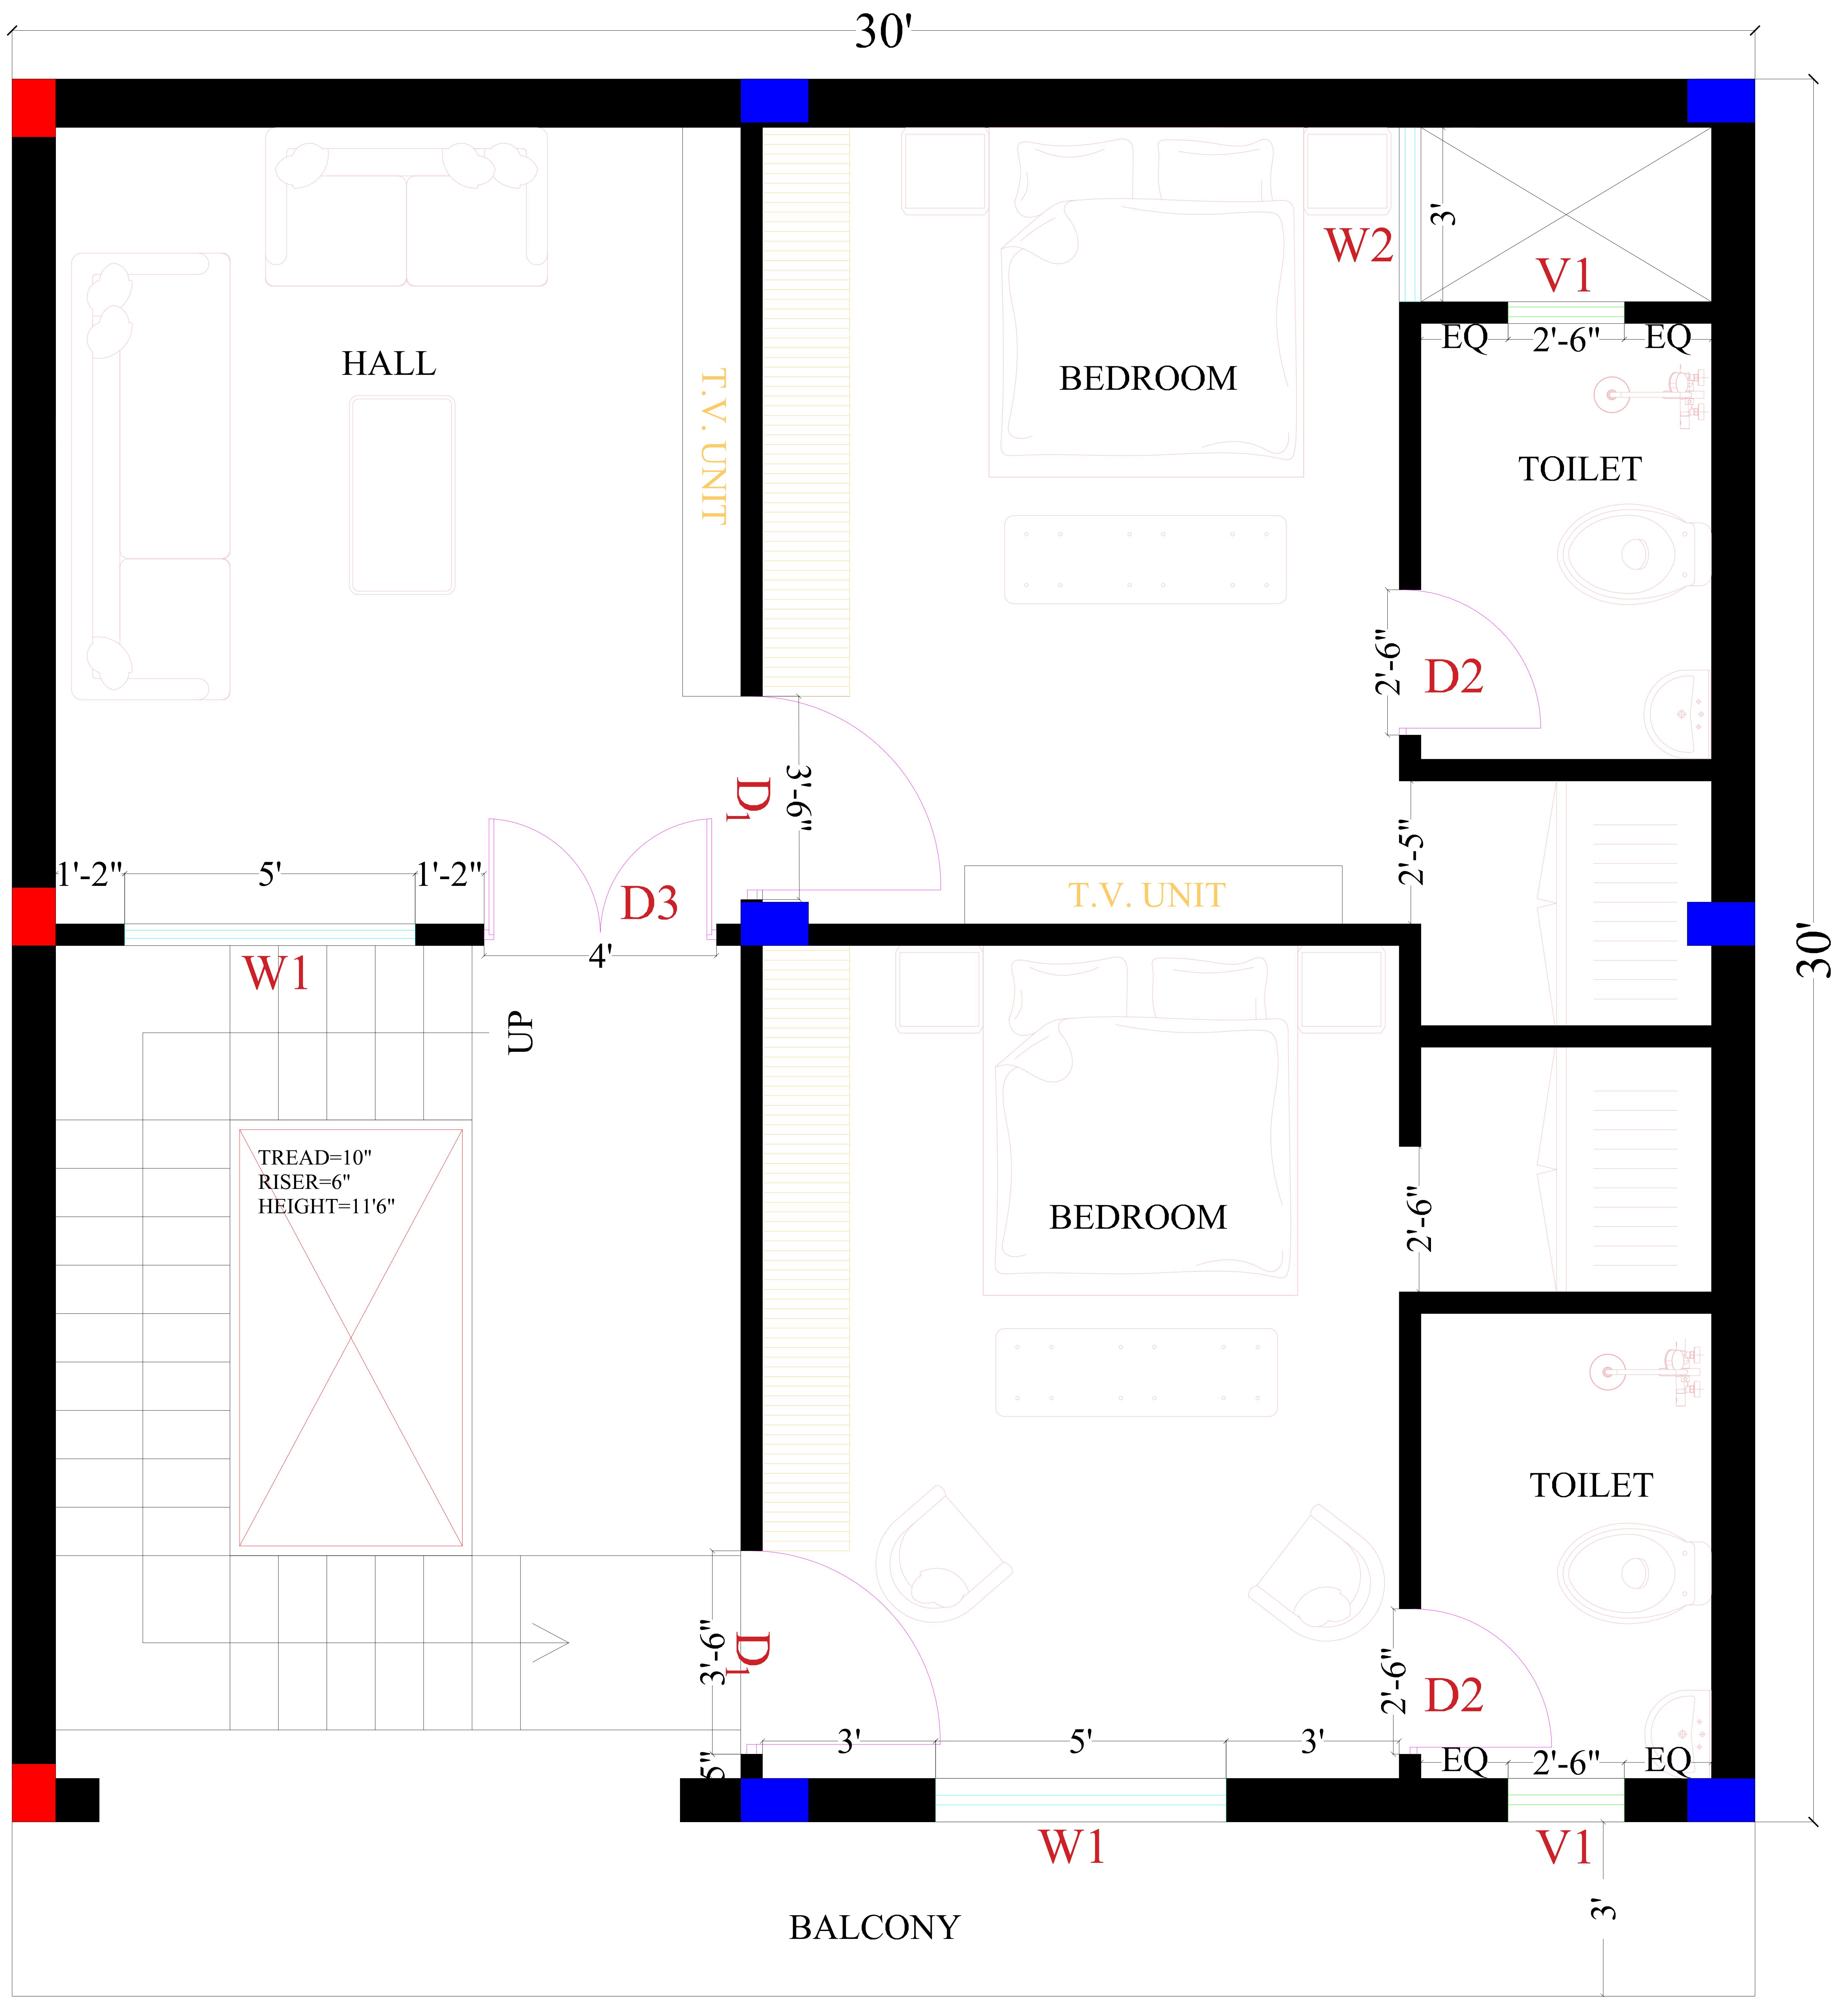

FIRST FLOOR DOOR WINDOW PLAN

This drawing, design & content is property of Architect and shall not be used, copied or reproduced without prior written permission of the firm

Follow the written dimensions only. Do not scale dimensions from drawings. Any discrepancy in the drawing or dimensions should be brought to the attention of architects prior to execution. This drawing should be read in conjunction with other drawings issued for project.

PROJECT	
Project:	Proposed House
Client:	Jhansi U.P., India Mr.Anubhav Sahu
Date:	20/05/2025

Drawn by
ER.Shaalu Gupta

Checked by
Er. Sankalp Tiwari

Date : 20/05/2025


Drawing Status
 conceptual
 for approval
 not for construction
 for construction
 as built
 other _____

Drawing and scale
WORKING




#LayID


Architects
Meerendra Buildcon
ARCHITECTURE PLANNING & INTERIOR DESIGN

Add:- 159/1, Ayodhapuri gwalior road, jhansi (U.P)
Mob:- 9450076030, 8299732040.
E-mail:- meerendra_07@gmail.com

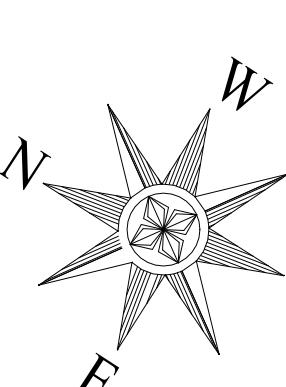

FIRST FLOOR DOOR WINDOW SCHEDULE

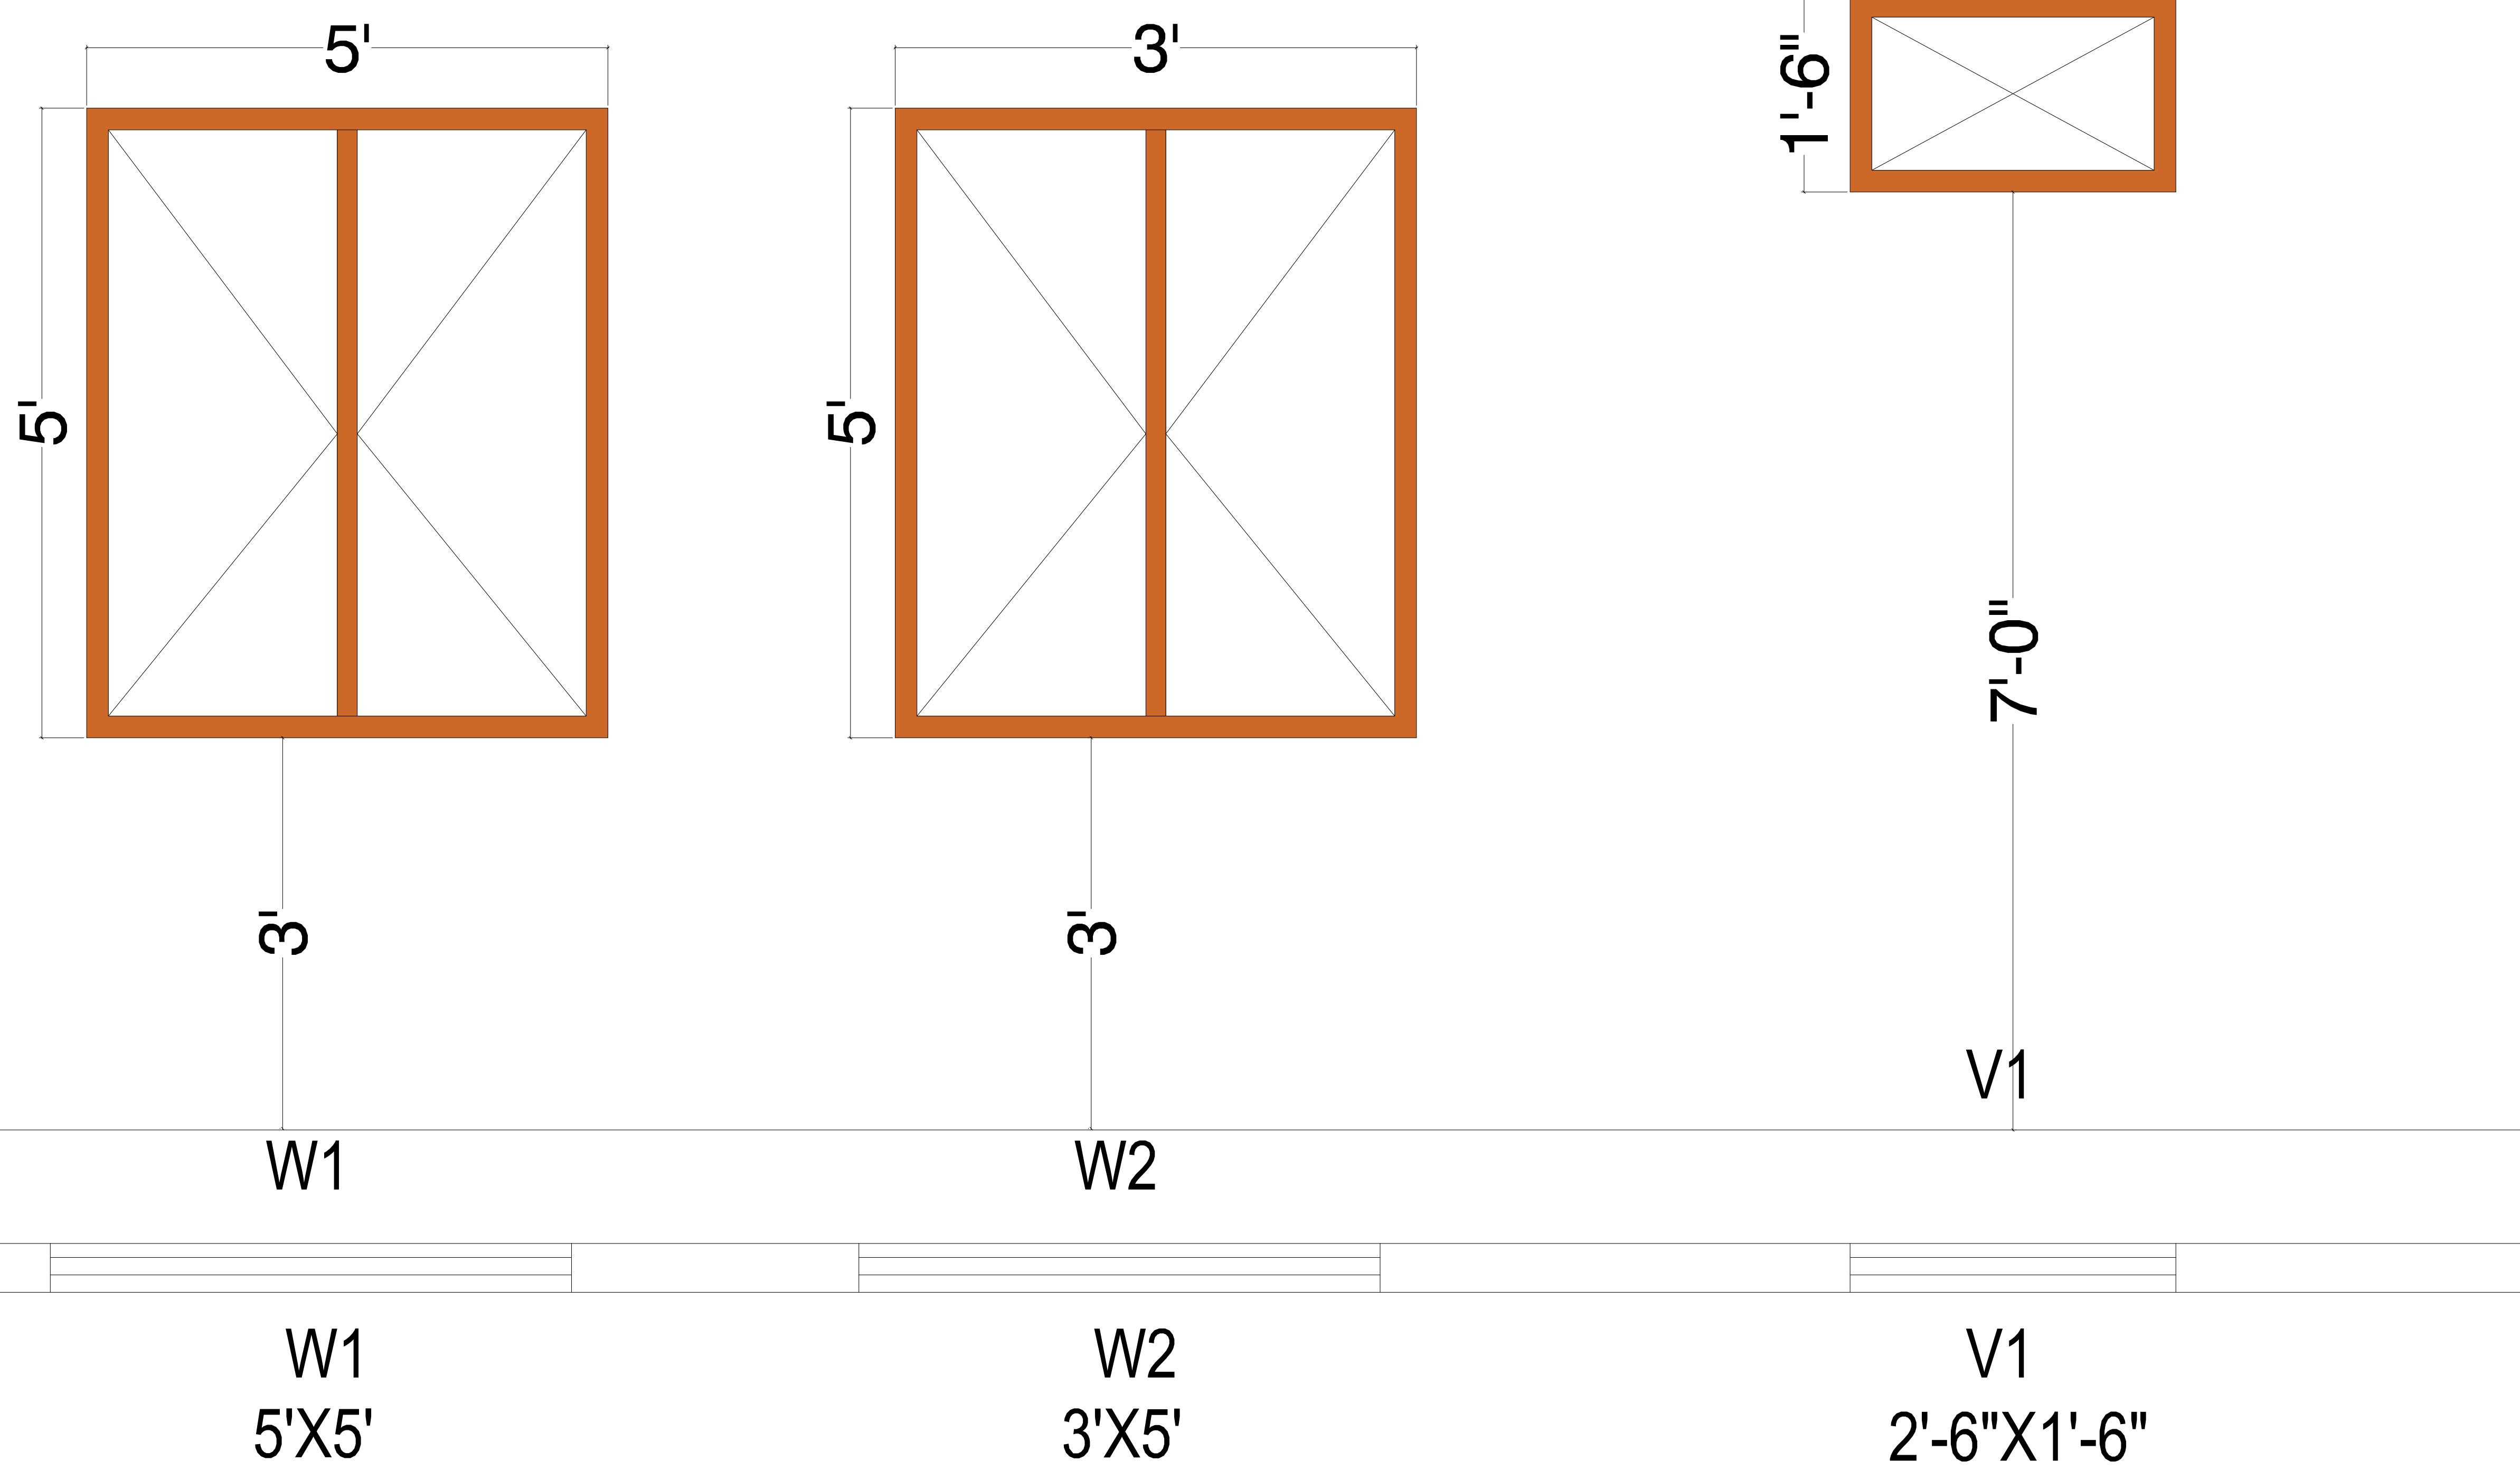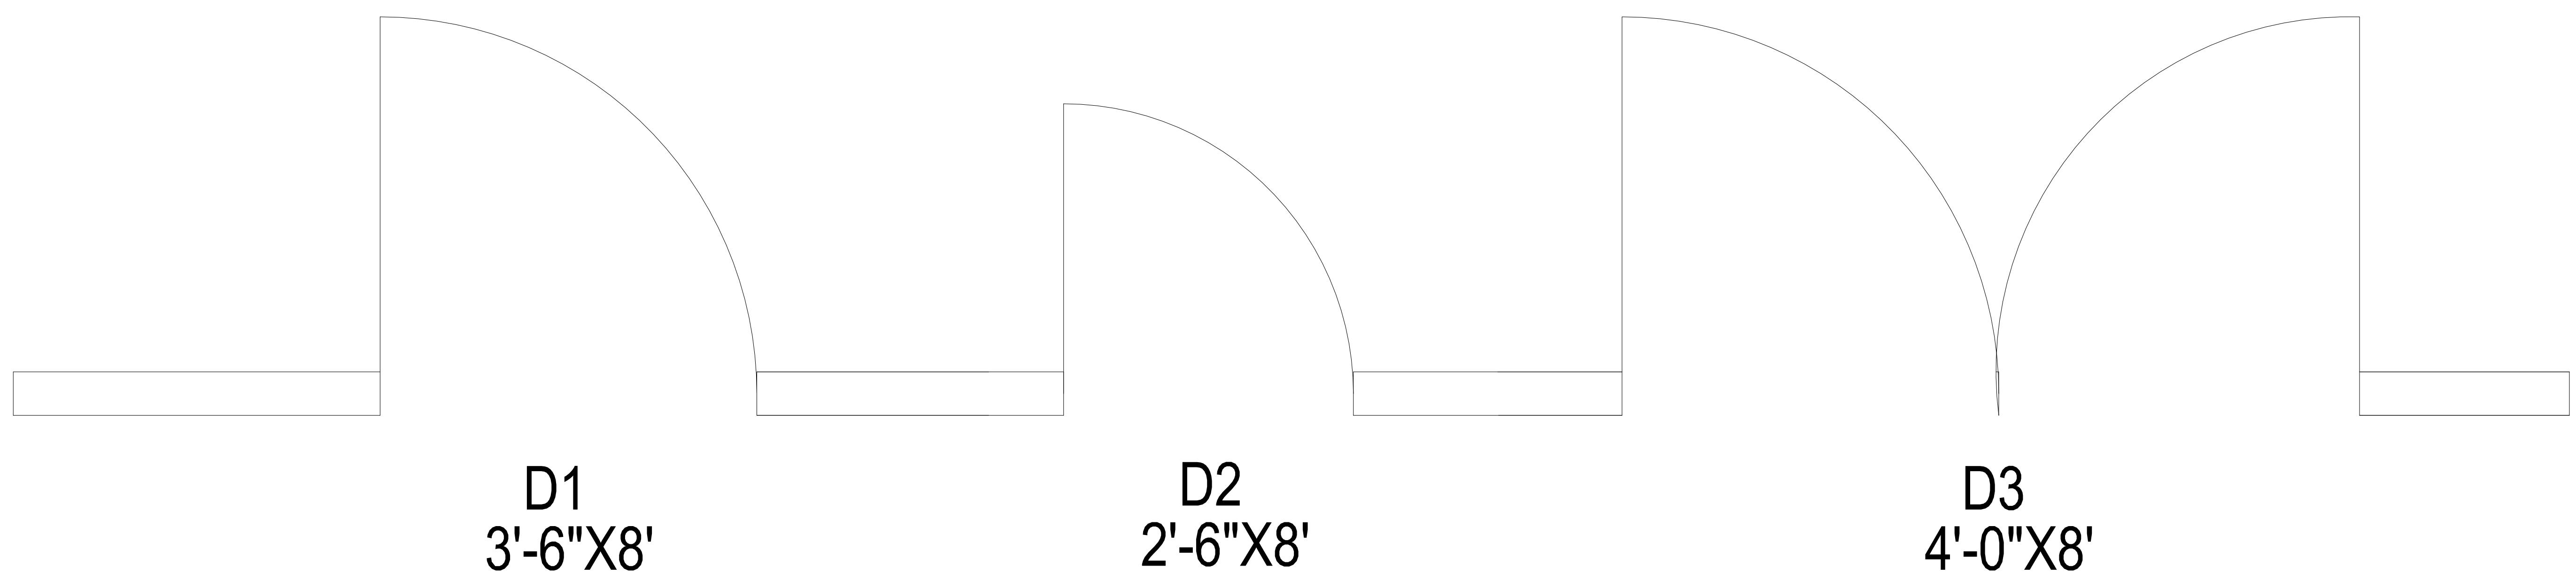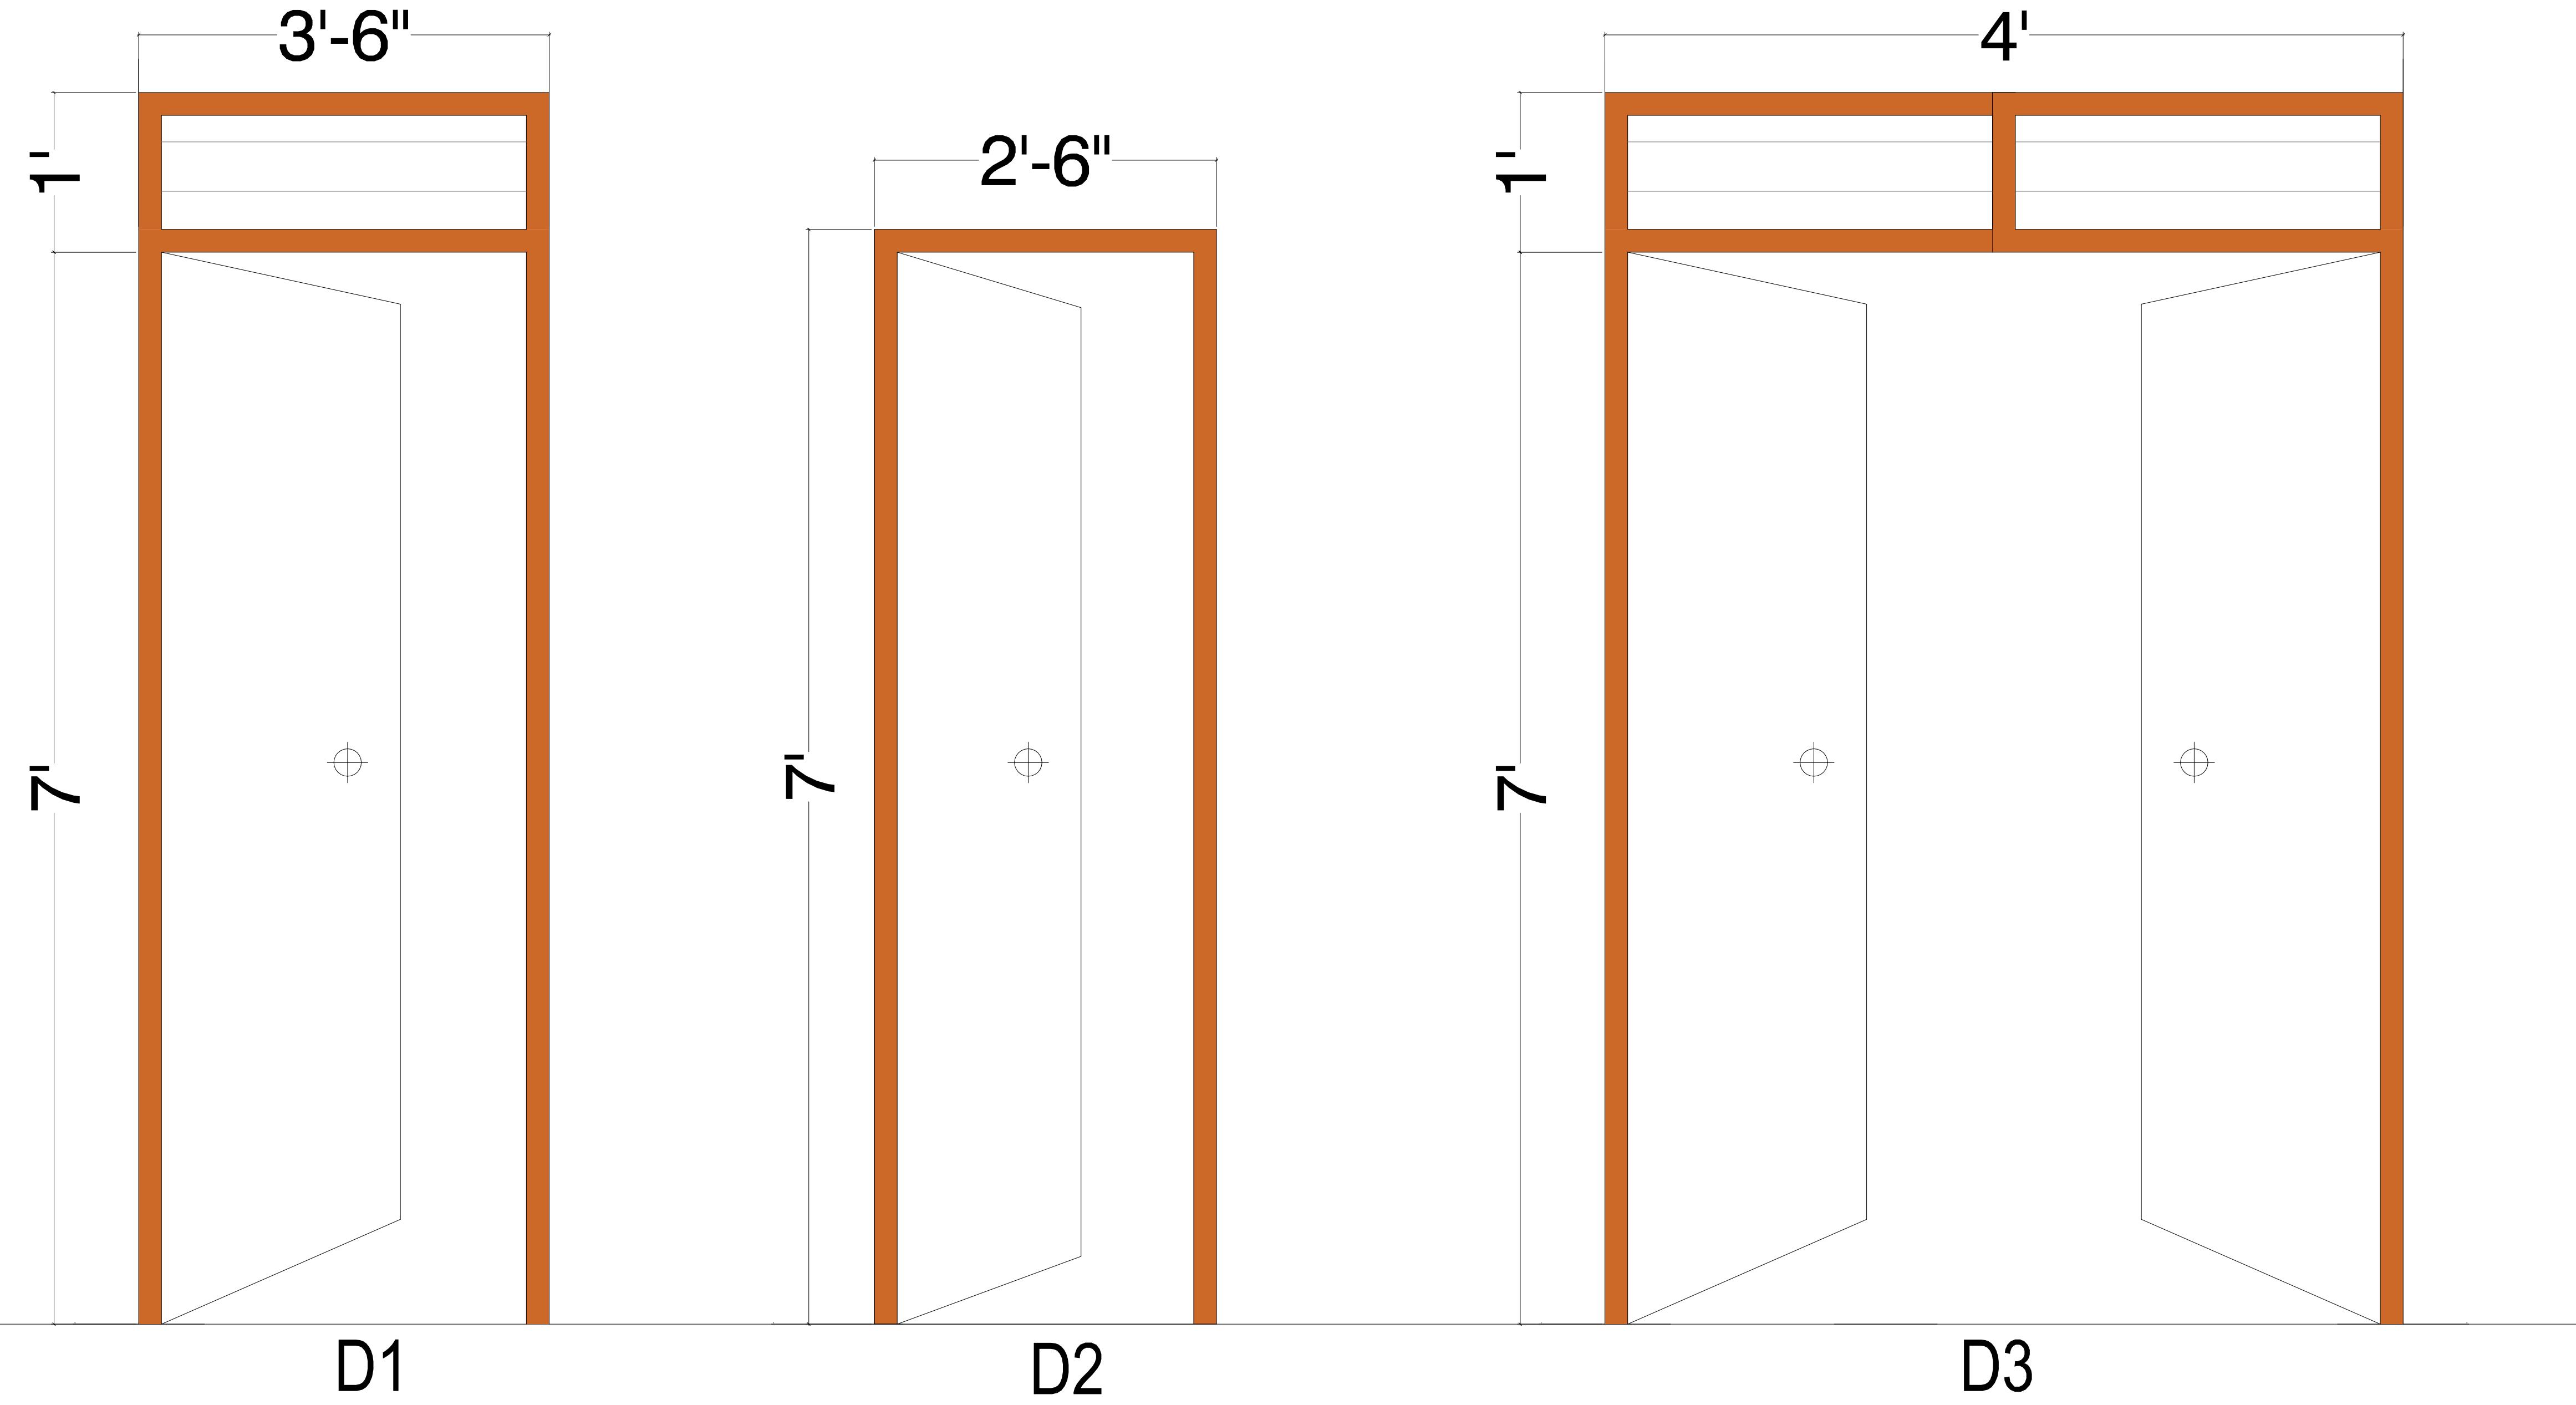

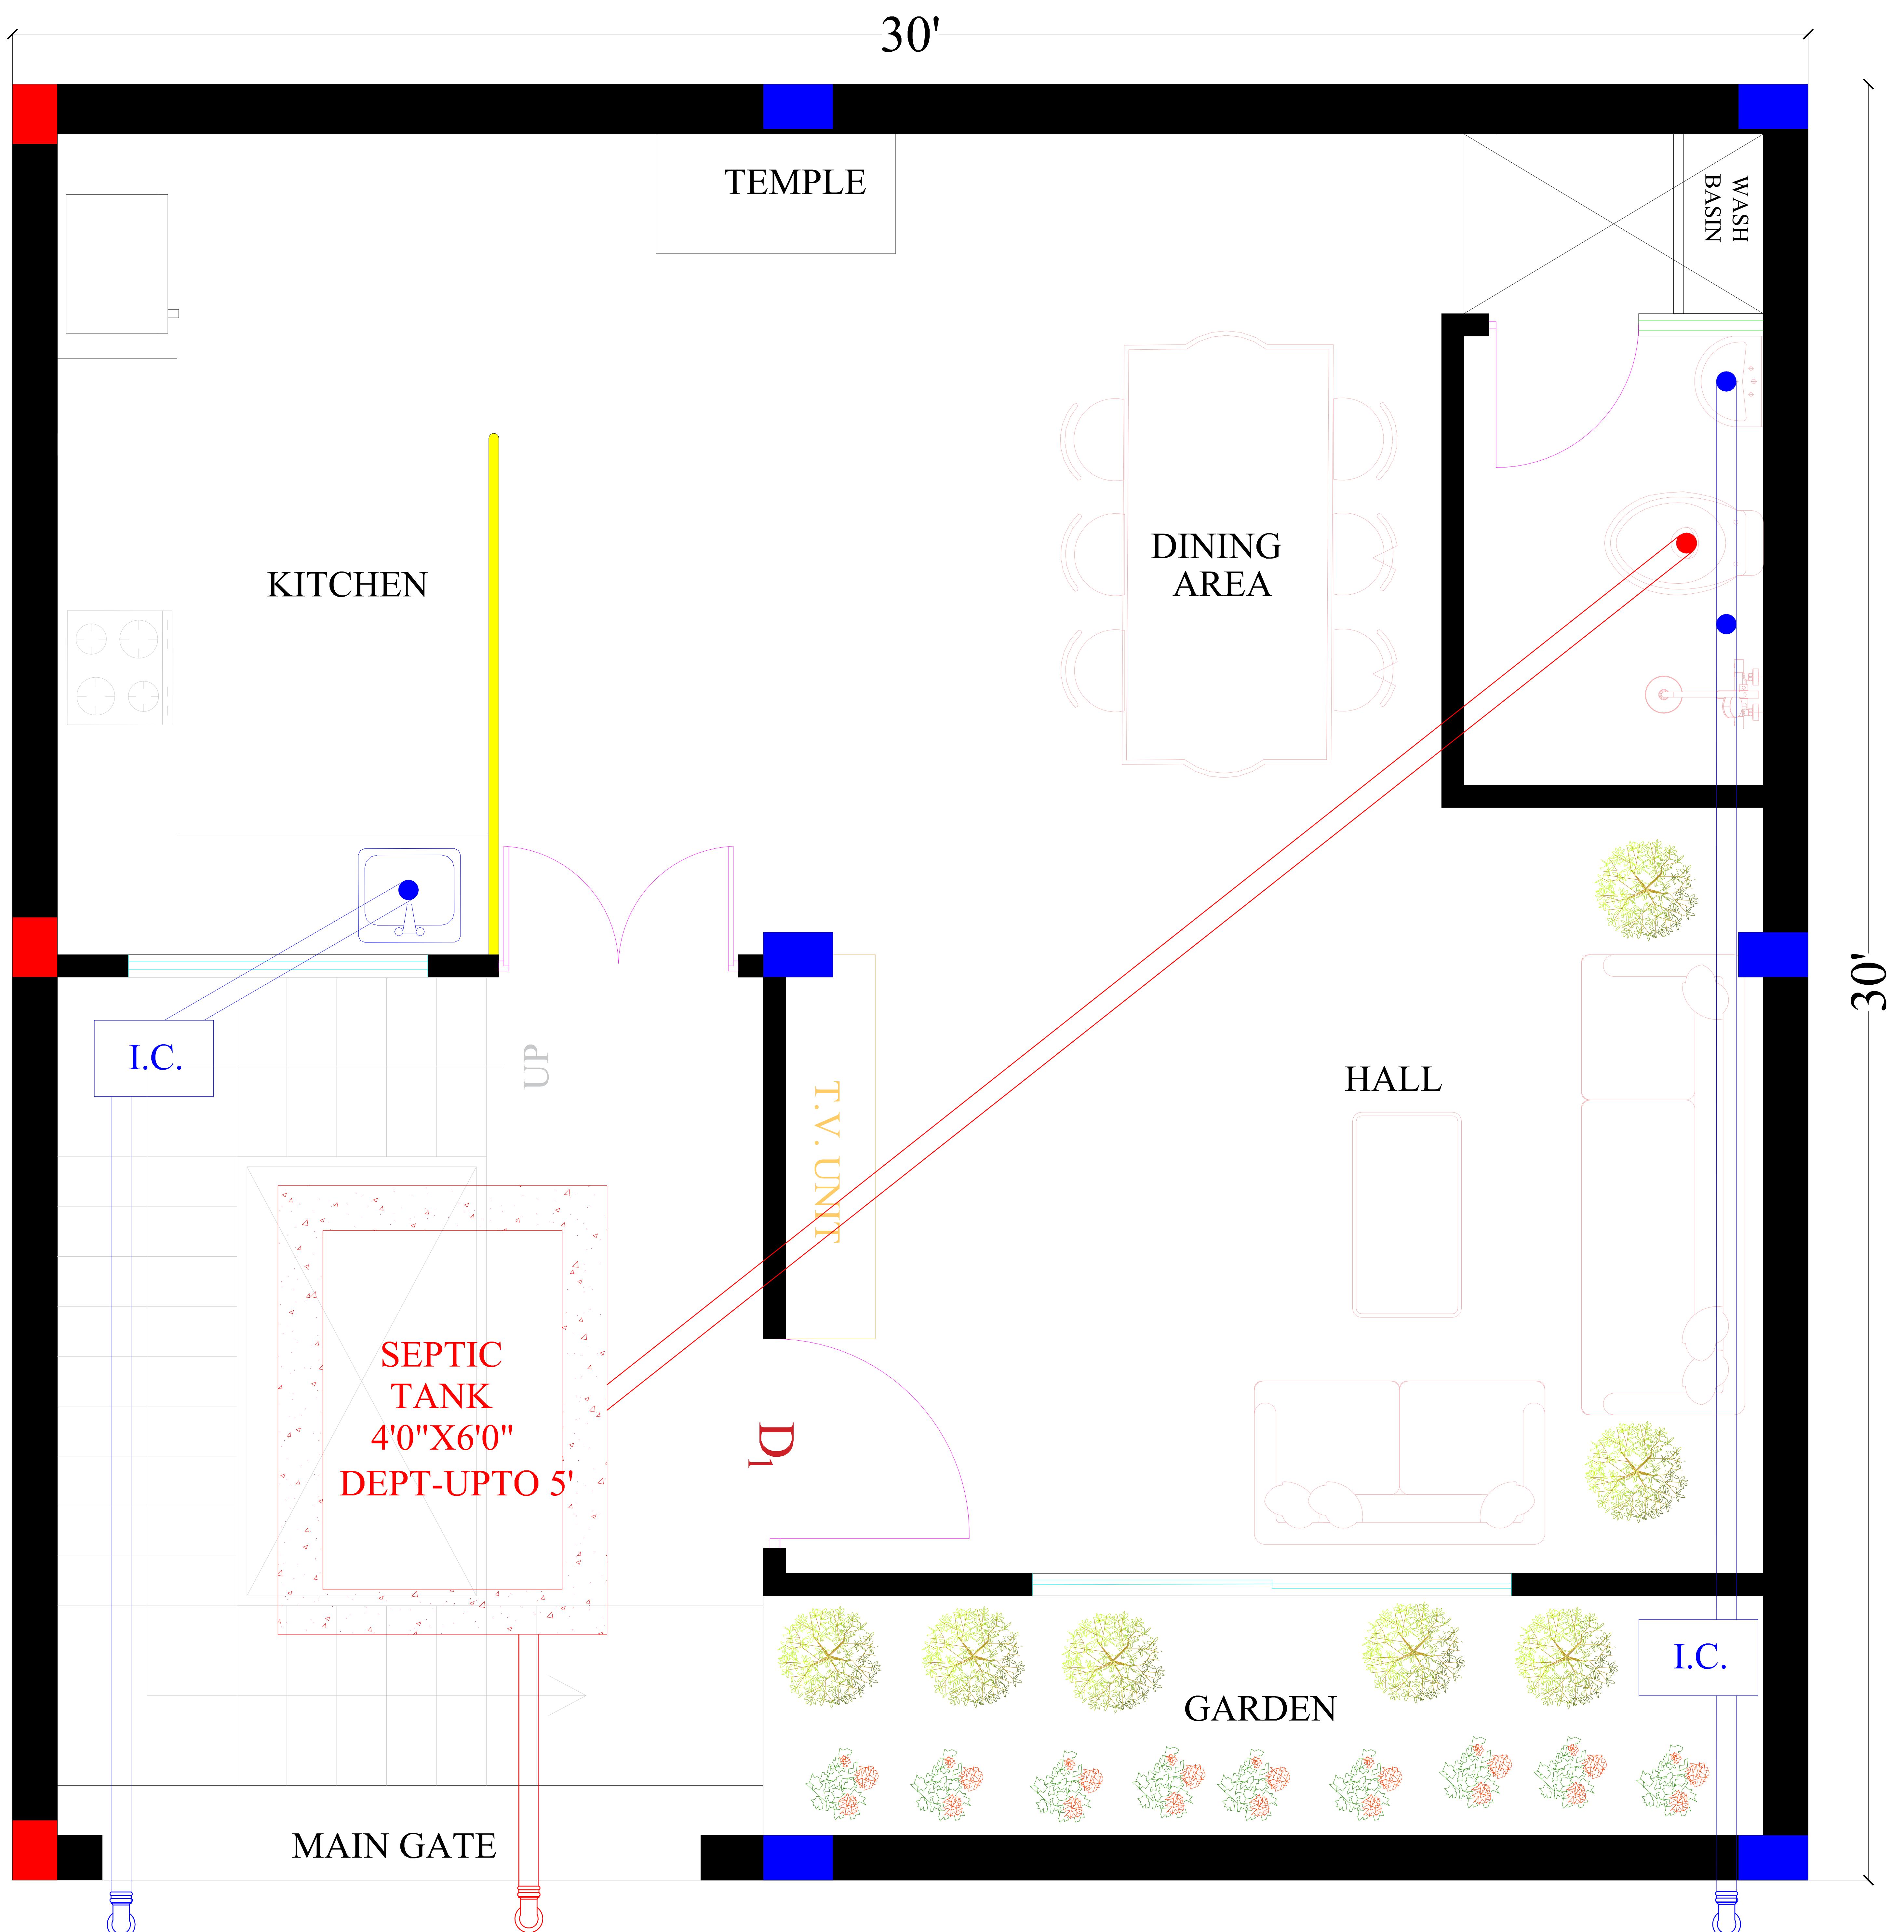

GROUND FLOOR PLUMBING PLAN

This drawing, design & content is property of Architect and shall not be used, copied or reproduced without prior written permission of the firm

Follow the written dimensions only. Do not scale dimensions from drawings. Any discrepancy in the drawing or dimensions should be brought to the attention of architects prior to execution. This drawing should be read in conjunction with other drawings issued for project.

PROJECT	
Project:	Proposed House
Client:	Jhansi U.P., India Mr.Anubhav Sahu
Date :	20/05/2025

Drawn by
ER.Shaalu Gupta

Checked by
Er. Sankalp Tiwari

Date : 20/05/2025

Drawing Status
 conceptual
 for approval
 not for construction
 for construction
 as built
 other _____


Drawing and scale
WORKING


#LayID

Architects

Meerendra Buildcon
ARCHITECTURE PLANNING & INTERIOR DESIGN


Add:- 159/1, Ayodhapuri gwalior road, jhansi (U.P)
Mob:- 9450076030, 8299732040.
E-mail:- meerendra_07@gmail.com

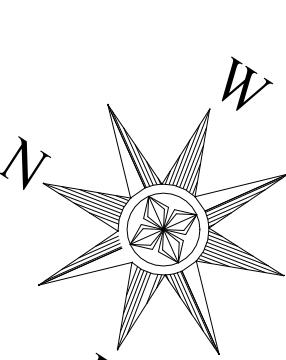

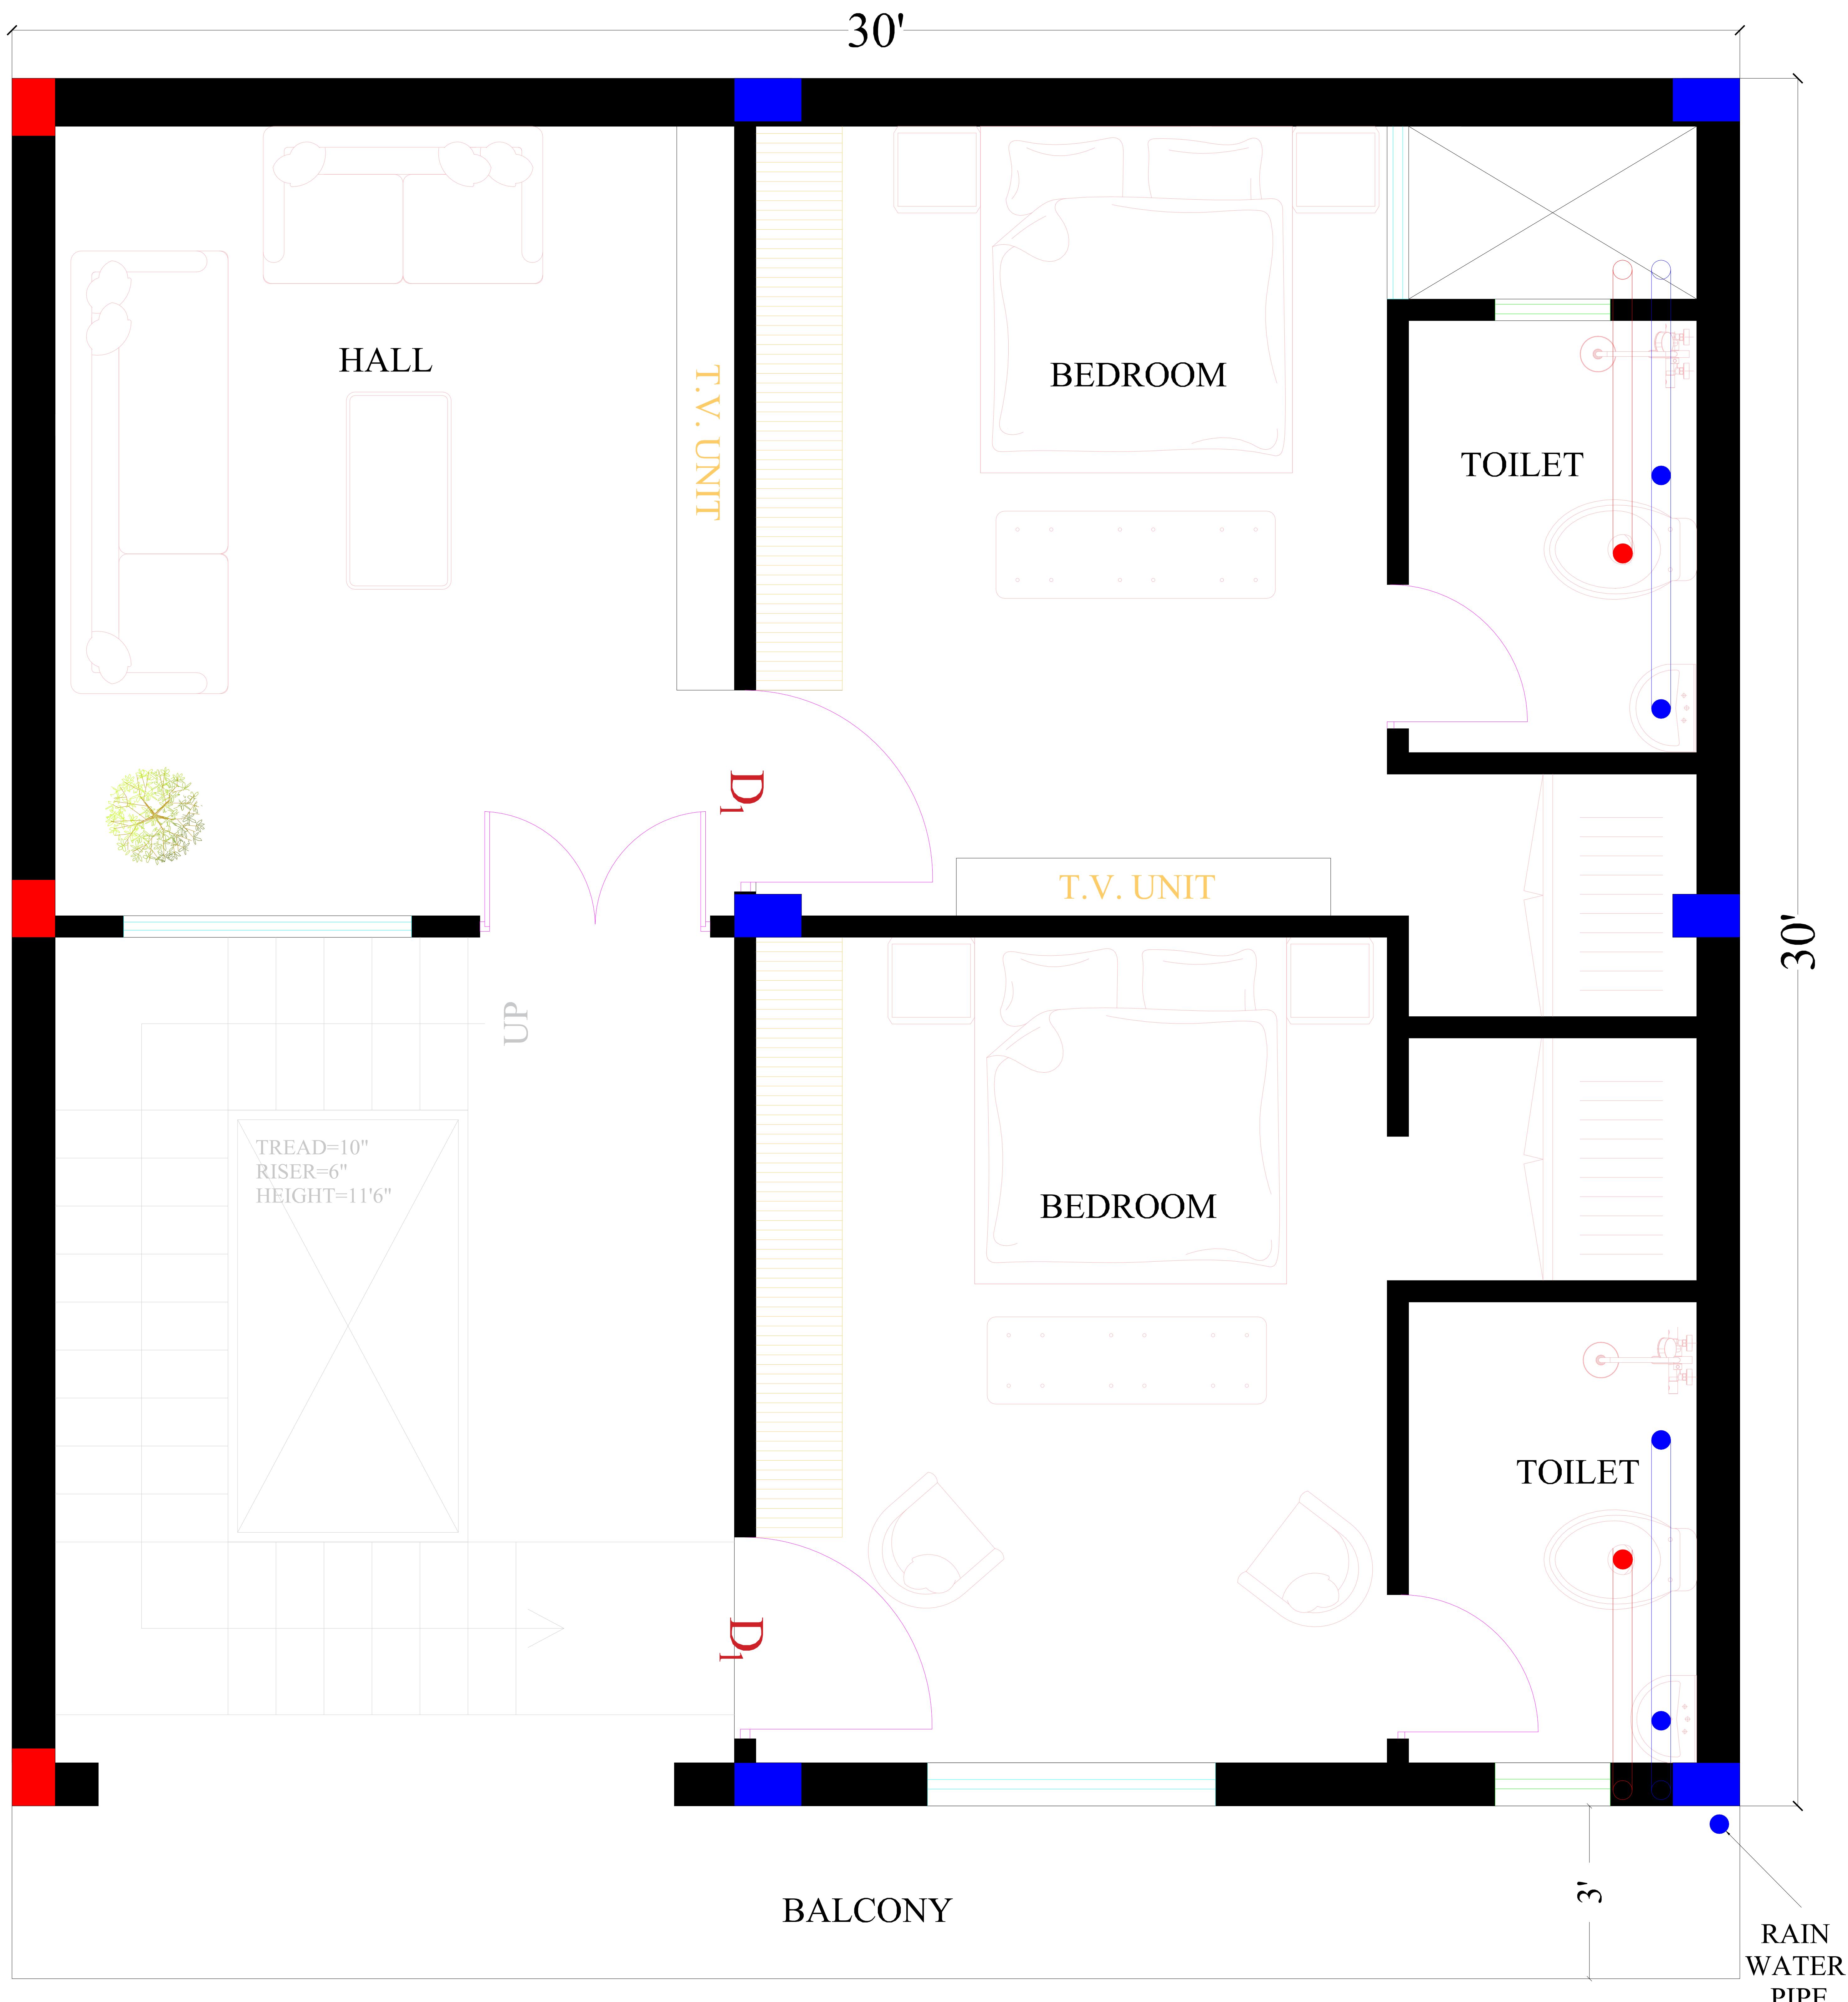

FIRST FLOOR PLUMBING PLAN

PROJECT	Drawn by ER.Shaalu Gupta	Drawing Status	Drawing and scale WORKING	#LayID	Architects
					Project: Proposed House
					Check by Er. Sankalp Tiwari
					Date : 20/05/2025
This drawing, design & content is property of Architect and shall not be used, copied or reproduced without prior written permission of the firm	Client: Mr.Anubhav Sahu	<input checked="" type="checkbox"/> conceptual <input type="checkbox"/> for approval <input type="checkbox"/> not for construction <input type="checkbox"/> for construction <input type="checkbox"/> as built <input type="checkbox"/> other _____			Meerendra Buildcon ARCHITECTURE PLANNING & INTERIOR DESIGN
Follow the written dimensions only. Do not scale dimensions from drawings. Any discrepancy in the drawing or dimensions should be brought to the attention of architects prior to execution. This drawing should be read in conjunction with other drawings issued for project.					Add:- 159/1, Ayodhapuri gwalior road, jhansi (U.P) Mob:- 9450076030, 8299732040. E-mail:- meerendra_07@gmail.com

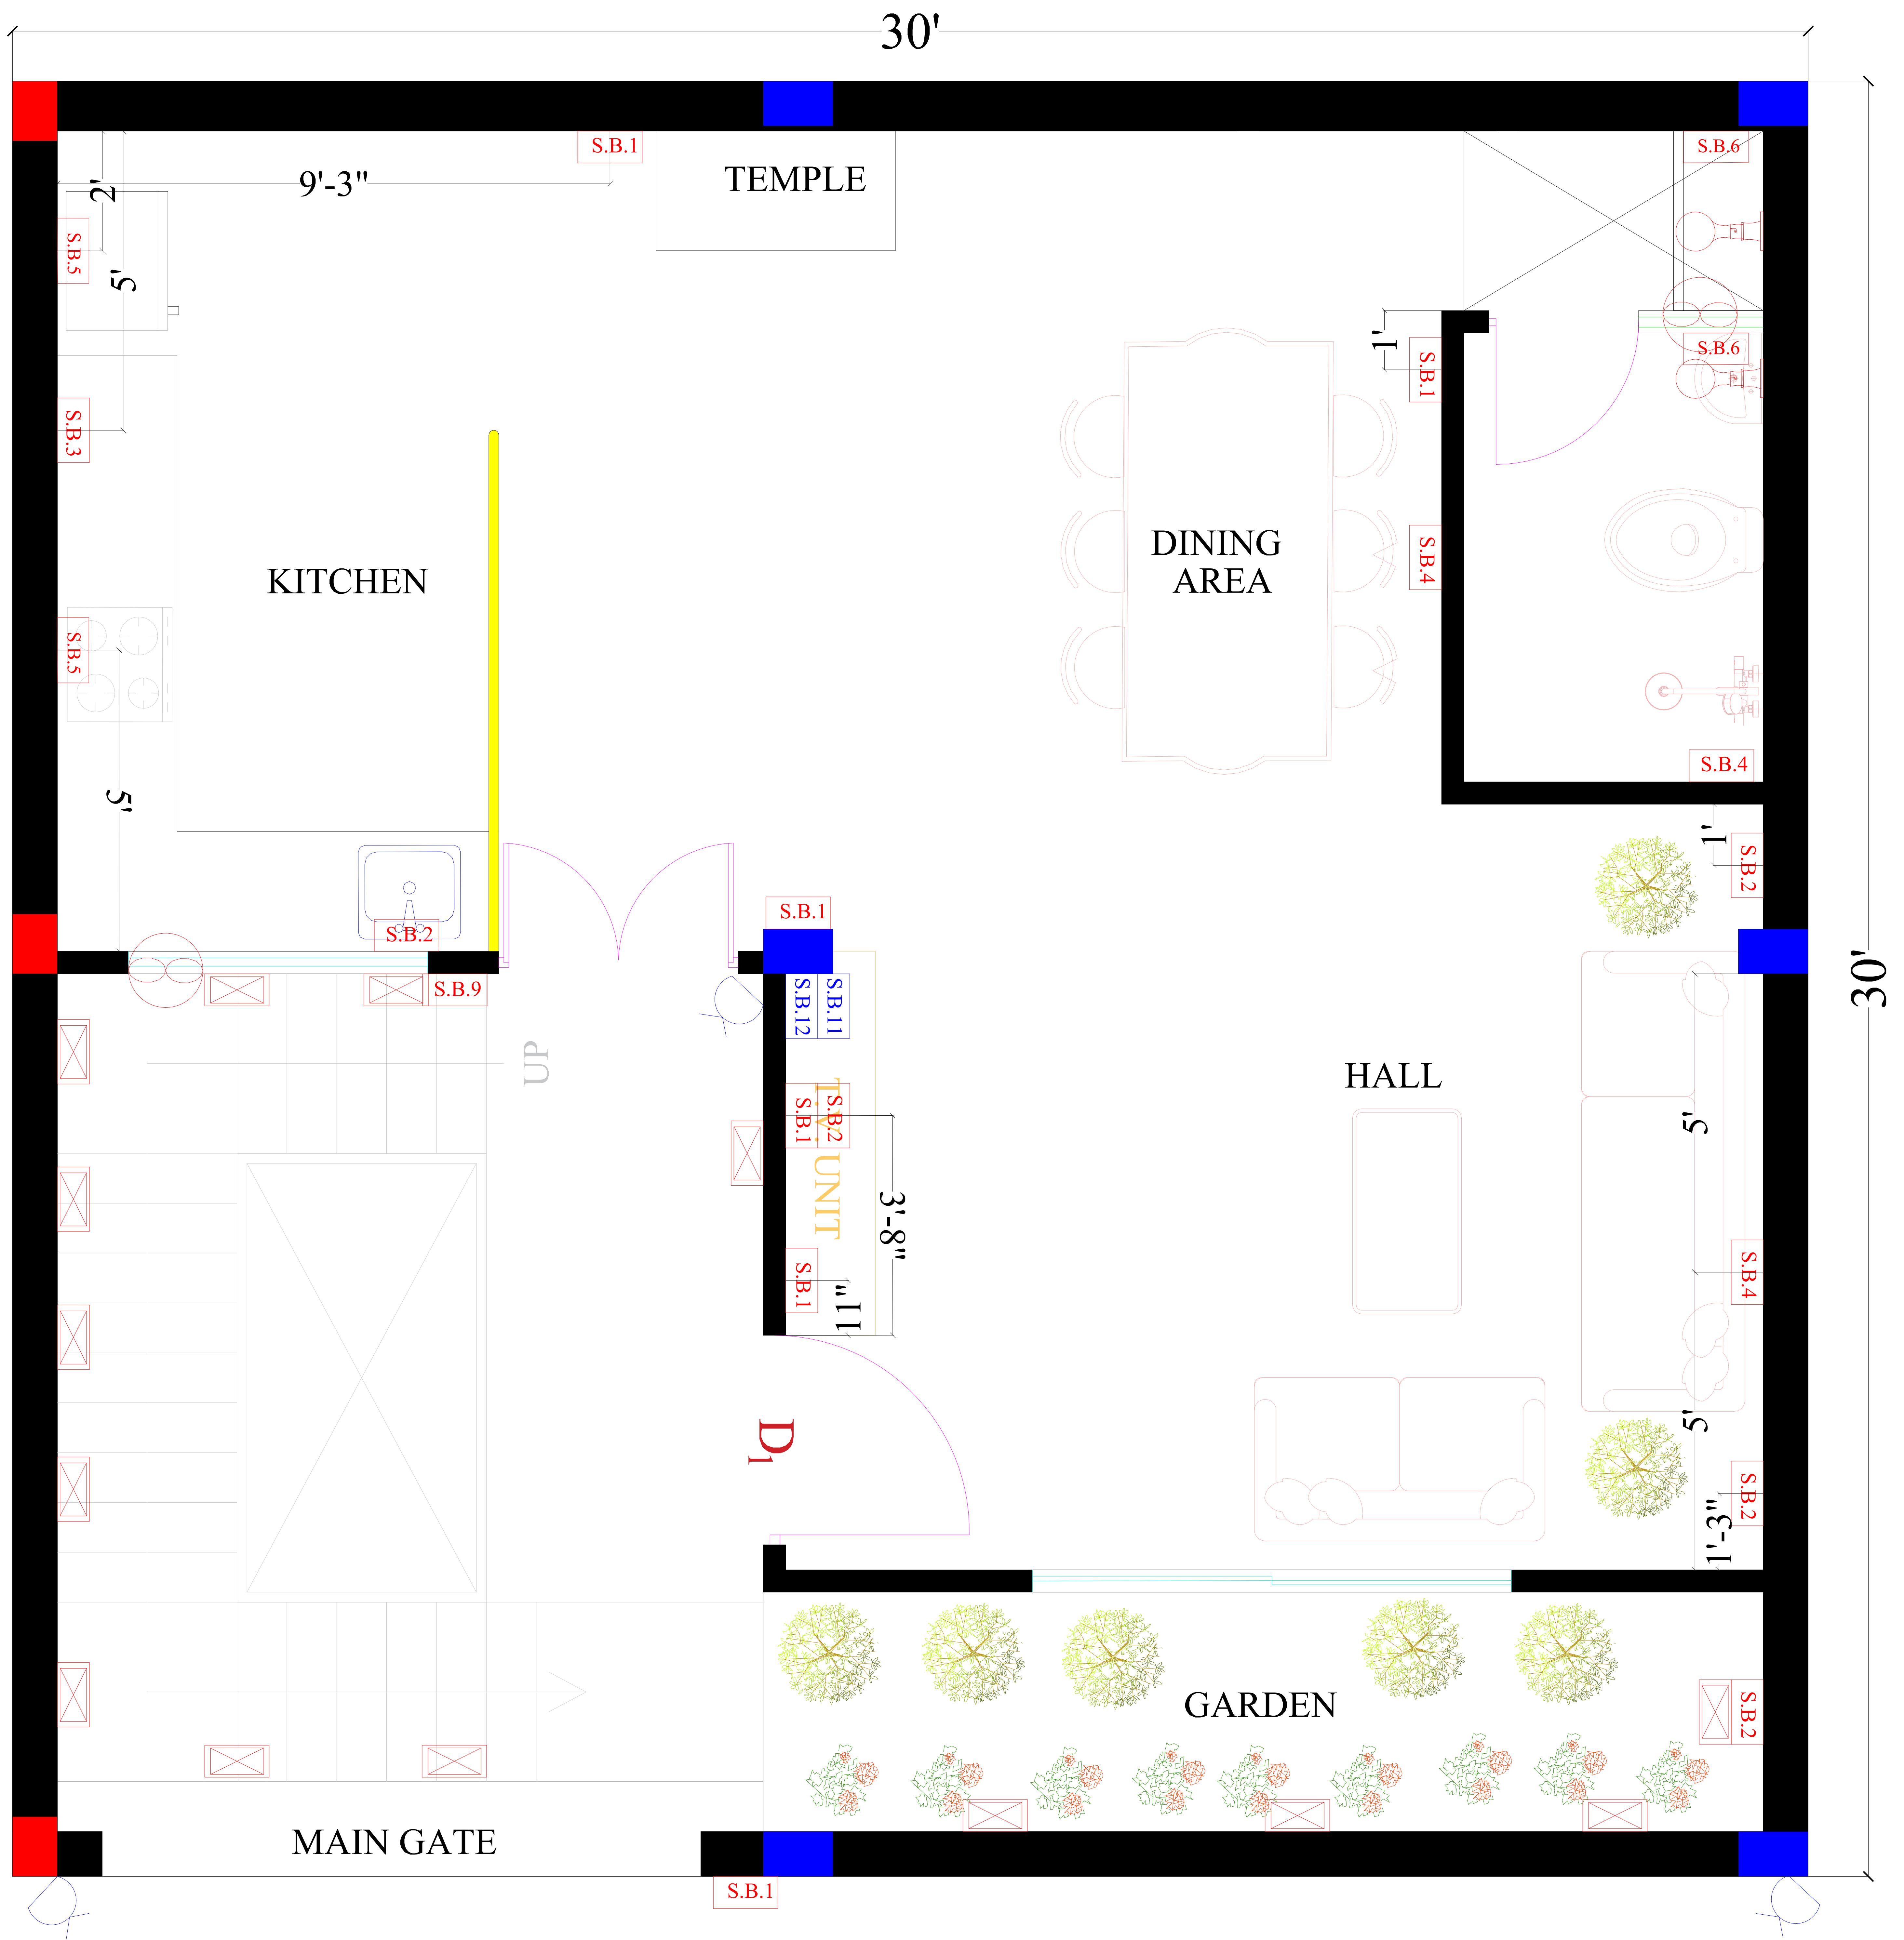

GROUND FLOOR WALL ELECTRICAL PLAN

This drawing, design & content is property of Architect and shall not be used, copied or reproduced without prior written permission of the firm

Follow the written dimensions only. Do not scale dimensions from drawings. Any discrepancy in the drawing or dimensions should be brought to the attention of architects prior to execution. This drawing should be read in conjunction with other drawings issued for project.

PROJECT	
Project:	Proposed House
Client:	Jhansi U.P., India Mr.Anubhav Sahu

Drawn by
ER.Shaalu Gupta

Checked by
Er. Sankalp Tiwari

Date : 20/05/2025

Drawing Status
 conceptual
 for approval
 not for construction
 for construction
 as built
 other _____


Drawing and scale
WORKING

#LayID

Architects

Meerendra Buildcon
ARCHITECTURE PLANNING & INTERIOR DESIGN

Add:- 159/1, Ayodhapuri gwalior road, jhansi (U.P)
Mob:- 9450076030, 8299732040.
E-mail:- meerendra_07@gmail.com

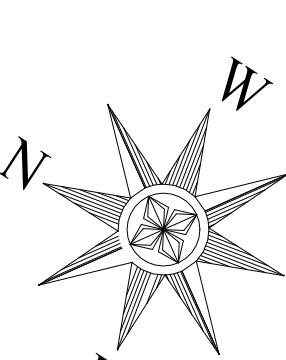



FIRST FLOOR WALL ELECTRICAL PLAN

This drawing, design & content is property of Architect and shall not be used, copied or reproduced without prior written permission of the firm

Follow the written dimensions only. Do not scale dimensions from drawings. Any discrepancy in the drawing or dimensions should be brought to the attention of architects prior to execution. This drawing should be read in conjunction with other drawings issued for project.

PROJECT	
Project:	Proposed House
Client:	Jhansi U.P., India Mr.Anubhav Sahu

Drawn by
ER.Shaalu Gupta

Checked by
Er. Sankalp Tiwari


Date : 20/05/2025

Drawing Status
 conceptual
 for approval
 not for construction
 for construction
 as built
 other _____






Drawing and scale
WORKING
#LayID


Architects
Meerendra Buildcon
ARCHITECTURE PLANNING & INTERIOR DESIGN

Add:- 159/1, Ayodhapuri gwalior road, jhansi (U.P)
Mob:- 9450076030, 8299732040.
E-mail:- meerendra_07@gmail.com

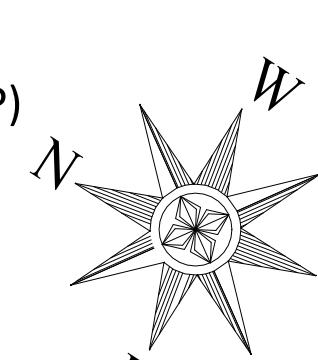

RESIDENCE:-

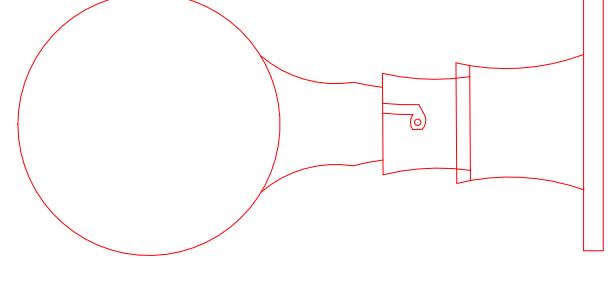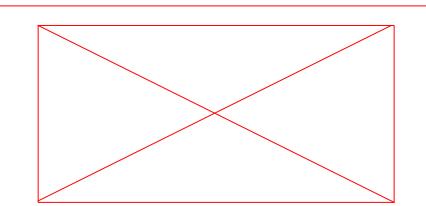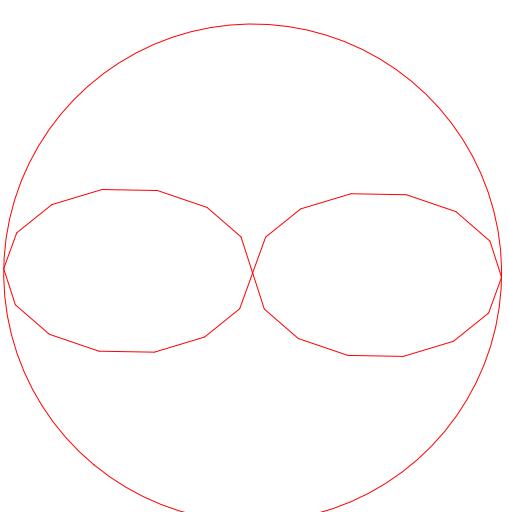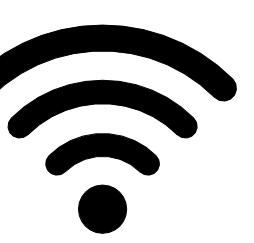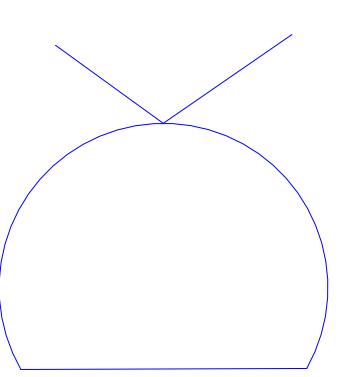NAME	LEGEND
Bulb Point (Height-7'6")	
Switch Board (Height-42")	S.B.1
Switch Board (Height-24")	S.B.2
Switch Board (Height-38")	S.B.3
15 Amp Socket (Height-Above Door)	S.B.4
15 Amp Socket (Height-44")	S.B.5
Switch Board (Height-48")	S.B.6
Switch Board (Height-5'-6")	S.B.7
Bell Point 15 AMP Socket 1 Feet Below Seeling	S.B.8
Switch Board 2 way Board (Height-42")	S.B.9
Foot Light (Height-1'-6")	
Exhust Fan	
Switch Board (Height-9'0")	S.B.11
WIFI (Height-9'0") 	S.B.12
CCTV CAMERA	

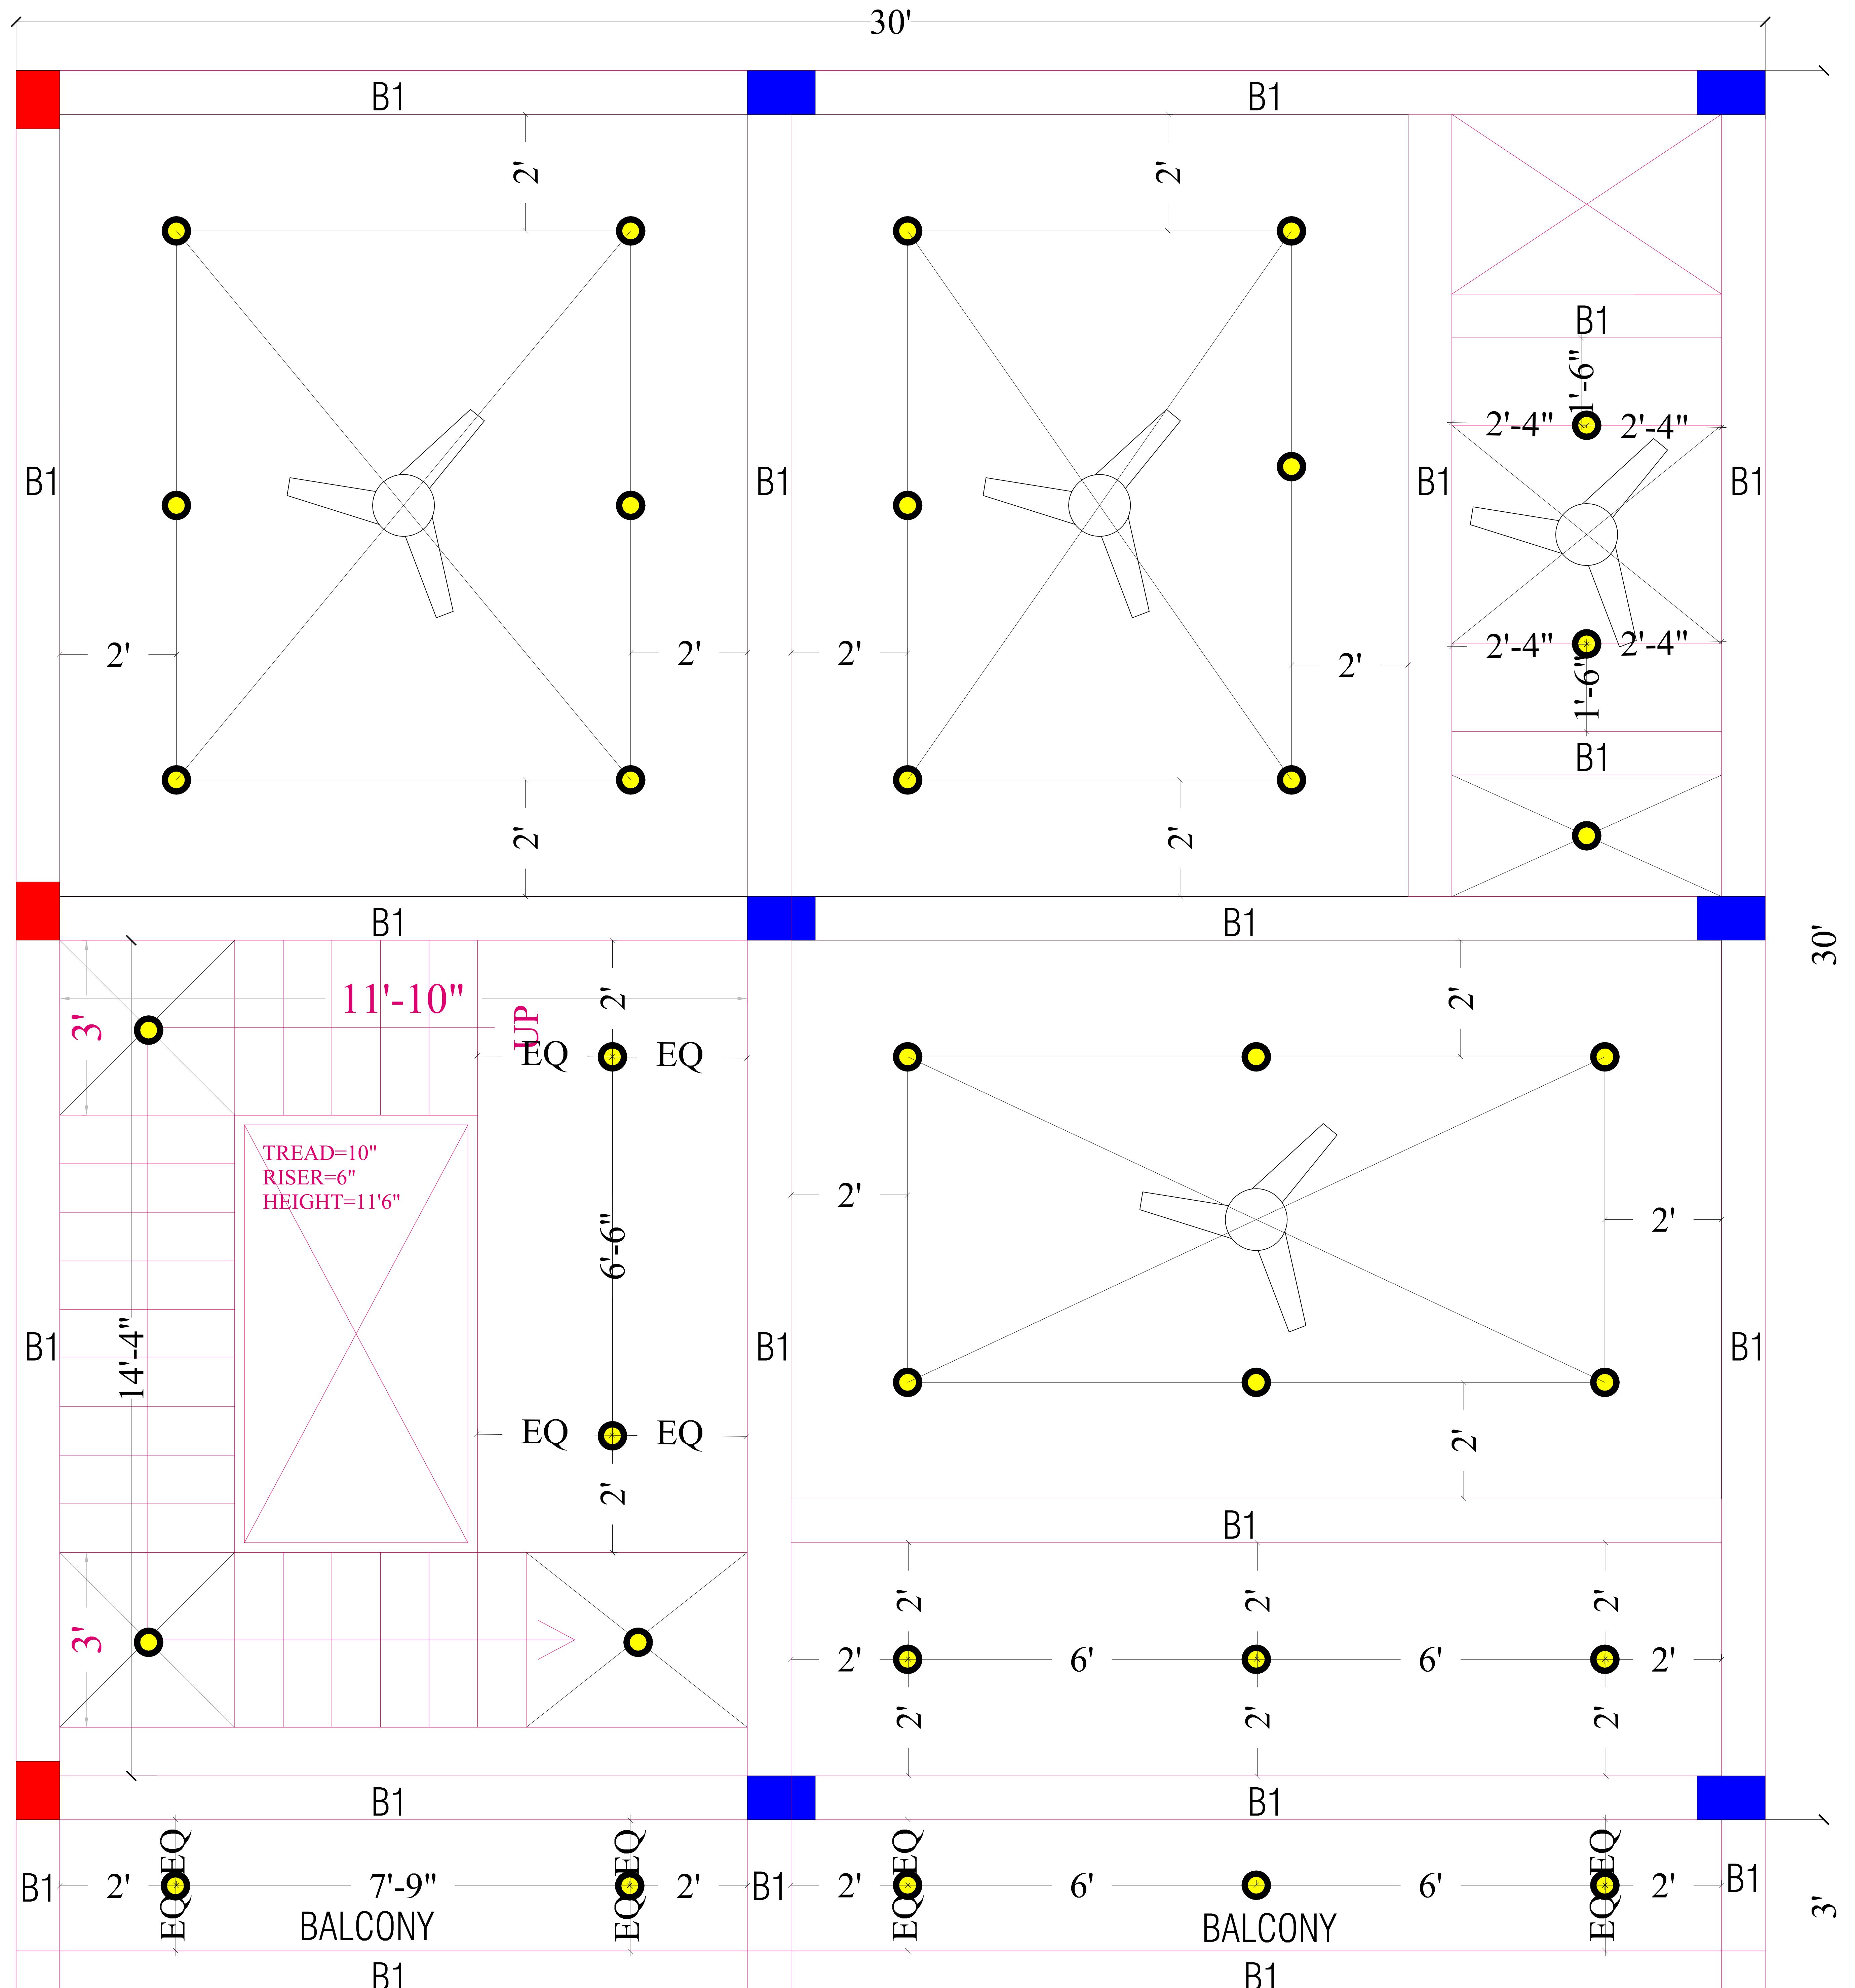

GROUND FLOOR CEILING ELECTRICAL PLAN

This drawing, design & content is property of Architect and shall not be used, copied or reproduced without prior written permission of the firm

Follow the written dimensions only. Do not scale dimensions from drawings. Any discrepancy in the drawing or dimensions should be brought to the attention of architects prior to execution. This drawing should be read in conjunction with other drawings issued for project.

PROJECT	
Project:	Proposed House
Client:	Mr.Anubhav Sahu
Jhansi U.P., India	

Drawn by
ER.Shaalu Gupta

Checked by
Er. Sankalp Tiwari

Date : 20/05/2025

Drawing Status
<input checked="" type="checkbox"/> conceptual
<input type="checkbox"/> for approval
<input type="checkbox"/> not for construction
<input type="checkbox"/> for construction
<input type="checkbox"/> as built
<input type="checkbox"/> other _____


Drawing and scale


WORKING

#LayID

Architects
Meerendra Buildcon
ARCHITECTURE PLANNING & INTERIOR DESIGN

Add:- 159/1, Ayodhapuri gwalior road, jhansi (U.P)
Mob:- 9450076030, 8299732040.
E-mail:- meerendra_07@gmail.com

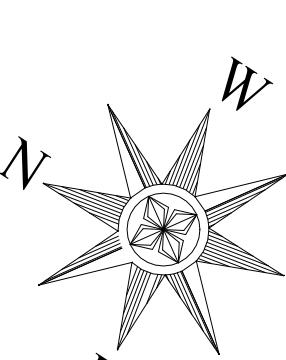

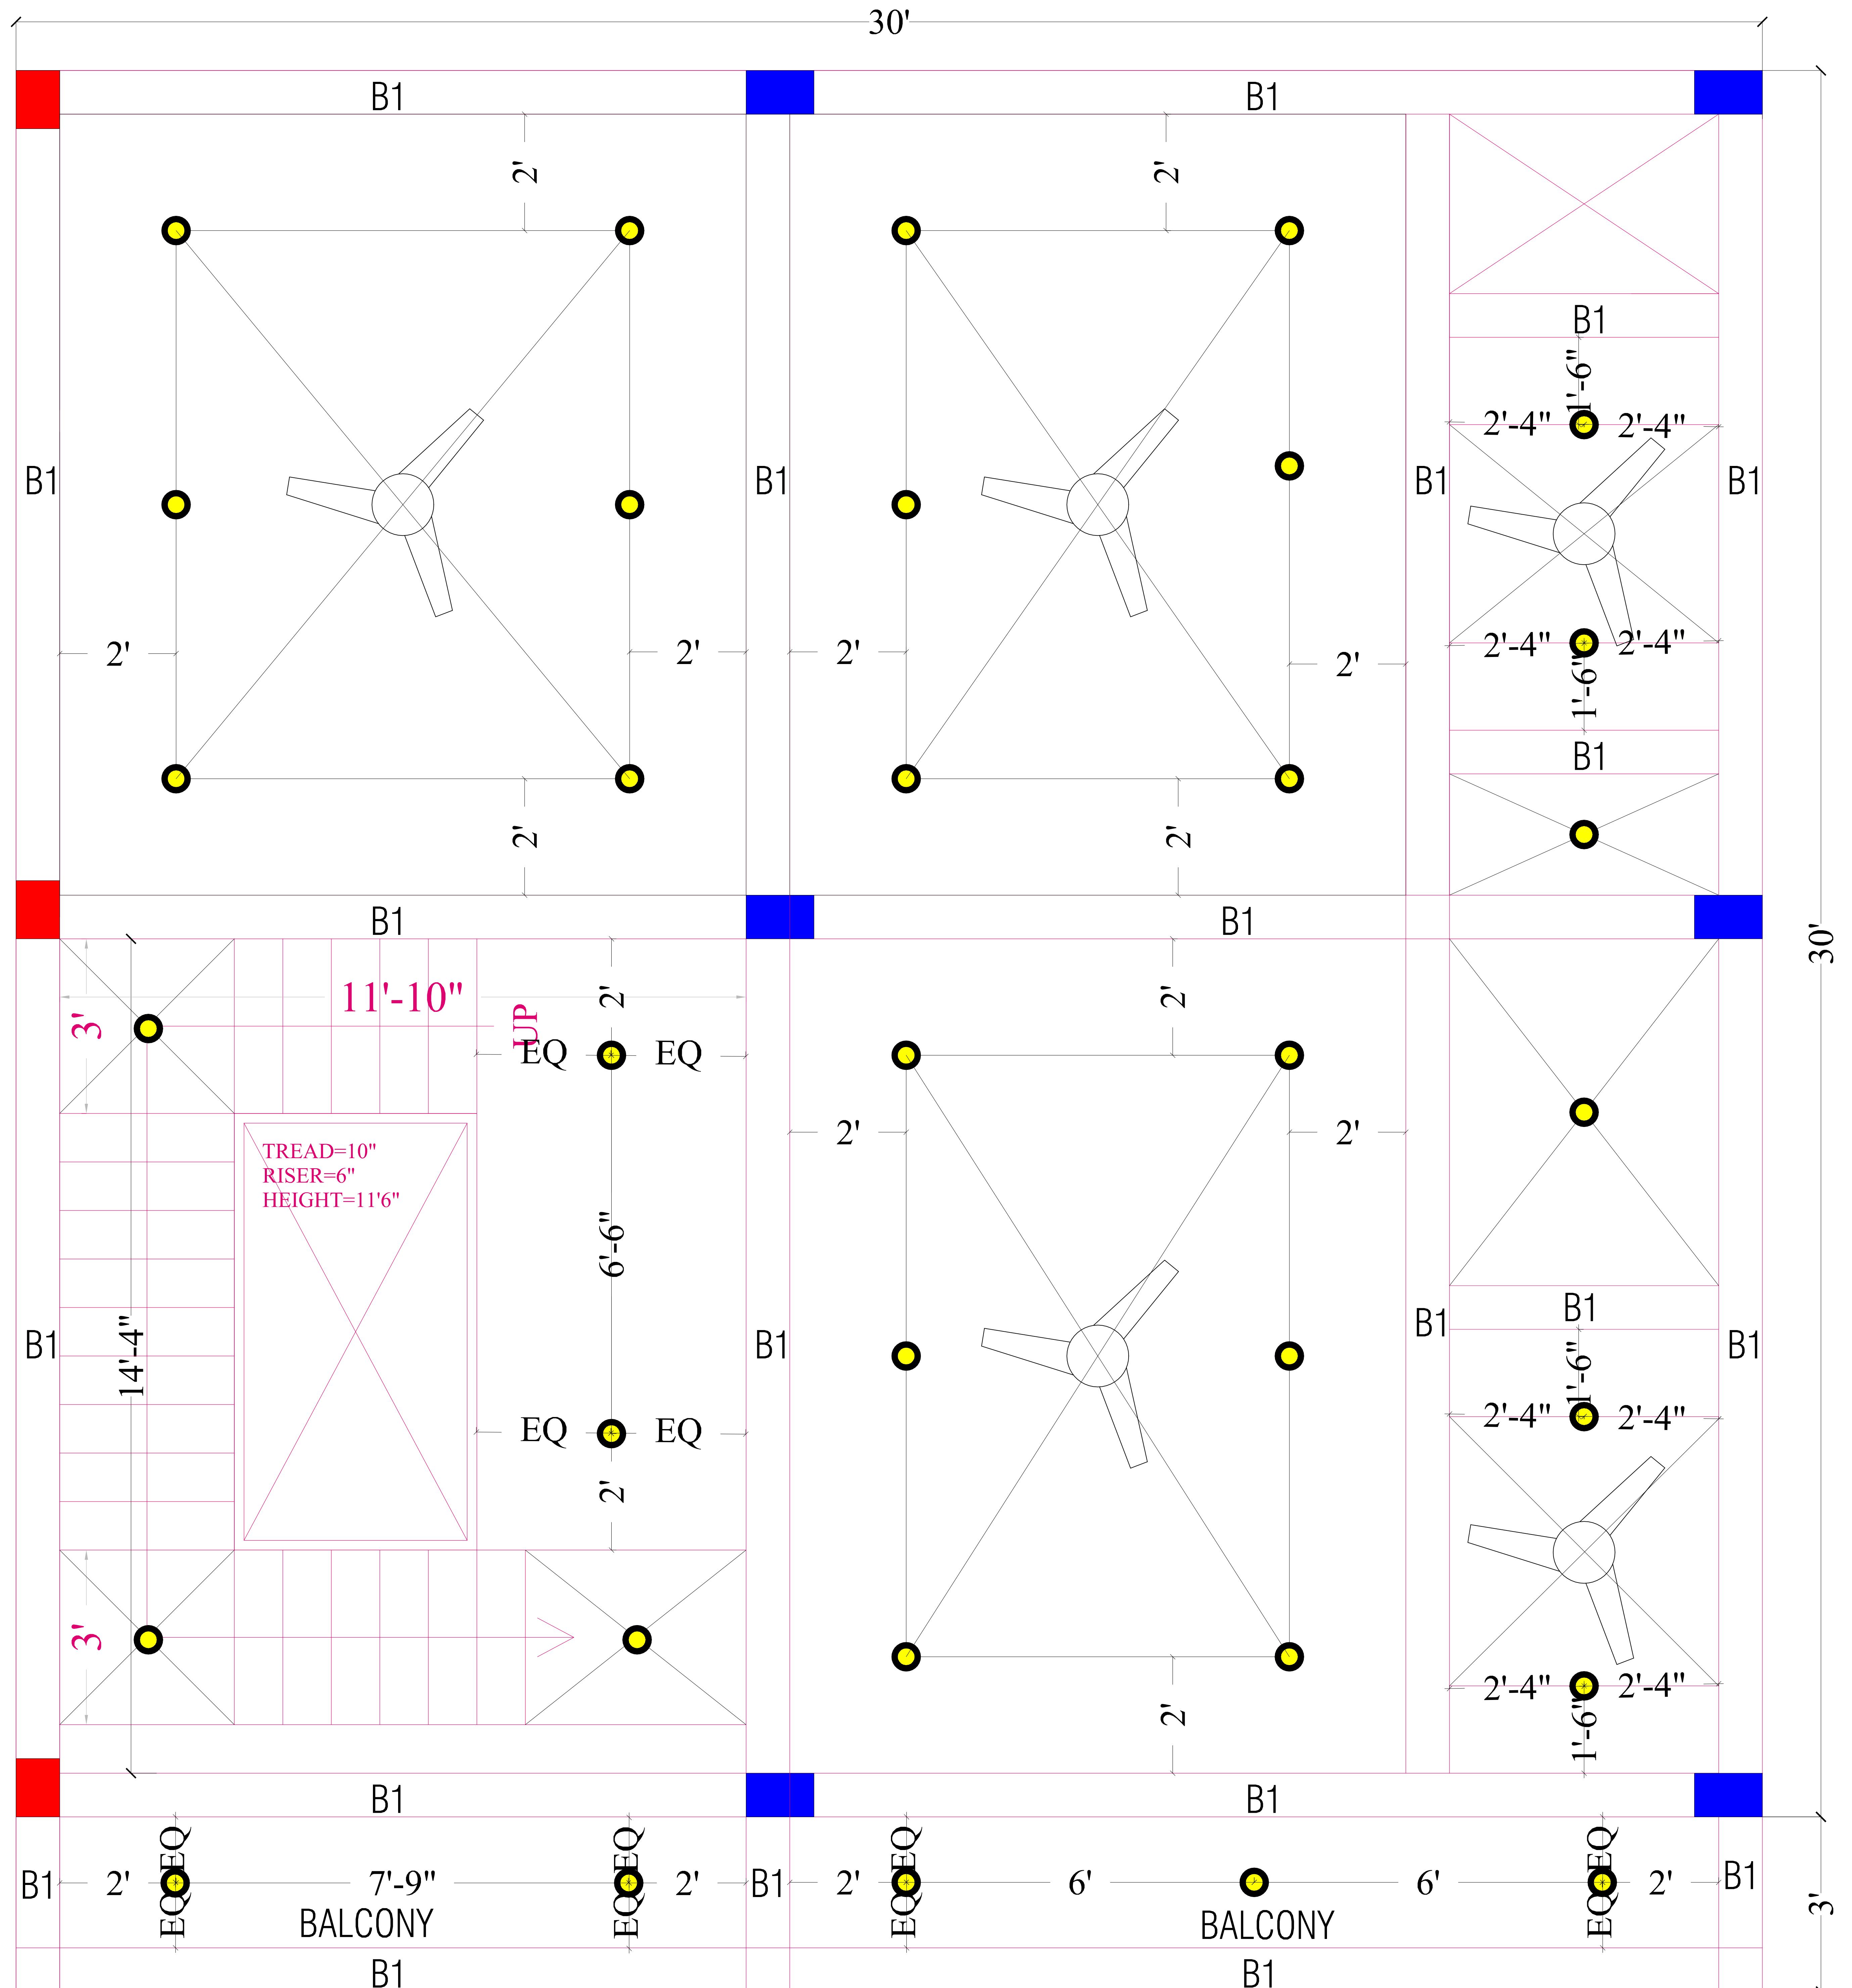

FIRST FLOOR CEILING ELECTRICAL PLAN

This drawing, design & content is property of Architect and shall not be used, copied or reproduced without prior written permission of the firm

Follow the written dimensions only. Do not scale dimensions from drawings. Any discrepancy in the drawing or dimensions should be brought to the attention of architects prior to execution. This drawing should be read in conjunction with other drawings issued for project.

PROJECT
Project: Proposed House
Client: Mr.Anubhav Sahu
Jhansi
U.P., India

Drawn by
ER.Shaalu Gupta

Checked by
Er. Sankalp Tiwari

Date : 20/05/2025

Drawing Status
 conceptual
 for approval
 not for construction
 for construction
 as built
 other _____

Drawing and scale
WORKING

#LayID

Architects
Meerendra Buildcon
ARCHITECTURE PLANNING & INTERIOR DESIGN

Add:- 159/1, Ayodhapuri gwalior road, jhansi (U.P)
Mob:- 9450076030, 8299732040.
E-mail:- meerendra_07@gmail.com

